POWELL DUPLEX IMPROVEMENTS

NEZ PERCE-CLEARWATER NATIONAL FORESTS
LOCHSA-POWELL RANGER DISTRICT,
192 POWELL RD, LOLO, MONTANA
IDAHO COUNTY



SHEET INDEX

ARCHITECTURAL DRAWINGS

A000	COVER
A001	GENERAL INFORMATION & ASSEMBLY TYPES
A100	DEMOLITION PLANS
A101	LEVEL 1 FLOOR PLAN
A102	LEVEL 2 FLOOR PLAN
A103	ROOF PLAN
A104	REFLECTED CEILING PLANS
A201	EXTERIOR ELEVATIONS
A301	BUILDING SECTIONS
A302	BUILDING SECTIONS
A401	EXTERIOR DETAILS
A701	DOOR & FINISH SCHEDULE

STRUCTURAL DRAWINGS

S001	GENERAL STRUCTURAL NOTES
S002	GENERAL STRUCTURAL NOTES, ANNOTATIONS AND SYMBOLS & ABBREVIATIONS
S101	FOUNDATION/MAIN FLOOR STRUCTURAL PLAN
S102	ROOF STRUCTURAL PLAN
S701	TYPICAL DETAILS

MECHANICAL DRAWINGS

M000	MECHANICAL LEGEND AND NOTES
M001	MECHANICAL SCHEDULES
M101	LEVEL 1 MECHANICAL DEMOLITION PLAN
M102	LEVEL 2 MECHANICAL DEMOLITION PLAN
M201	LEVEL 1 MECHANICAL PLAN
M202	LEVEL 2 MECHANICAL PLAN


PLUMBING DRAWINGS

P000	PLUMBING LEGEND AND NOTES
P001	PLUMBING SCHEDULES
P101	LEVEL 1 PLUMBING DEMOLITION
P102	LEVEL 2 DEMOLITION PLAN
P201	LEVEL 1 PLUMBING PLAN
P202	LEVEL 2 PLUMBING PLAN

ELECTRICAL DRAWINGS

E000	ELECTRICAL SYMBOLS AND ABBREVIATIONS
E001	ELECTRICAL DETAILS
E102	LEVEL 1 ELECTRICAL DEMOLITION PLAN
E106	LEVEL 1 POWER PLAN
E108	LEVEL 1 LIGHTING PLAN

VICINITY MAP NOT TO SCALE

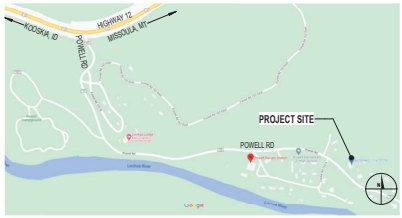

PROJECT DESCRIPTION

REPLACEMENT OF METAL ROOF, AND OF WATER-DAMAGED SIP PANELS AND STRUCTURAL MEMBERS IN THE ROOF AND WALLS OF AN EXISTING RESIDENTIAL DUPLEX. OTHER MINOR REPAIRS AND UPGRADES NECESSARY TO RETURN THIS BUILDING TO SERVICE ARE ALSO INCLUDED. BUILDING AREA: 2600 SF FIRST FLOOR = 1327 SF SECOND FLOOR = 3927 SF TOTAL.

PROJECT DIRECTORY

ARCHITECT:

MOSAIC ARCHITECTURE, P.C.
317 CRUSE AVE., SUITE 201
HELENA, MT 59601
(406) 449-2013
CONTACT: JEFF DOWNHOUR, AIA jeff@mosaicarch.com

MECHANICAL/ELECTRICAL/PLUMBING ENGINEERING:

MORRISON MAIERLE
1055 Mount Avenue
Missoula MT 59801
406.542.8880
ELECTRICAL CONTACT: Garth Stevens gstevens@m-m.net
MECHANICAL/PLUMBING: Jason Beaudette jbeaudette@m-m.net

STRUCTURAL ENGINEERING:

MORRISON MAIERLE
1 Engineering Pl
Helena, MT 59602
406.442.3050
CONTACT: Aubrey Yerger ayerger@m-m.net

APPROVED:

Heath Perrine — Digitally signed by Heath Perrine
DEPUTY FOREST SUPERVISOR — DATE
NEZ PERCE-CLEARWATER NATIONAL FORESTS

CORRINE KEGEL — Digitally signed by CORRINE KEGEL Date: 2025.06.09 11:49:12 -06'00'
DIRECTOR OF ENGINEERING — DATE
NORTHERN REGION

RECOMMENDED:

SUSAN GRAVES — Digitally signed by SUSAN GRAVES Date: 2025.05.14 14:42:39 -07'00'
FOREST ENGINEER — DATE
NEZ-PERCE-CLEARWATER NATIONAL FORESTS

DISTRICT RANGER — DATE
LOCHSA POWELL RANGER DISTRICT

BRANDON KNAPTON — KNAPTON Date: 2025.05.15 15:44:09 -07'00' Digitally signed by BRANDON

THESE DRAWINGS WERE PREPARED BY MOSAIC ARCHITECTURE, P.C. FOR CONSTRUCTION OF THE PROJECT DESCRIBED HEREIN. AS SUCH, THE DOCUMENTS ARE THE PROPERTY OF MOSAIC ARCHITECTURE, P.C. & MAY NOT BE REPRODUCED, COPIED OR USED IN ANY WAY WITHOUT PRIOR APPROVAL FROM MOSAIC ARCHITECTURE, P.C.

mosaic architecture-planning-design
317 Cruse Avenue Suite 201
Helena, Montana 59601
406.449.2013
www.mosaicarch.com

LICENSED ARCHITECT AR-986501
JEFFERY R. DOWNHOUR
STATE OF IDAHO

U.S. DEPARTMENT OF AGRICULTURE
FOREST SERVICE
R-1 NORTHERN REGION

POWELL DUPLEX RENOVATION

LOCHSA-POWELL RANGER DISTRICT
192 POWELL RD, LOLO, MT 59847
NEZ PERCE-CLEARWATER NATIONAL FORESTS
CONSTRUCTION DOCUMENTS

MARK	DATE	REVISION

PROJECT NO. 1240LU23F0138
DATE: 7/19/2024
Drawn By: Mosaic
Designed By: Mosaic
Checked By: Mosaic

COVER


SHEET: A000

DATE STAMP: 7/19/2024 10:18:39 AM

ABBREVIATIONS:

@	at	FA	fire alarm/floor-ceiling assembly	PTDR	paper towel dispenser/receptacle		
A.B.	anchor bolt	FAH	fire alarm horn	PVMT	pavement		
A/C	air conditioning	FAS	fire alarm station	PVC	polyvinylchloride		
ACC PNL	access panel	FD	floor drain	QTY	quantity		
ACOUST	acoustical	FDN/FND	foundation	R/RAD	radius		
ACT	acoustical ceiling tile	FE	fire extinguisher	R	riser		
AD	area drain	FEC	fire extinguisher cabinet	RA	roof/ceiling assembly		
ADJ	adjacent	FF	finished floor	RB	rubber base		
AFF	above finished floor	FFHB	frost free hose bib	RD	roof drain		
AIB	air infiltration barrier	FG	finish grade	RE	regarding		
ALT	alternate	FH	fire hydrant	REF	reference/refrigerator		
ALUM	aluminum	FIN. FLR	top of floor sheathing	REINF	reinforcing		
ANOD	anodized	FIN	finish	REQD	required		
APPROX	approximate	FIXT	fixture	RES	resilient		
ARCH	architect	F.O.	face of	RM	room		
AUTO	automatic	FLR/FL	floor	RO	rough opening		
BBD	bulletin board	FLUOR	fluorescent	RV	roof vent		
BD	board	FND	feminine napkin dispenser/disposal	R&S	rod and shelf		
BITUM	bituminous	FOC	face of concrete	S	south		
BL	building line	FOF	face of finish	SACT	suspended acoustical ceiling tile		
BLDG	building	FOS	face of stud	SC	solid core		
BLK	block	FOW	face of wall	SCD	seat cover dispenser		
BLKG	blocking	FT	foot or feet	SCHED	schedule		
BM	beam/bench mark	FTG	footing	SD	soap dispenser		
BO	by owner	GA	gauge	SECT	section		
B.O.	bottom of	GB	grab bar	SF	square feet		
BOT	bottom	GALV	galvanized	SGL	single		
BRG	bearing	G.C.	general contractor	SHT	sheet		
BSBD	baseboard	GEN	general	SHTG	sheathing		
BTWN	between	GFRG	glass fiber reinforced gypsum	SHWR	shower		
B.O.W.	bottom of wall	GI	galvanized iron	SIM.	similar		
BU	built up	GL	glass	S.I.P.	structural insulated panel		
CAB	cabinet	GLU LAM	or G.L.B. glue laminated beam	SLNT	sealant		
CAP	capacity	GRD	grade/grid	SOG	slab on grade		
CB	catch basin	GWB	gypsum wall board	SPEC	specifications		
CL	centerline	GYP	gypsum	S.S.	stainless steel		
C.C.	center to center	HB	hose bib	SS	service sink		
CDX	exterior grade plywood	HC	hollow core/handicapped	SSM	solid surface material		
CG	corner guard	HD BD	Hard board	STD	standard		
CH	channel	HDR	header	STF	storefront		
CI	cast iron/cubic inches	HOR	horizontal	STL	steel		
CJ	control joint	HR	hour	STOR	storage		
CLG	ceiling	HT	height	STRUCT	structural		
C.L.L.	contract limit line	HTG	heating	SUBFLR	subfloor		
CL	center line	HVAC	heating, ventilation, air conditioning	SUSP	suspended		
CLR	clear	HW	hot water	SV	sheet vinyl		
CMU	concrete masonry unit	IN	inch	SY	square yard		
CO	clean out	INCL	included	T	tread/thermostat		
COL	column	INFO	information	TB	towel bar		
CONC	concrete	INSUL	insulation	TEL	telephone		
COND	condition	INT	interior	TEMP	temperature		
CONF	conference	IWA/IW	interior wall assembly	T&G	tongue and groove		
CONN	connection	JAN	janitor	THK	thick		
CONST	construction	JST	joist	THRU	through		
CTRD	centered	JT	joint	TJI	Truss Joist Incorporated		
CONT	continuous	LAV	lavatory	T.O.	top of		
CONTR	contractor	LF	lineal foot	T.O.B.	top of beam		
CORR	corridor	LTG	lighting	T.O.C.	top of concrete		
CPT	carpet	M	men's	T.O.P.	top of plate		
CT	ceramic tile	MAT	material	T.O. FTG	top of footing		
CUH	cabinet unit heater	MAX	maximum	T.O.S.	top of steel		
CW	curtain wall system	MECH	mechanical	T.O.SL.	top of slab		
CY	cubic yard	MDF	medium density fiber board	T.O.W.	top of wall		
DBL	double	MEMB	membrane	TPD	toilet paper dispenser		
DEPT	department	MEZZ	mezzanine	TR	tread		
DF	drinking fountain	MFR	manufacturer	TS	tubular steel		
DIA	diameter	MH	manhole	TV	television		
DIAG	diagonal	MIN	minimum	TYP	typical		
DIM	dimension	MIR	mirror	UG	underground		
DISP	dispenser	MISC	miscellaneous	UNO	unless noted otherwise		
DN	down	MO	masonry opening	UR	urinal		
DR	door	MTL	metal	VAC	vacuum outlet		
DWR	drawer	MULL	mullion	VAR	varies		
DS	downspout	N	north	VB	vapor barrier		
DTL	detail	NA	not applicable	VCT	vinyl composition tile		
DWG	drawing	NIC	not in contract	VERT	vertical		
E	east	NO	number	VEST	vestibule		
EA	each	NTS	not to scale	VFY	verify		
EIFS	exterior insulation finish system	OFCI	owner furnished/contractor installed	VT	vinyl tile		
E.J.	expansion joint	OC	on center	VWC	vinyl wall covering		
EL/ELEV	elevation - height/elevator	OD	outside diameter	W	west/women/width		
ELEC	electrical	OH	overhead/opposite hand	W/	with		
ENCL	enclosure	OPNG	opening	W/O	without		
EO	electrical outlet	OPP	opposite	WC	water closet		
EP	electrical panel	PART.BD	particle board	WD	wood		
EQ	equal	PART'N	partition	WD	washer/dryer		
EQUIP	equipment	PC	precast concrete	WH	water heater		
EWA/EW	exterior wall assembly	PFM	prefinished metal	WNDW	window		
EWC	electrical water cooler	PL	plate	WP	waterproof		
EWH	electrical water heater	P.LAM	plastic laminate	WR	water resistant		
(E)/EXIST	existing	PLWD	plywood	WRB	weather resistive barrier		
EXH	exhaust	PNL	panel	WT	weight		
EXP	expansion	PR	pair	WWF	welded wire fabric		
EXT	exterior	PSL	parallel strand lumber	WWM	welded wire mesh		
		PT	point	X	by		
		PTD	paper towel dispenser	YD	yard		

REFERENCE SYMBOLS:

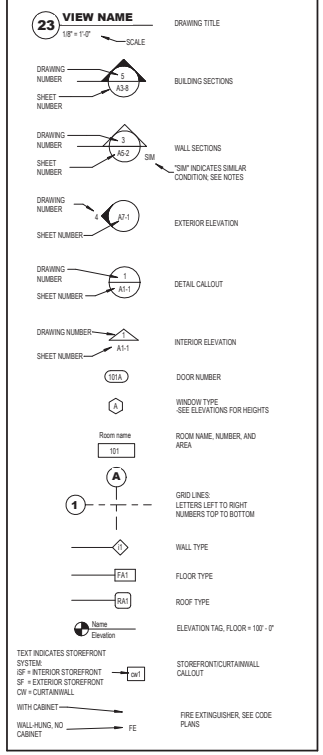

GENERAL CONDITIONS:

1. THE GENERAL CONDITIONS TO THE CONTRACT FOR THE CONSTRUCTION OF BUILDINGS: DOCUMENT A-201, ISSUED BY THE AMERICAN INSTITUTE OF ARCHITECTS HEREINAFTER REFERRED TO AS THE "GENERAL CONDITIONS" RELATES TO THE WORK OF THIS PROJECT AND IS HEREBY MADE A PART OF THE CONTRACT AS THOUGH FULLY CONTAINED IN THESE SPECIFICATIONS.
2. CONTRACT DOCUMENTS INCLUDE THE ARCHITECT'S DRAWINGS, SPECIFICATIONS, GENERAL CONDITIONS, AGREEMENT (BUILDING CONTRACT) AND ALL ADDENDA. THEY ARE TO INCLUDE ALL LABOR, EQUIPMENT, AND MATERIALS NECESSARY FOR THE PROPER EXECUTION OF THE WORK EXCEPT AS MAY BE SPECIFICALLY NOTED OTHERWISE ON THE DRAWINGS OR FOR WHICH SEPARATE PRICES MAY BE ASKED IN THE BID PROPOSAL.
3. REGULATIONS, TAXES AND PERMITS: THE WHOLE OF THE WORK IS TO BE EXECUTED IN STRICT ACCORDANCE WITH THE REGULATIONS AND CODES OF THE GOVERNMENTAL AGENCIES WHOSE JURISDICTION IS APPLICABLE.

GENERAL NOTES:

1. GENERAL CONTRACTOR SHALL FIELD VERIFY ALL EXISTING DIMENSIONS & CONDITIONS. EXISTING DIMENSIONS SHOWN ARE APPROXIMATE AND MUST BE FIELD VERIFIED.
2. REFER TO SPECIFICATIONS FOR DETAILED DESCRIPTIONS & REQUIREMENTS OF CONSTRUCTION.
3. GENERAL CONTRACTOR SHALL COORDINATE THE WORK OF ALL TRADES. PROVIDE ON-SITE SUPERVISION & BE RESPONSIBLE FOR COMPLIANCE WITH ALL SAFETY PRECAUTIONS, CODES AND REGULATIONS.
4. PROTECT EXISTING UTILITIES, SITE IMPROVEMENTS & PLANTING TO REMAIN.
5. PATCH ANY SURFACES DAMAGED DURING CONSTRUCTION. SURFACES ARE TO BE PATCHED FLUSH WITH EXISTING. MATCH EXISTING ADJACENT FINISH OR APPLY NEW FINISH AS SCHEDULED.
6. PROVIDE SOLID BACKING FOR ALL WALL-MOUNTED ITEMS.
7. IN GENERAL, REPETITIVE DETAILS DRAWN ARE SHOWN IN FULL ONLY ONCE. REPETITIONS MAY NOT BE COMPLETE IN EVERY DETAIL AS SHOWN IN THE ORIGINAL DETAIL.
8. DIMENSIONS ARE SHOWN ON THE DRAWINGS. DO NOT SCALE THE DRAWINGS.
9. ALL HEIGHTS ARE DIMENSIONED FROM THE TOP OF SUBFLOOR UNLESS NOTED OTHERWISE.
10. WHERE COLUMNS & STUD WALLS ALIGN, GYPSUM BOARD TO BE CONTINUOUS OVER COLUMNS OR BOXED AROUND COLUMN IF COLUMN PROJECTS BEYOND WALL.
11. BRING TO THE ATTENTION OF THE ARCHITECT ANY CONDITION OR AREA OF FINISH THAT IS IN QUESTION OR NOT NOTED.
12. SEAL ALL PENETRATIONS OF WALLS, FLOORS AND CEILINGS WITH A FIRE RATING EQUIVALENT TO THE CONSTRUCTION PENETRATED AND PER DETAILS & SPECIFICATIONS.
13. DUST BARRIERS MUST BE INSTALLED WHEREVER NEW WORK IS ADJACENT TO OCCUPIED AREAS. BARRIERS MUST BE SEALED TO INSURE NO DUST TRANSMISSION TO OCCUPIED SPACES. COORDINATE LAYOUT, CLEARANCES, PENETRATIONS, BACKING & FASTENERS WITH WORK TO FOLLOW.
14. HEATING, PLUMBING AND ELECTRICAL PLANS WHERE SHOWN DIAGRAMMATICALLY ARE INTENDED TO INDICATE CAPACITY, SIZE, LOCATION & GENERAL ARRANGEMENTS. ALL NECESSARY FEATURES OF RELATED CONSTRUCTION WILL BE REQUIRED AS IF SHOWN IN DETAIL.
15. WHERE MECHANICAL & ELECTRICAL EQUIPMENT LOCATIONS CONFLICT ELECTRICAL, LIGHT FIXTURE LOCATIONS SHALL TAKE PRECEDENCE.
16. PROVIDE SUFFICIENT STUD DEPTH TO CONCEAL MECHANICAL & ELECTRICAL WORK IN WALLS.
17. PROVIDE ALL NEW MATERIALS (U.N.O.) AND QUALIFIED CRAFT PERSONS TO COMPLETE THE WORK.
18. CONSTRUCTION DOCUMENTS SHOW THE DESIGN INTENT OF THE PROJECT AND MAY NOT SHOW MINOR DETAILS OF PROPOSED INSTALLATIONS. THE INCLUSION OF THESE MINOR DETAILS IS IMPLIED TO PROVIDE A COMPLETE PROJECT AND ARE TO BE INCLUDED AS A PART OF A BID.
19. REFER TO MECHANICAL & ELECTRICAL DRAWINGS FOR COORDINATION OF WORK.
20. IN THE CASE OF CONTRADICTIONS BETWEEN DRAWINGS OR BETWEEN DRAWINGS & SPECIFICATIONS, ASSUME THE MORE COSTLY APPROACH FOR BIDDING PURPOSES. BRING ALL CONTRADICTIONS TO THE ATTENTION OF THE ARCHITECT.
21. CONTRACTOR SHALL PROMPTLY REMOVE ALL WASTE MATERIALS AND LEAVE PREMISES AND SITE CLEAN.
22. THE CONTRACTOR SHALL PROVIDE ALL CEILING AND/OR WALL ACCESS PANELS/DOORS AS REQUIRED BY THE AIR CONDITIONING, PLUMBING & ELECTRICAL SYSTEMS. PROVIDE APPROVED ASSEMBLIES W/ SELF-CLOSING DEVICES IN RATED CONSTRUCTION. (PAINT TO MATCH ADJACENT WALL COLOR)
23. ELECTRICAL OUTLETS AND LIGHTING ARE ONLY SHOWN ON ARCHITECTURAL "A" SHEETS WHERE PLACEMENT OF SUCH IS CRITICAL TO PARTICULAR AESTHETICS. SEE ELECTRICAL DRAWINGS FOR ALL ELECTRICAL AND DATA FEATURES.

DRAWING SET NOTE: THESE DRAWINGS ARE TO BE UTILIZED AS A COMPLETE SET FOR BIDDING & CONSTRUCTION. INDIVIDUAL SECTIONS OF DRAWINGS SHOULD NOT BE SEPARATED FROM THE ENTIRE SET. IMPORTANT NOTES FOR ONE AREA OF WORK MAY BE INCLUDED IN OTHER AREAS IN THE DRAWINGS. ALL CONTRACTORS & SUPPLIERS MUST REVIEW ENTIRE DRAWING SET & SPECIFICATIONS.

GENERAL WALL NOTES

1. WALL TYPE CONSTRUCTION IS CONTINUOUS FROM SLAB TO ROOF FRAMING ABOVE UNLESS INDICATED OTHERWISE.
2. IF A WALL TYPE IS NOT INDICATED, PROVIDE WALL TYPE OF MOST SIMILAR CONDITION - VERIFY WITH ARCHITECT.
3. IN CASES OF CONFLICT BETWEEN SECTIONS AND WALL TYPES, CLARIFY WITH ARCHITECT PRIOR TO BIDDING WHEN TIME ALLOWS, OTHERWISE ASSUME THE MOST EXPENSIVE CONDITION FOR BIDDING PURPOSES.
4. STRUCTURAL NOTES, SPECIFICATIONS, STUD GAUGE NOTATIONS ETC. TAKE PRECEDENCE OVER ARCHITECTURAL WALL TYPES.
5. FOR LIGHT GAUGE (NON-STRUCTURAL) METAL FRAMING, PROVIDE MIN. 22 GAUGE STUDS UNLESS THE CONTRACTOR CAN PROVIDE MANUFACTURER'S DATA SUPPORTING LIGHTER GAUGE STUDS BASED ON HEIGHT AND FINISH MATERIALS.
6. ALL VOIDS IN EXTERIOR WALLS - INCLUDING IN NON-VISIBLE LOCATIONS - TO BE FILLED TIGHT WITH INSULATION. SMALL CRACKS & VOIDS TO BE CAULKED OR SPRAY-FOAMED FOR TIGHT SEAL.
7. ALL EXTERIOR WALLS TO RECEIVE VAPOR BARRIER UNDER INTERIOR FINISH. ALL SEAMS OF VAPOR BARRIER MUST BE TAPED/SEALED TIGHT AND ALL JOINTS MUST BE TAPED/ SEALED TIGHT WITH MATERIALS AND METHODS APPROVED BY VAPOR BARRIER MFR.
8. TYPE "X" GYPSUM WALL BOARD SPECIFIED THROUGHOUT. PROVIDE WATER-RESISTANT TYPE "X" GYPSUM BOARD ON ENTIRE WALL WHERE PLUMBING FIXTURES OCCUR. PROVIDE TILE BACKER BOARD TYPE "X" ON ALL WALLS WITH TILE.
9. WALLS INDICATED WITH ACOUSTICAL INSULATION TO MEET AN STC RATING OF 48 OR MORE, UNLESS OTHERWISE INDICATED.
10. PROVIDE SOUND ATTENUATION INSULATION ON TOP OF ACT WHERE WALLS TERMINATE AT CEILING OR 6" ABOVE CEILING. EXTEND 5 FEET TO BOTH SIDES OF WALL. HOLD INSULATION 7" AWAY FROM LIGHT FIXTURES.
11. PROVIDE BACKER ROD & CAULKING JOINT AT ABUTMENT OF ALL DISSIMILAR MATERIALS.
12. PROVIDE STEEL "J" EDGE METAL AND 1/4" CAULK JOINT AT PERIMETER OF ALL GYPSUM BOARD WALLS WHERE ABUTTING DIFFERENT MATERIALS.
13. PROVIDE CORNER BEADS AT ALL EXTERNAL GYPSUM BOARD CORNERS.
14. PENETRATIONS OF FIRE-RESISTIVE WALLS, HORIZONTAL ASSEMBLIES SHALL BE PROTECTED AS REQUIRED IN IBC SECTION 714.
15. PROVIDE FIRE, SMOKE AND CEILING RADIATION DAMPERS AT DUCT PENETRATIONS AND AIR TRANSFER OPENINGS IN FIRE RATED ASSEMBLES PER IBC SECTION 717.

APPLICABLE BUILDING CODES

THIS PROJECT SHALL COMPLY WITH THE LATEST EDITION OF CODES ADOPTED BY THE USDA FOREST SERVICE:

2021 International Residential Code (IBC)
2021 International Mechanical Code (IMC)
2021 International Fuel Gas Code (IFGC)
2021 International Plumbing Code (IPC)
2020 National Electrical Code (NEC)
2021 International Fire Code (IFC)
2021 International Energy Conservation Code (IECC)
2021 International Existing Building Code (IEBC)

WALL TYPE TAG




WALL STUD & FINISH HEIGHT

c GWB TO 6" ABOVE CEILING; FRAME OR BRACE TO STRUCTURE
e EXTERIOR - SEE SECTIONS
f FURRING
p PARTIAL HEIGHT
s TO STRUCTURE
x SHAFT - CONTINUOUS THROUGH FLOOR ASSEMBLIES


INTERIOR WALL TYPES

NOTE: SEE ELEVATIONS AND FINISH SCHEDULES FOR WALL FINISHES, TYPICAL ALL WALL TYPES

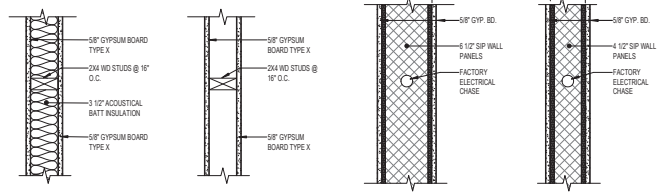


I1 INTERIOR PARTITION — NON-RATED SOUND WALL
I2 INTERIOR PARTITION — NON-RATED SOUND WALL
I3 INTERIOR PARTITION — NON-RATED
I4 INTERIOR PARTITION — NON-RATED

EXTERIOR WALL TYPE

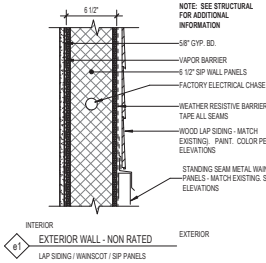

ROOF/CEILING ASSEMBLY

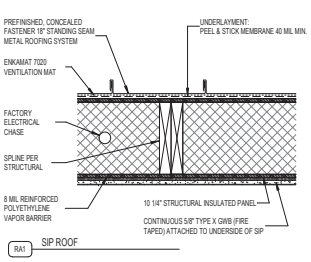

BID ALTERNATES

ADDITIVE ALTERNATE NO. 1

BASE BID: REPLACE SIP PANELS AS SHOWN ON DRAWINGS.
ALTERNATE: 1. PROVIDE COST PER SQUARE FOOT FOR ADDITIONAL DAMAGED SIP PANEL REPLACEMENTS, INCLUDING SPLINES, FASTENERS, SEALANTS, AND OTHER COMPONENTS TO PROVIDE COMPLETE SYSTEM.
2. PROVIDE COST PER LINEAR FOOT FOR REPLACEMENT OF DAMAGED 5 1/8"X12" GLU-LAM ROOF BEAMS.

ADDITIVE ALTERNATE NO. 2

BASE BID: PAINT ROOMS PER FINISH SHEDULE
ALTERNATE: PAINT ALL ROOMS (WALLS & CEILINGS, P1) EXCEPT GARAGES AND STORAGE 209

mosaic
architecture-planning-design
317 Cruse Avenue Suite 201
Helena, Montana 59601
406.449.2013
www.mosaicarch.com

LICENSED ARCHITECT AR-986501
JEFFERY R. DOWNHOUR
STATE OF IDAHO

U.S. DEPARTMENT OF AGRICULTURE
FOREST SERVICE
R-1 NORTHERN REGION

POWELL DUPLEX RENOVATION

LOCHSA-POWELL RANGER DISTRICT
192 POWELL RD, LOLO, MT 59847
NEZ PERCE-CLEARWATER NATIONAL FORESTS

CONSTRUCTION DOCUMENTS


MARK	DATE	REVISION

PROJECT NO. 1240LU23F0138
DATE: 7/19/2024
Drawn By: Mosaic
Designed By: Mosaic
Checked By: Mosaic


GENERAL INFORMATION & ASSEMBLY TYPES

SHEET: **A001**

DATESTAMP - 7/19/2024 10:15:59 AM

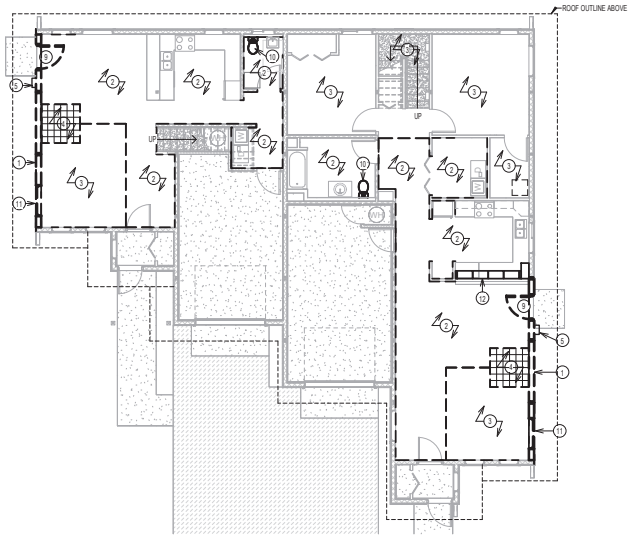

1 **LEVEL 1 DEMOLITION PLAN**
1/8" = 1'-0"

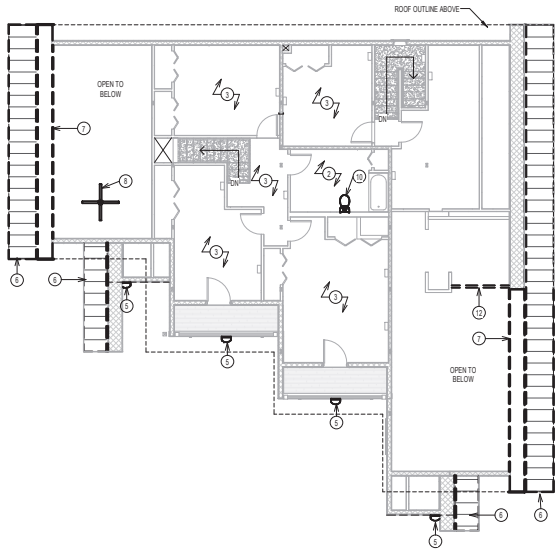

2 **LEVEL 2 DEMOLITION PLAN**
1/8" = 1'-0"

DEMOLITION KEYNOTES

NOTE: SEE MECH/ELEC/STRUCT AND CIVIL DRAWINGS FOR ADDITIONAL DEMOLITION INFORMATION.


1. REMOVE ALL EXISTING SIP WALL PANELS AND STUD PACKS/COLUMNS EXHIBITING DAMAGE OR DEGRADATION DUE TO WATER INFILTRATION. AREAS INDICATED AS DEMOLISHED TO BE INCLUDED IN BASE BID. ADDITIONAL DAMAGED PANELS & STRUCTURE DISCOVERED WHICH REQUIRE DEMOLITION & REPLACEMENT TO BE ADDRESSED THROUGH UNIT PRICING PROVISIONS OF ADDITIVE ALTERNATE 1. RETAIN EXISTING UNDAMAGED WINDOWS & DOORS FOR RE-INSTALLATION IN NEW SIP PANELS AS NOTED. REPAIR ALL ADJACENT SURFACES TO RECEIVE NEW FINISHES.
2. REMOVE EXISTING SHEET VINYL FLOORING AND PREPARE SUBFLOOR FOR INSTALLATION OF NEW FLOORING
3. REMOVE EXISTING CARPETING AND PREPARE SUBFLOOR FOR INSTALLATION OF NEW FLOORING
4. REMOVE EXISTING TILE FLOOR PROTECTOR AND PREPARE SUBFLOOR FOR INSTALLATION OF NEW FLOORING.
5. REMOVE LIGHT FIXTURE - SEE MEP.
6. REMOVE ENTIRE EXISTING STANDING SEAM ROOF AND UNDERLAYMENT.
7. REMOVE ALL EXISTING SIP ROOF PANELS, SPLINES, AND SUPPORT BEAMS EXHIBITING DAMAGE OR DEGRADATION DUE TO WATER INFILTRATION. SHADED AREAS INDICATE PANELS INDICATED TO BE DEMOLISHED WHICH ARE TO BE INCLUDED IN BASE BID. ADDITIONAL DAMAGED PANELS & STRUCTURAL ELEMENTS DISCOVERED WHICH REQUIRE DEMOLITION & REPLACEMENT TO BE ADDRESSED THROUGH UNIT PRICING PROVISIONS OF ADDITIVE ALTERNATE 1. REPAIR ALL ADJACENT SURFACES TO RECEIVE NEW FINISHES. FASCIAS AND SOFFITS ATTACHED TO PANELS BEING DEMOLISHED ARE TO BE REPLACED AS WELL.
8. REMOVE EXISTING CEILING FAN
9. REMOVE EXISTING DOOR & SCREEN DOOR.
10. REMOVE EXISTING PLUMBING FIXTURE - SEE PLUMBING DRAWINGS.
11. REMOVE EXISTING WINDOW AND RETAIN FOR RE-USE IN NEW SIP PANEL.
12. REMOVE EXISTING BEAM AND UPPER CABINETS, OR SUPPORT IN PLACE, AS REQUIRED FOR REPLACEMENT OF EXISTING COLUMN BETWEEN SIP PANELS. ATTACH BEAM TO NEW COLUMN, REINSTALLING CABINETS IF REMOVED.
13. CUT OPENING IN ROOF AS REQUIRED FOR STOVE PIPE. CEILING SUPPORT BOX; BLOCK ALL SIDES OF OPENING W/ 2X PLATING & SIP SEALANT

GENERAL DEMOLITION NOTES


1. VERIFY ALL CONDITIONS AND COORDINATE WITH ALL DISCIPLINES OF CONTRACT. UNDOCUMENTED FIELD CHANGES MAY HAVE OCCURRED AND ARE TO BE BROUGHT TO THE ATTENTION OF THE ARCHITECT WHEN DISCOVERED.
2. SEE CIVIL DRAWINGS FOR SITE DEMOLITION.
3. SEE MECHANICAL, ELECTRICAL AND PLUMBING DRAWINGS FOR DEMOLITION WORK OF THOSE TRADES.
4. WHERE DEMOLITION IS INDICATED, WALLS SHALL BE REMOVED AND CEILING SHALL BE PATCHED, REPAIRED AND PAINTED TO MATCH EXISTING.
5. CONTRACTOR SHALL MAINTAIN A TEMPORARY WEATHER TIGHT ENCLOSURE AS ITEMS ARE BEING REMOVED.
6. COORDINATE ALL MECHANICAL, ELECTRICAL, FIRE SYSTEMS, COMMUNICATIONS AND UTILITY SHUT-DOWNS WITH OWNER PRIOR TO REMOVING AND OR RELOCATING.
7. DEMOLITION IS NOT NECESSARILY LIMITED TO WHAT IS SHOWN ON DRAWINGS. THE INTENT IS TO INDICATE THE GENERAL SCOPE OF DEMOLITION REQUIRED TO COMPLETE THE WORK IN ACCORDANCE WITH THE CONTRACT DRAWINGS.
8. THESE DRAWINGS INDICATE STRUCTURAL AND NON-STRUCTURAL DEMOLITION THAT IS TO OCCUR TO MAKE WAY FOR NEW CONSTRUCTION. ADDITIONAL STRUCTURAL DEMOLITION WORK, CONSTRUCTION OR SHORING REQUIRING COORDINATION WITH NEW STRUCTURAL IS INDICATED ON THE STRUCTURAL DRAWINGS.
9. EXISTING OPENINGS IN WHICH MECHANICAL AND PLUMBING ARE REMOVED IN A CONCRETE SLAB SHALL BE FILLED WITH AN EPOXY-BASED TWO-COMPONENT CEMENTITIOUS TROWEL-GRADE MORTAR. OPENINGS SHALL BE FORMED AND MATERIAL PLACED IN OPENINGS OF 12"x12" SQ/DIA OR LARGER, CONTRACTOR SHALL PROVIDE #4 DOWELS AT 8" O.C. EACH WAY IN OPENINGS. CONTRACTOR SHALL EPOXY MORTAR/CHEM. AND ADHESIVE SET DOWELS INTO EXISTING CONCRETE WITH 4" MIN. EMBED.
10. SEE HAZARDOUS MATERIALS ABATEMENT DRAWINGS FOR ADDITIONAL INFORMATION AND COORDINATION.

LINEWORK LEGEND


- DEMOLISHED ELEMENTS
- EXISTING ELEMENTS TO REMAIN

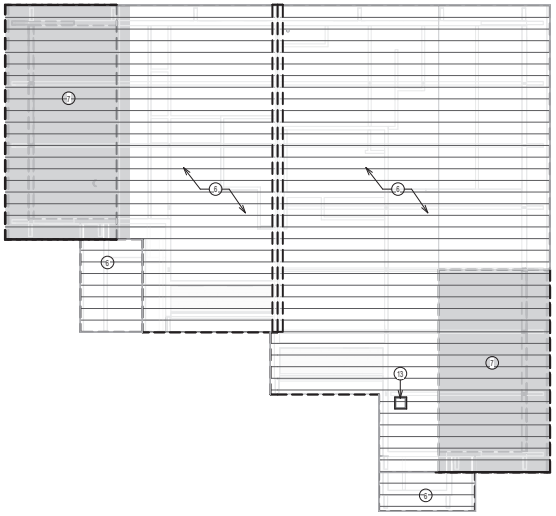

3 **ROOF DEMOLITION PLAN**
1/8" = 1'-0"

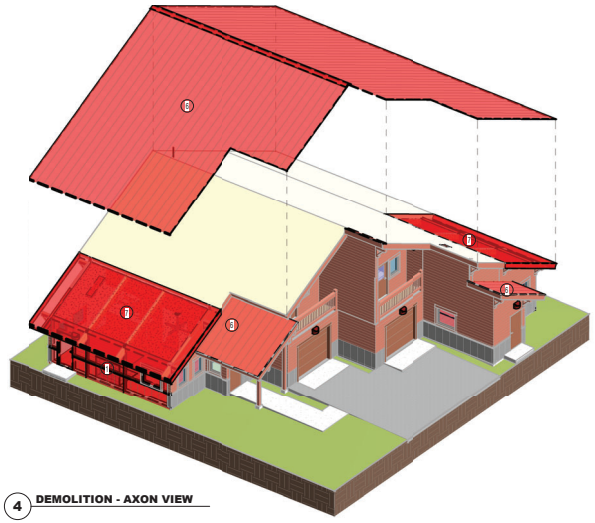

4 **DEMOLITION - AXON VIEW**

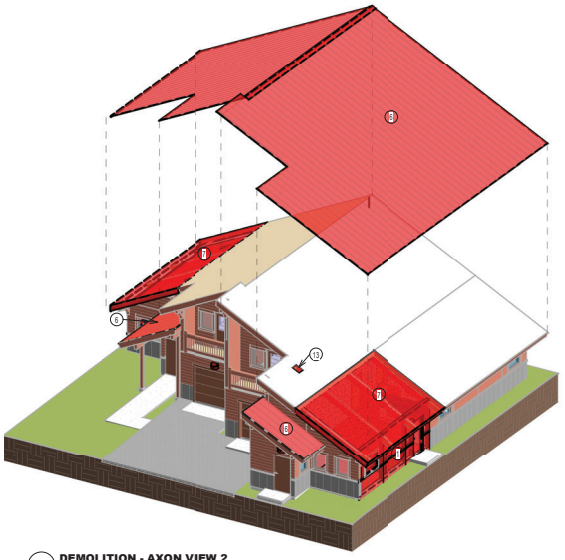

5 **DEMOLITION - AXON VIEW 2**

mosaic
architecture-planning-design
317 Cruse Avenue Suite 201
Helena, Montana 59601
406.449.2013
www.mosaicarch.com

LICENSED ARCHITECT
AR-986501
JEFFERY R. DOWNHOUR
STATE OF IDAHO

U.S. DEPARTMENT OF AGRICULTURE
FOREST SERVICE
R-1 NORTHERN REGION

POWELL DUPLEX RENOVATION

LOCHSA-POWELL RANGER DISTRICT
192 POWELL RD, LOLO, MT 59847
NEZ PERCE-CLEARWATER NATIONAL FORESTS

CONSTRUCTION DOCUMENTS


MARK	DATE	REVISION

PROJECT NO. 1240LU23F0138
DATE: 7/19/2024
Drawn By: Mosaic
Designed By: Mosaic
Checked By: Mosaic

DEMOLITION PLANS

SHEET: A100

DATE STAMP - 7/19/2024 10:19:43 AM

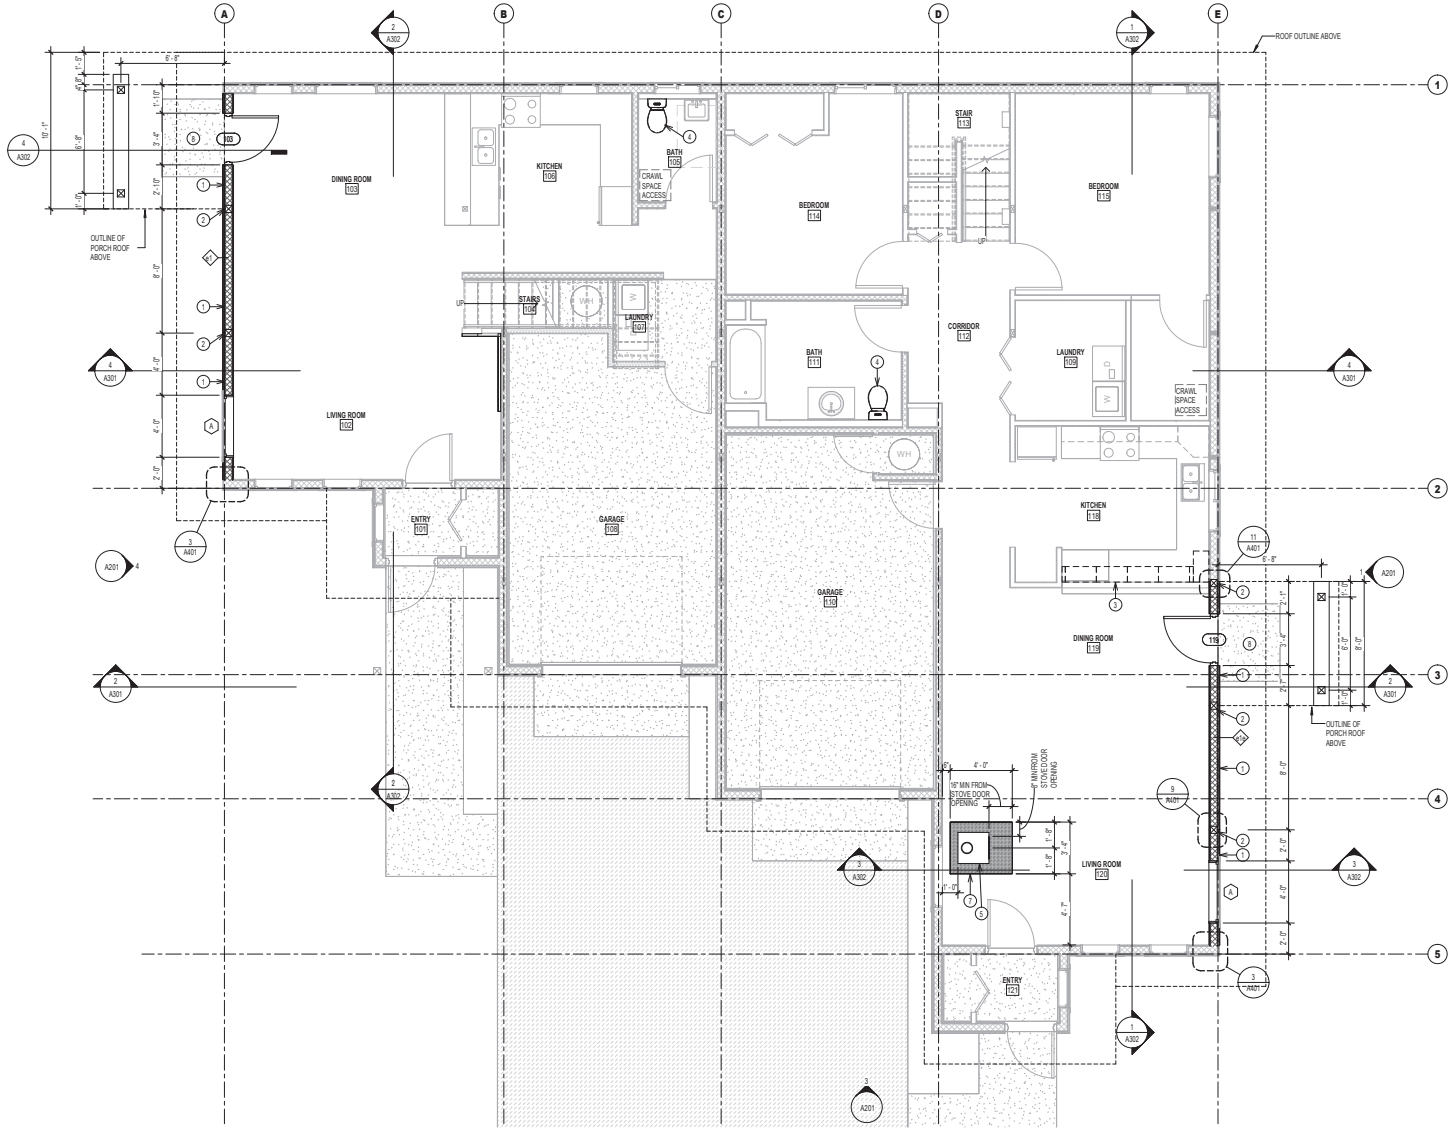

1 **LEVEL 1 FLOOR PLAN**
1/4" = 1'-0"

GENERAL FLOOR PLAN NOTES

1. DIMENSIONS ARE TO FACE OF STUD, EXISTING WALL FINISH, MASONRY, OR DOOR/WINDOW OPENINGS. DIMENSIONS OF EXISTING CONSTRUCTION ARE NOT SHOWN ON DRAWINGS - VERIFY DIMENSIONS OF ALL EXISTING CONSTRUCTION IN THE FIELD. DIMENSIONS TO OPENINGS ARE NOMINAL. VERIFY ALL OPENINGS WITH ROUGH OPENING REQUIREMENTS.
2. ALL DOOR OPENINGS PERPENDICULAR TO A WALL ARE 4" TO THE WALL FRAMING U.N.O.
3. EXISTING CONSTRUCTION TO REMAIN SHOWN SHADED, NEW CONSTRUCTION SHOWN SOLID.
4. SEE SHEET A-002 FOR WALL TYPES. IN AREAS WITH SUSPENDED ACOUSTICAL TILE CEILINGS, GYPSUM WALL BOARD MAY BE TERMINATED 6" ABOVE THE CEILING. IN AREAS WITH EXPOSED STRUCTURE CONTINUE GYPSUM BOARD TO UNDERSIDE OF STRUCTURE.
5. VERIFY EXISTING WALL CONSTRUCTION.
6. ALL EGRESS DOORS SHALL BE READILY OPERABLE FROM THE EGRESS SIDE WITHOUT THE USE OF A KEY OR SPECIAL KNOWLEDGE OR EFFORT.

LINEWORK LEGEND

- NEW CONSTRUCTION
- EXISTING ELEMENTS TO REMAIN

PLAN KEYNOTES

NOTE: SEE MECH/ELEC/STRUCT AND CIVIL DRAWINGS FOR ADDITIONAL INFORMATION.

1. NEW SIP WALL PANEL PER STRUCTURAL
2. NEW 6X6 POST EMBEDDED IN SIP WALL CONT TO ROOF BEAM - SEE STRUCT
3. RE-MOUNT EXISTING BEAM AND UPPER CABINETS IF REMOVED TO ALLOW REPLACEMENT OF COLUMN AT SIP WALL. ATTACH BEAM TO NEW COLUMN
4. NEW TOILET - SEE PLUMBING
5. WOOD STOVE - SEE SPECIFICATIONS.
6. NEW SIP ROOF PANEL PER STRUCTURAL.
7. STOVE BOARD PROVIDING EMBER & THERMAL FLOOR PROTECTION - SEE SPECIFICATIONS.
8. EXISTING CONCRETE PORCH TO REMAIN.

mosaic
architecture-planning-design
317 Cruse Avenue Suite 201
Helena, Montana 59601
406.449.2013
www.mosaicarch.com

LICENSED ARCHITECT
AR-986501
JEFFERY R. DOWNHOUR
STATE OF IDAHO

U.S. DEPARTMENT OF AGRICULTURE
FOREST SERVICE
R-1 NORTHERN REGION

POWELL DUPLEX RENOVATION

LOCHSA-POWELL RANGER DISTRICT
192 POWELL RD, LOLO, MT 59847
NEZ PERCE-CLEARWATER NATIONAL FORESTS

CONSTRUCTION DOCUMENTS


MARK	DATE	REVISION

PROJECT NO. 1240LU23F0138
DATE: 7/19/2024
Drawn By: Mosaic
Designed By: Mosaic
Checked By: Mosaic

LEVEL 1 FLOOR PLAN

SHEET: **A101**

DATE STAMP: 7/19/2024 10:19:44 AM

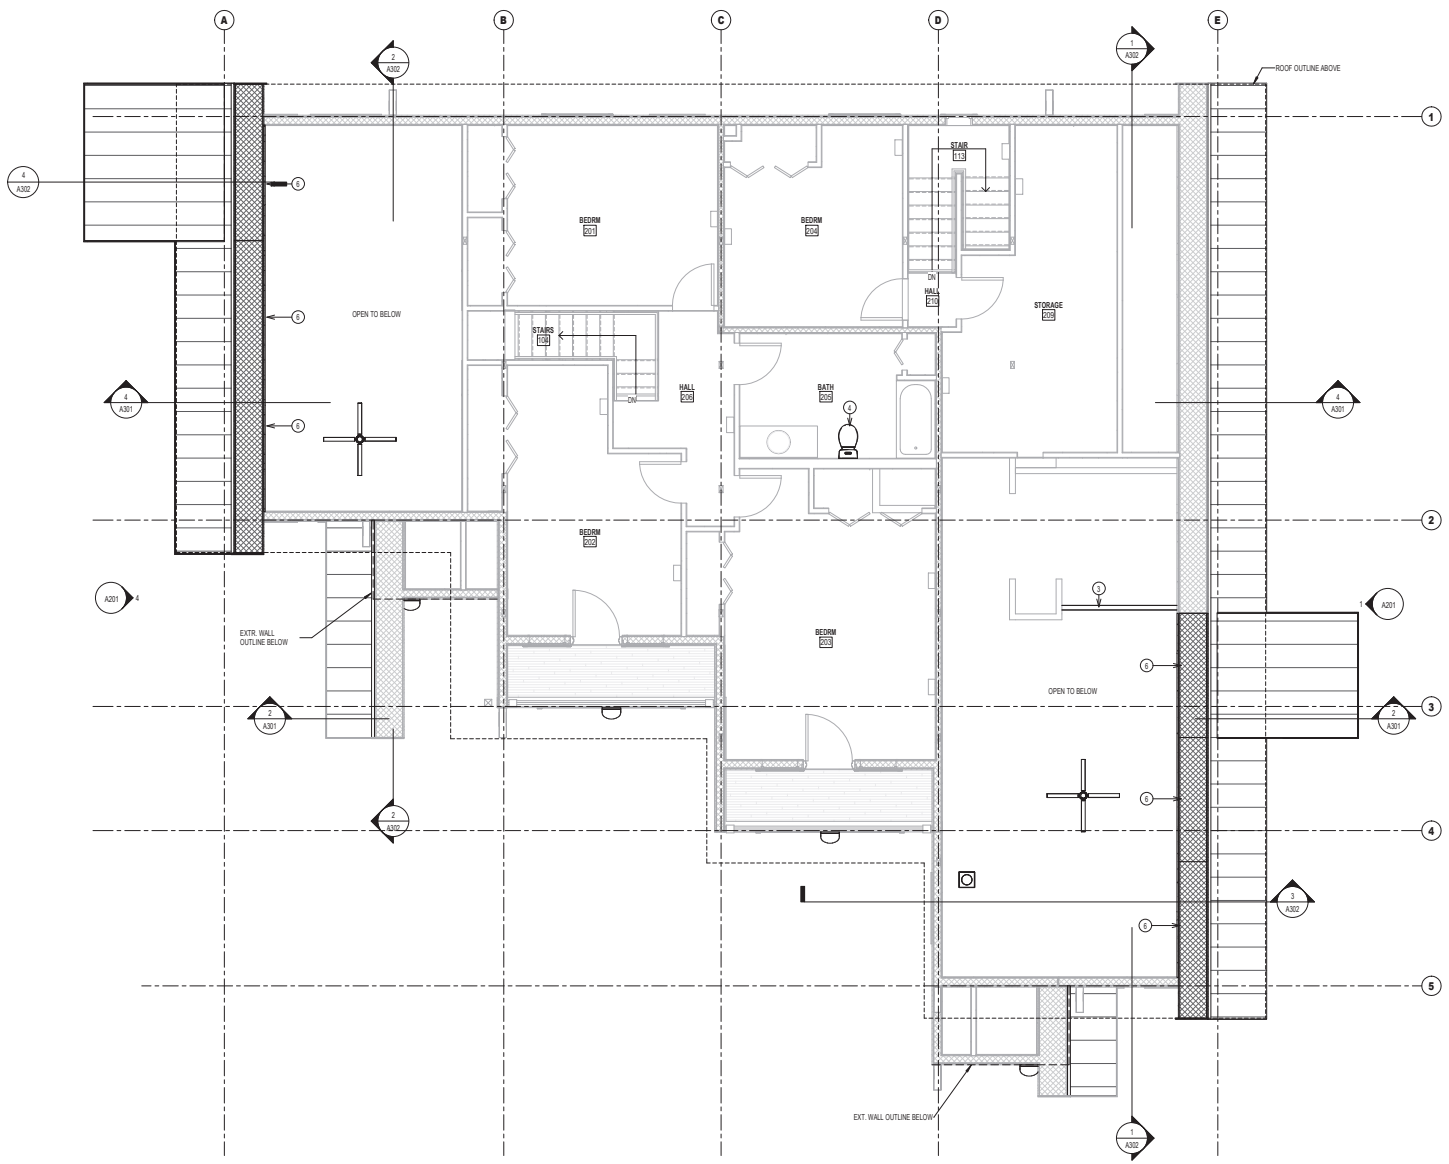

1 **LEVEL 2 FLOOR PLAN**
1/4" = 1'-0"

GENERAL FLOOR PLAN NOTES

1. DIMENSIONS ARE TO FACE OF STUD, EXISTING WALL FINISH, MASONRY, OR DOOR/WINDOW OPENINGS. DIMENSIONS OF EXISTING CONSTRUCTION ARE NOT SHOWN ON DRAWINGS - VERIFY DIMENSIONS OF ALL EXISTING CONSTRUCTION IN THE FIELD. DIMENSIONS TO OPENINGS ARE NOMINAL. VERIFY ALL OPENINGS WITH ROUGH OPENING REQUIREMENTS.
2. ALL DOOR OPENINGS PERPENDICULAR TO A WALL ARE 4" TO THE WALL FRAMING UNO.
3. EXISTING CONSTRUCTION TO REMAIN SHOWN SHADED, NEW CONSTRUCTION SHOWN SOLID.
4. SEE SHEET A-002 FOR WALL TYPES. IN AREAS WITH SUSPENDED ACOUSTICAL TILE CEILINGS, GYPSUM WALL BOARD MAY BE TERMINATED 8" ABOVE THE CEILING. IN AREAS WITH EXPOSED STRUCTURE CONTINUE GYPSUM BOARD TO UNDERSIDE OF STRUCTURE.
5. VERIFY EXISTING WALL CONSTRUCTION.
6. ALL EGRESS DOORS SHALL BE READILY OPERABLE FROM THE EGRESS SIDE WITHOUT THE USE OF A KEY OR SPECIAL KNOWLEDGE OR EFFORT.

LINEWORK LEGEND

NEW CONSTRUCTION

EXISTING ELEMENTS TO REMAIN

PLAN KEYNOTES

NOTE: SEE MECH/ELEC/STRUCT AND CIVIL DRAWINGS FOR ADDITIONAL INFORMATION.

1. NEW SIP WALL PANEL PER STRUCTURAL
2. NEW 6X6 POST EMBEDDED IN SIP WALL CONT TO ROOF BEAM - SEE STRUCT
3. RE-MOUNT EXISTING BEAM AND UPPER CABINETS IF REMOVED TO ALLOW REPLACEMENT OF COLUMN AT SIP WALL. ATTACH BEAM TO NEW COLUMN
4. NEW TOILET - SEE PLUMBING
5. WOOD STOVE - SEE SPECIFICATIONS,
6. NEW SIP ROOF PANEL PER STRUCTURAL.
7. STOVE BOARD PROVIDING EMBER & THERMAL FLOOR PROTECTION - SEE SPECIFICATIONS.
8. EXISTING CONCRETE PORCH TO REMAIN.

mosaic
architecture-planning-design
317 Cruse Avenue Suite 201
Helena, Montana 59601
406.449.2013
www.mosaicarch.com

LICENSED ARCHITECT
AR-986501
JEFFERY R. DOWNHOUR
STATE OF IDAHO

U.S. DEPARTMENT OF AGRICULTURE
FOREST SERVICE
R-1 NORTHERN REGION

POWELL DUPLEX RENOVATION

LOCHSA-POWELL RANGER DISTRICT
192 POWELL RD, LOLO, MT 59847
NEZ PERCE-CLEARWATER NATIONAL FORESTS

CONSTRUCTION DOCUMENTS


MARK	DATE	REVISION

PROJECT NO. 1240LU23F0138
DATE: 7/19/2024
Drawn By: Mosaic
Designed By: Mosaic
Checked By: Mosaic


LEVEL 2 FLOOR PLAN

SHEET: **A102**


DATE STAMP - 7/19/2024 10:19:45 AM

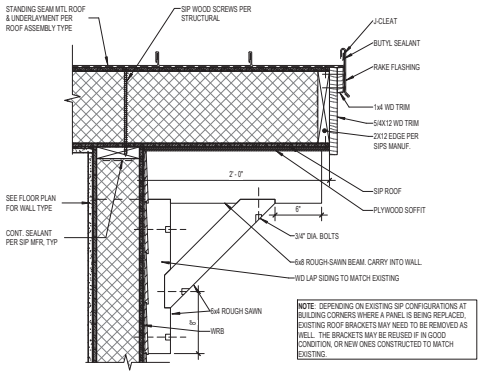


2 SIP ROOF AT RAKE
1 1/2" = 1'-0"

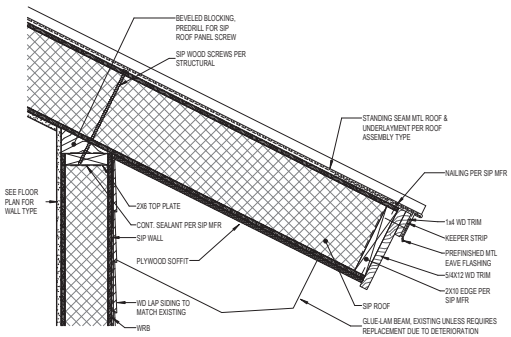

3 SIP ROOF AT LOW EAVE
1 1/2" = 1'-0"

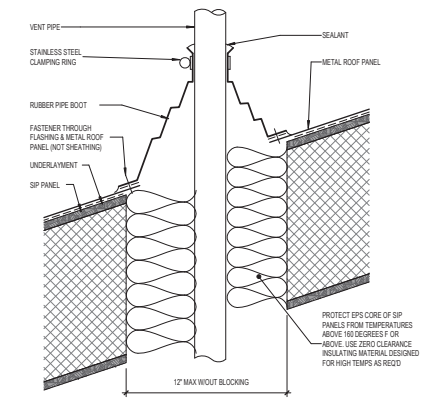

4 PIPE PENETRATION AT ROOF
3" = 1'-0"

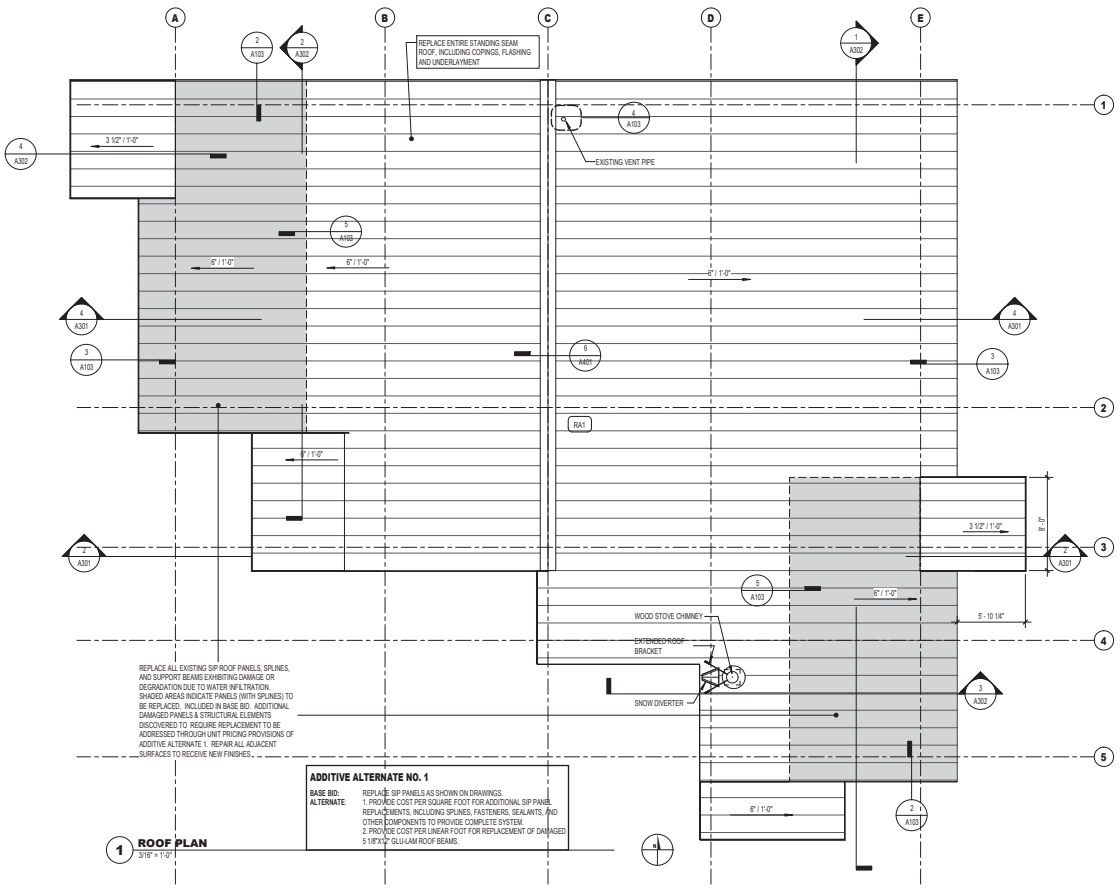


ADDITIVE ALTERNATE NO. 1


BASE BID: REPLACE SIP PANELS AS SHOWN ON DRAWINGS.

ALTERNATE:
1. PROVIDE COST PER SQUARE FOOT FOR ADDITIONAL SIP PANEL REPLACEMENTS, INCLUDING SPLINES, FASTENERS, SEALANTS, AND OTHER COMPONENTS TO PROVIDE COMPLETE SYSTEM.
2. PROVIDE COST PER LINEAR FOOT FOR REPLACEMENT OF DAMAGED 5 1/8"X12" GLU-LAM ROOF BEAMS.


1 ROOF PLAN
3/16" = 1'-0"

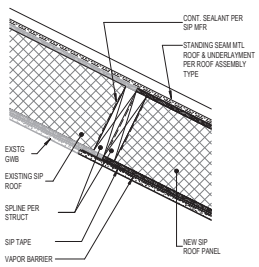

5 SIP ROOF SPLINE - LONGITUDINAL
1 1/2" = 1'-0"

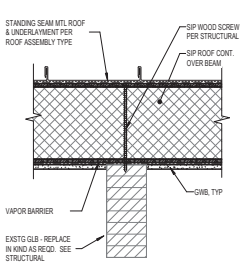

6 SIP ROOF AT BEAM
1 1/2" = 1'-0"

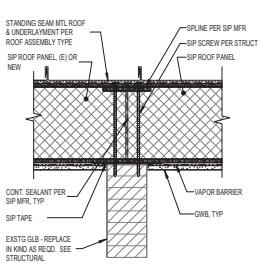

7 SIP ROOF SPLINE AT BEAM
1 1/2" = 1'-0"

GENERAL ROOFING NOTES

1. INSTALL SELF-ADHERING ICE BARRIER MATERIAL ON ALL EAVES AND OVERHANGS FROM THE LOWEST EDGE OF ALL ROOF SURFACES TO A POINT AT LEAST 36" INSIDE THE EXTERIOR WALL LINE OF THE BUILDING.
2. INSTALL SELF-ADHERING ICE BARRIER MATERIAL AT ALL VALLEYS & CHANGES IN ROOF SLOPE, 24" MIN. EACH SIDE OF TRANSITION.
3. PROVIDE TAPERED INSULATION CRICKET ON UPHILL SIDE OF ALL ROOF CURBS/PENETRATIONS GREATER THAN 1'-0" WIDE.
4. GANG PLUMBING VENTS ABOVE CEILING TO MINIMIZE ROOF PENETRATIONS. VERIFY PENETRATIONS IN FIELD. LOCATE PENETRATIONS TO NOT BE VISIBLE FROM APPROACH TO FRONT ENTRY WHERE FEASIBLE.
5. SEE MECHANICAL AND PLUMBING DRAWINGS FOR PIPING AND EQUIPMENT PENETRATIONS. ALL PVC PIPE PENETRATIONS TO BE PAINTED DARK GREY.

LINEWORK LEGEND

NEW CONSTRUCTION

EXISTING ELEMENTS TO REMAIN

mosaic
architecture-planning-design
317 Cruse Avenue Suite 201
Helena, Montana 59601
406.449.2013
www.mosaicarch.com

LICENSED ARCHITECT
AR-986501
JEFFERY R. DOWNHOUR
STATE OF IDAHO

U.S. DEPARTMENT OF AGRICULTURE
FOREST SERVICE
R-1 NORTHERN REGION

POWELL DUPLEX RENOVATION

LOCHSA-POWELL RANGER DISTRICT
192 POWELL RD, LOLO, MT 59847
NEZ PERCE-CLEARWATER NATIONAL FORESTS

CONSTRUCTION DOCUMENTS


MARK	DATE	REVISION

PROJECT NO. 1240LU23F0138
DATE: 7/19/2024
Drawn By: Mosaic
Designed By: Mosaic
Checked By: Mosaic


ROOF PLAN

SHEET: **A103**

DATESTAMP - 7/19/2024 10:19:43 AM

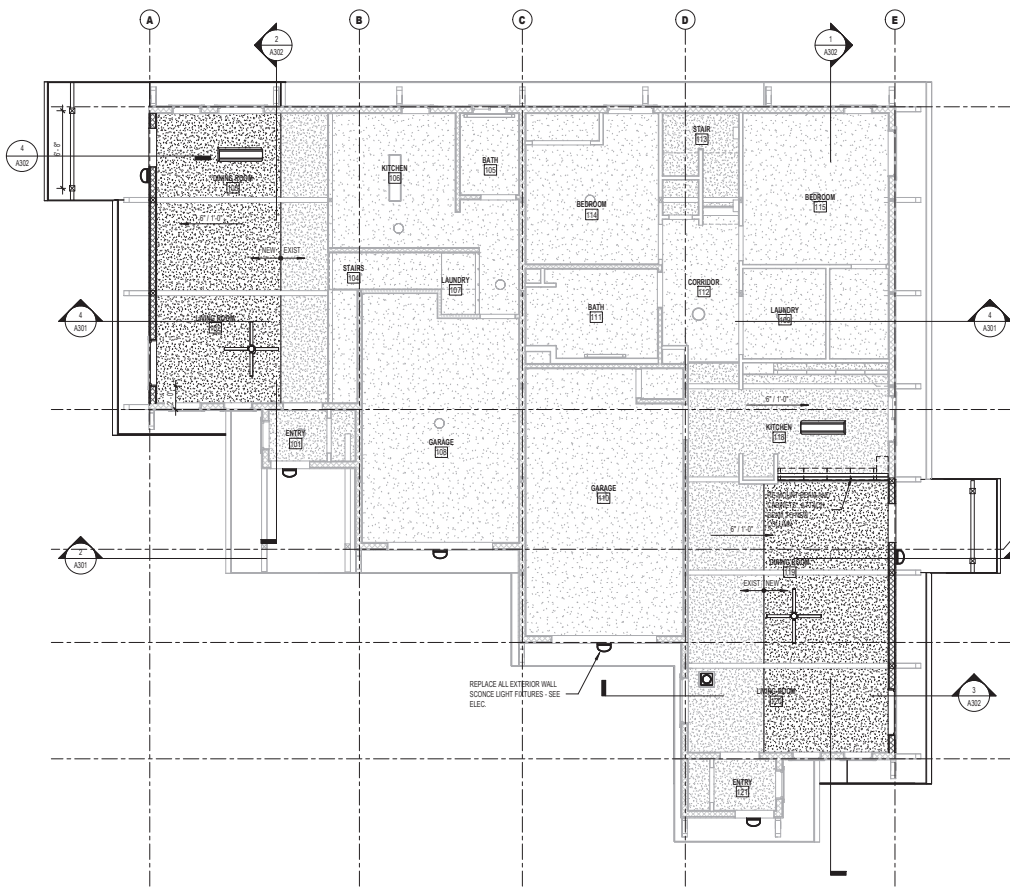

1 **LEVEL 1 RCP**
3/16" = 1'-0"

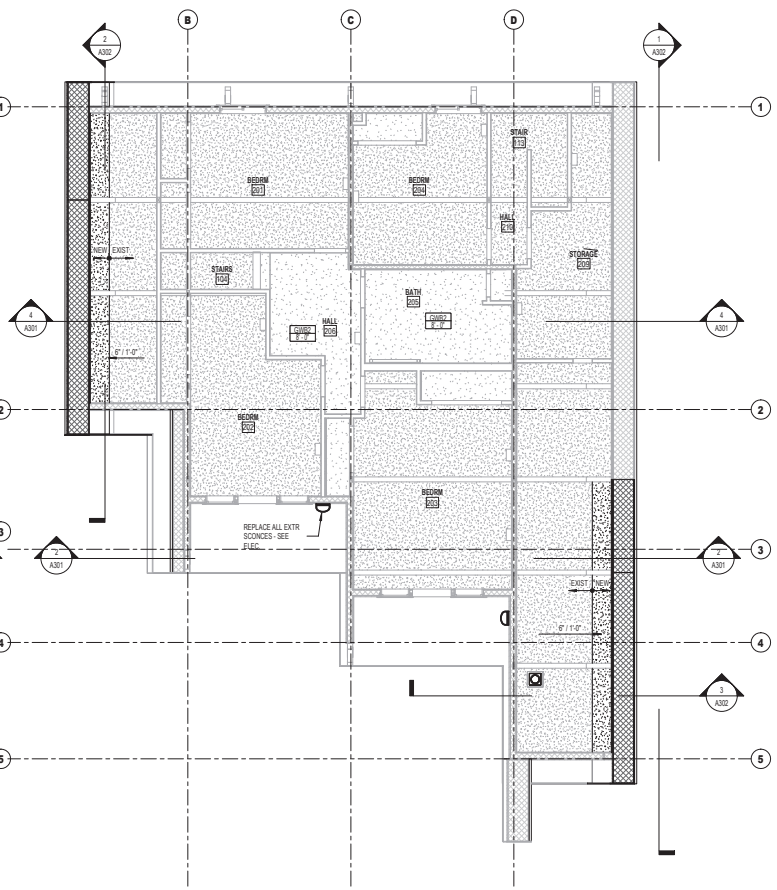

2 **LEVEL 2 RCP**
3/16" = 1'-0"

CEILING LEGEND

GWB1	SLOPED CEILING - 1/2" TYPE "X" GYPSUM WALLBOARD ON SIP PANEL
GWB2	FLAT CEILING - 1/2" TYPE "X" GYPSUM WALLBOARD ON WOOD FRAMING
	OPEN TO STRUCTURE

CEILING LAYOUT NOTES: LAY-IN CEILINGS ARE SHOWN CONCEPTUALLY. IT IS THE INTENT THE CEILINGS AREA CENTERED WITHIN THE ROOM. IN ODD SHAPED ROOMS, PRIMARY VISUAL AREA TO BE CENTERED. CEILING INSTALLER SHOULD CONSULT WITH THE ARCHITECT IN THE FIELD FOR ANY AREAS IN WHICH THEY WOULD LIKE TO MODIFY THE LAYOUT FROM THAT SHOWN ON THE PLAN. MODIFICATIONS MAY BE ALLOWED, AT THE DISCRETION OF THE ARCHITECT, TO EASE INSTALLATION, SAVE CUTTING, OR INCREASE VISUAL APPEAL.

GENERAL CEILING NOTES

1. GENERALLY CENTER CEILING GRIDS IN EACH ROOM AS SHOWN ON PLANS TO PROVIDE EQUALLY SIZED PANELS ON OPPOSITE WALLS. IF PLANS INDICATE A GRID ALIGNING WITH A COLUMN, WALL SOFFIT, ETC., START GRID AT INDICATED SURFACE.
2. SEE FLOOR PLAN FOR WALL TYPES AND WALLS THAT EXTEND FULL HEIGHT TO STRUCTURE.
3. SEE TYPICAL DETAILS THIS SHEET.
4. CEILING FIXTURES ARE SHOWN FOR REFERENCE ONLY FOR COORDINATION WITH CEILING FINISH SYSTEM. SEE MECHANICAL, ELECTRICAL AND SPRINKLER DRAWINGS FOR ALL CEILING FIXTURES AND TYPES.
5. SPOT ELEVATIONS ARE FROM FINISH FLOOR TO SURFACE FINISH OF CEILING AND ARE ROUNDED TO THE NEAREST INCH.

LINEWORK LEGEND

NEW CONSTRUCTION

EXISTING ELEMENTS TO REMAIN

mosaic
architecture-planning-design
317 Cruse Avenue Suite 201
Helena, Montana 59601
406.449.2013
www.mosaicarch.com

LICENSED ARCHITECT AR-986501
JEFFERY R. DOWNHOUR
STATE OF IDAHO

U.S. DEPARTMENT OF AGRICULTURE
FOREST SERVICE
R-1 NORTHERN REGION

POWELL DUPLEX RENOVATION

LOCHSA-POWELL RANGER DISTRICT
192 POWELL RD, LOLO, MT 59847
NEZ PERCE-CLEARWATER NATIONAL FORESTS

CONSTRUCTION DOCUMENTS


MARK	DATE	REVISION

PROJECT NO. 1240LU23F0138
DATE: 7/19/2024
Drawn By: Mosaic
Designed By: Mosaic
Checked By: Mosaic


REFLECTED CEILING PLANS

SHEET: **A104**


DATE STAMP - 7/19/2024 10:15:47 AM

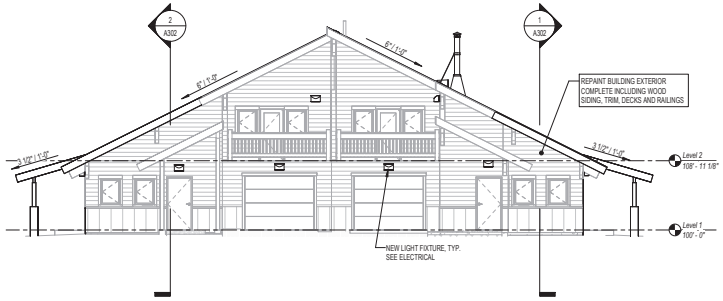


3 SOUTH ELEVATION
1/8" = 1'-0"

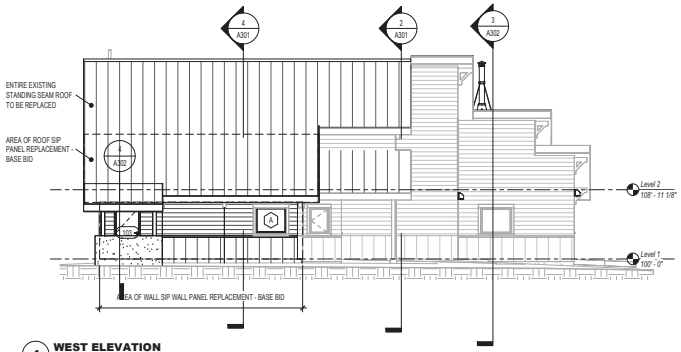

4 WEST ELEVATION
1/8" = 1'-0"

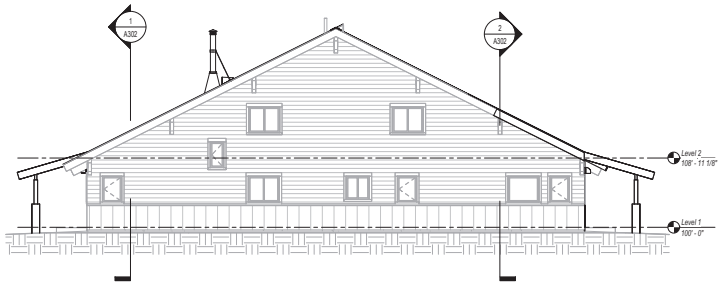

2 NORTH ELEVATION
1/8" = 1'-0"

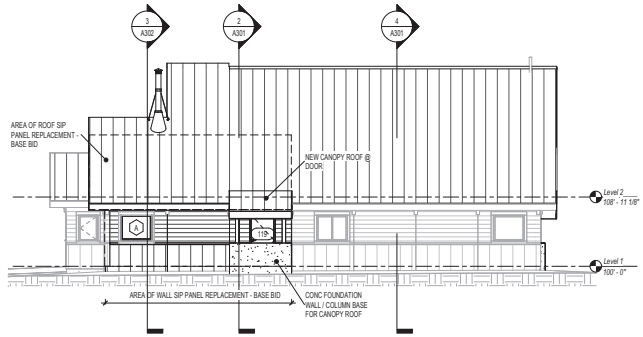

1 EAST ELEVATION
1/8" = 1'-0"

MATERIALS LEGEND

- STANDING SEAM METAL ROOF
- WOOD LAP SIDING - MATCH EXISTING PROFILE AND EXPOSURE - PAINTED COLOR P1
- STANDING SEAM METAL WAINSCOT - MATCH EXISTING PROFILE & COLOR


NOTES

1. THIS LEGEND DOES NOT INCLUDE ALL MATERIALS. SEE NOTES AND REFERENCED DETAILS FOR ADDITIONAL INFORMATION.
2. ALL EXPOSED WOOD & FIBER CEMENT TO BE PAINTED.
3. PAINT ALL WINDOW TRIM, WD SOFFITS & ROOF FASCIAS COLOR P11.

LINEWORK LEGEND

- NEW CONSTRUCTION
- EXISTING ELEMENTS TO REMAIN

WINDOW LEGEND

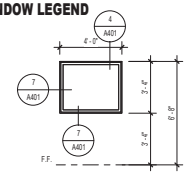

EXTERIOR T-1 GLASS
CLAD WOOD FIXED WINDOW
RE-USE EXISTING - VERIFY DIMENSIONS

mosaic
architecture-planning-design
317 Cruse Avenue Suite 201
Helena, Montana 59601
406.449.2013
www.mosaicarch.com

LICENSED ARCHITECT
AR-986501
JEFFERY R. DOWNHOUR
STATE OF IDAHO

U.S. DEPARTMENT OF AGRICULTURE
FOREST SERVICE
R-1 NORTHERN REGION

POWELL DUPLEX RENOVATION

LOCHSA-POWELL RANGER DISTRICT
192 POWELL RD, LOLO, MT 59847
NEZ PERCE-CLEARWATER NATIONAL FORESTS

CONSTRUCTION DOCUMENTS


MARK	DATE	REVISION

PROJECT NO. 1240LU23F0138
DATE: 7/19/2024
Drawn By: Mosaic
Designed By: Mosaic
Checked By: Mosaic


EXTERIOR ELEVATIONS

SHEET: A201

DATESTAMP - 7/19/2024 10:19:48 AM

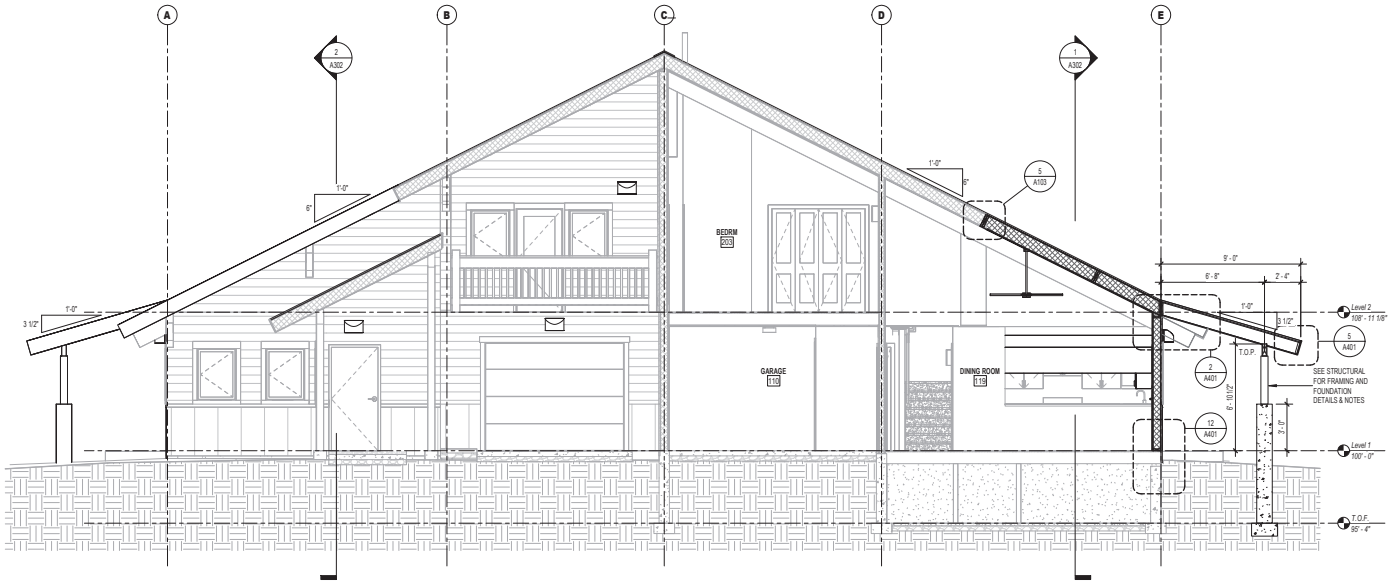

2 BUILDING SECTION
1/4" = 1'-0"

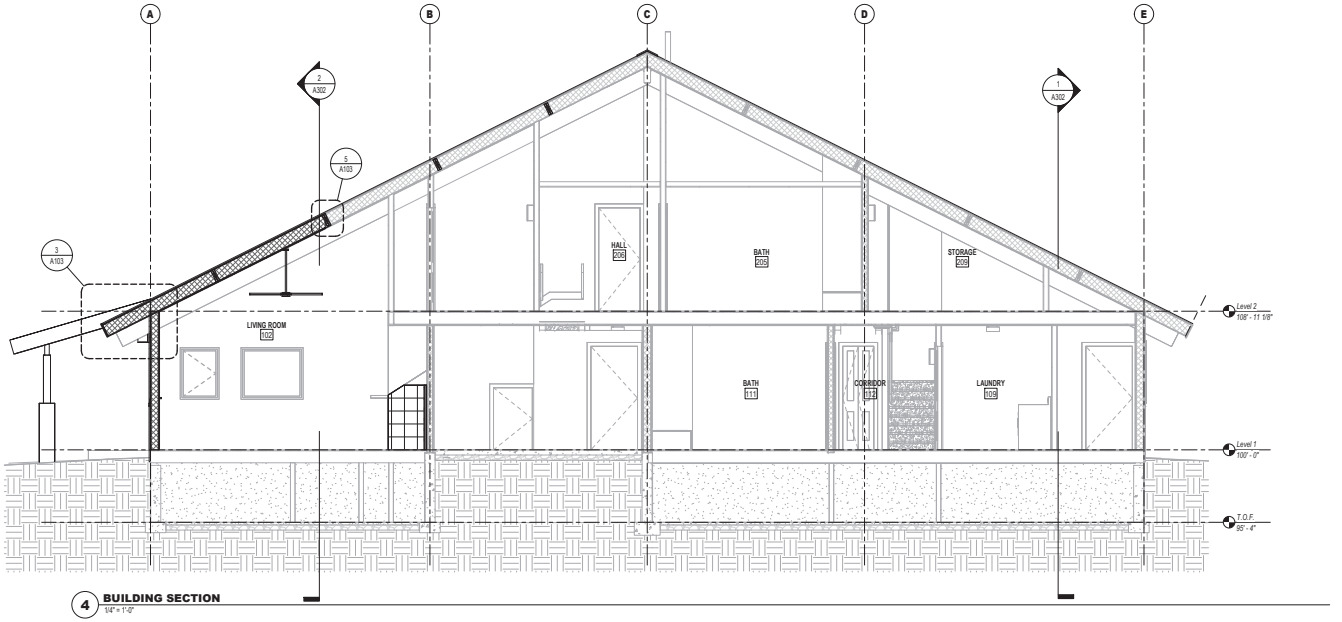

4 BUILDING SECTION
1/4" = 1'-0"

mosaic
architecture+planning+design
317 Cruse Avenue Suite 201
Helena, Montana 59601
406.449.2013
www.mosaicarch.com

LICENSED ARCHITECT
AR-986501
JEFFERY R. DOWNHOUR
STATE OF IDAHO

U.S. DEPARTMENT OF AGRICULTURE
FOREST SERVICE
R-1 NORTHERN REGION

POWELL DUPLEX RENOVATION

LOCHSA-POWELL RANGER DISTRICT
192 POWELL RD, LOLO, MT 59847
NEZ PERCE-CLEARWATER NATIONAL FORESTS

CONSTRUCTION DOCUMENTS

MARK	DATE	REVISION

PROJECT NO. 1240LU23F0138
DATE: 7/19/2024
Drawn By: Mosaic
Designed By: Mosaic
Checked By: Mosaic

BUILDING SECTIONS


SHEET: **A301**

DATESTAMP - 7/19/2024 10:15:49 AM


SECTION KEYNOTES

NOTE: SEE MECH/ELEC/STRUCT AND CIVIL DRAWINGS FOR ADDITIONAL INFORMATION.


1. NEW SIP WALL PANEL PER STRUCTURAL
2. NEW SIP ROOF PANEL PER STRUCTURAI
3. RE-MOUNT EXISTING BEAM AND UPPER CABINETS IF REMOVED TO ALLOW REPLACEMENT OF COLUMN AT SIP WALL.. ATTACH BEAM TO NEW COLUMN

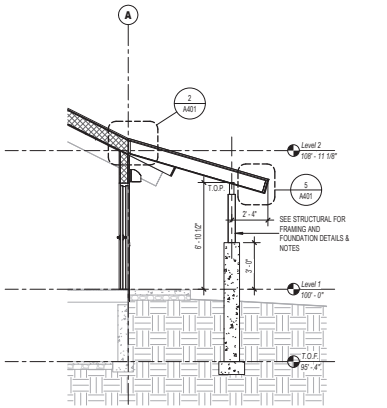


4 SECTION AT PORCH ROOF
1/4" = 1'-0"

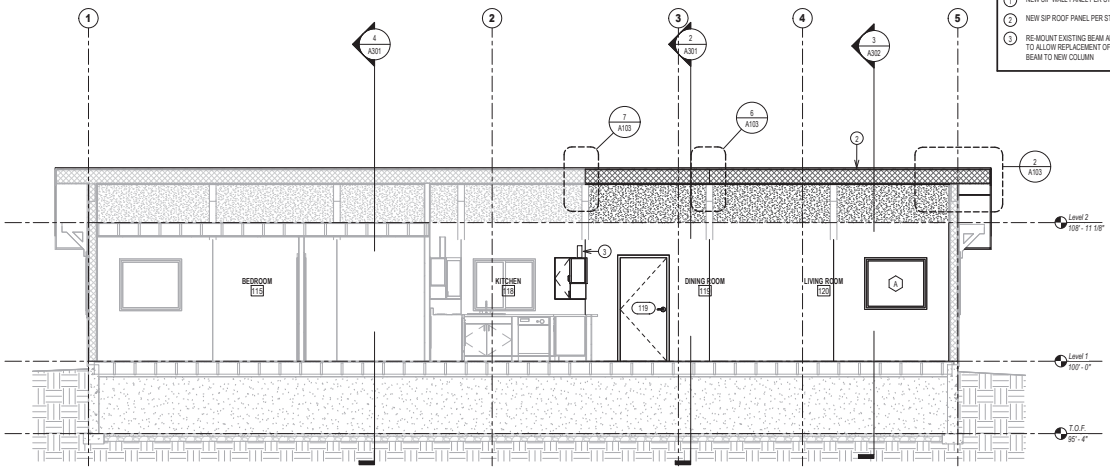

1 BUILDING SECTION
1/4" = 1'-0"

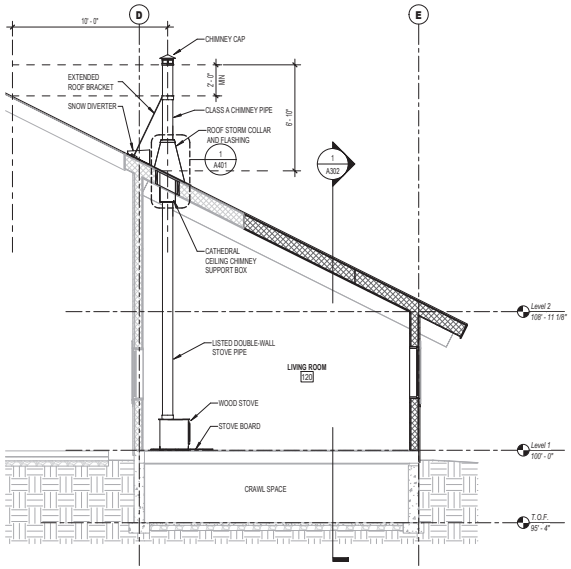

3 SECTION AT WOODSTOVE
1/4" = 1'-0"

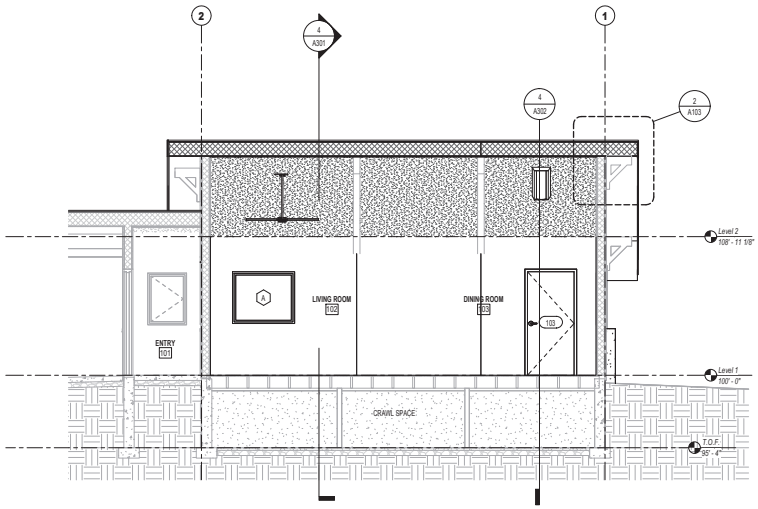

2 BUILDING SECTION
1/4" = 1'-0"

mosaic
architecture-planning-design
317 Cruse Avenue Suite 201
Helena, Montana 59601
406.449.2013
www.mosaicarch.com

LICENSED ARCHITECT
AR-986501
JEFFERY R. DOWNHOUR
STATE OF IDAHO

FOREST SERVICE
U.S. DEPARTMENT OF AGRICULTURE

U.S. DEPARTMENT OF AGRICULTURE
FOREST SERVICE
R-1 NORTHERN REGION

POWELL DUPLEX RENOVATION

LOCHSA-POWELL RANGER DISTRICT
192 POWELL RD, LOLO, MT 59847
NEZ PERCE-CLEARWATER NATIONAL FORESTS

CONSTRUCTION DOCUMENTS


MARK	DATE	REVISION

PROJECT NO. 1240LU23F0138
DATE: 7/19/2024
Drawn By: Mosaic
Designed By: Mosaic
Checked By: Mosaic


BUILDING SECTIONS

SHEET: **A302**


DATE STAMP: 7/19/2024 10:18:50 AM

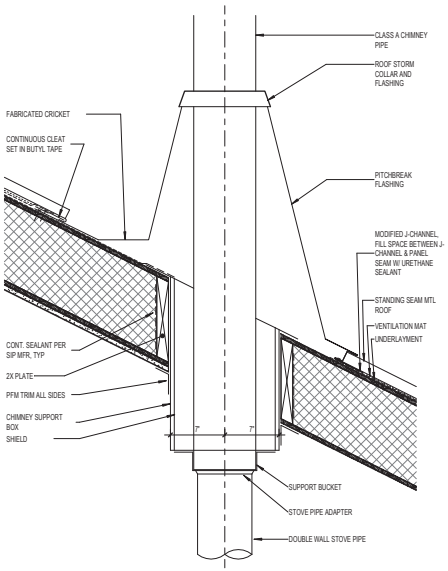


1 SIP ROOF AT CHIMNEY PENETRATION
1 1/2" = 1'-0"

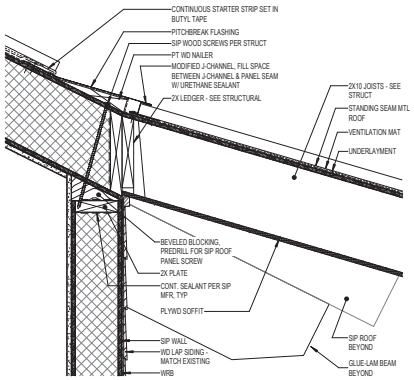


2 SIP ROOF AT PORCH ROOF
1 1/2" = 1'-0"

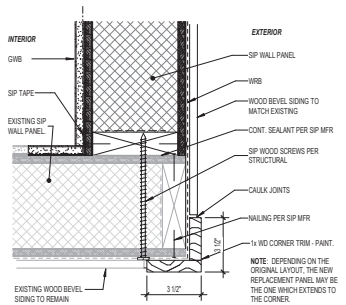


3 SIP WALL CORNER DETAIL
3" = 1'-0"

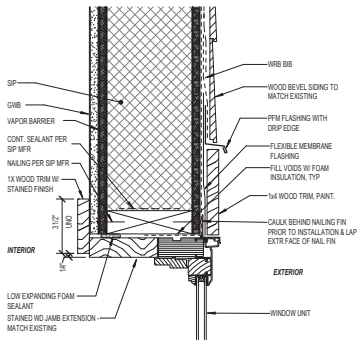


4 WINDOW HEAD AT SIP
3" = 1'-0"

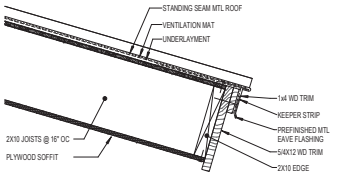


5 PORCH ROOF AT LOW EAVE
1 1/2" = 1'-0"

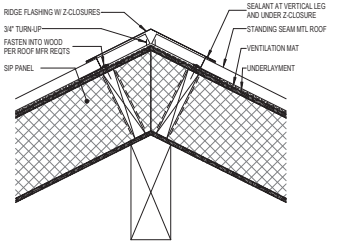


6 SIP ROOF AT RIDGE
1 1/2" = 1'-0"

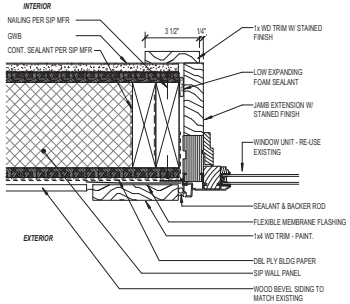


7 WINDOW JAMB AT SIP
3" = 1'-0"

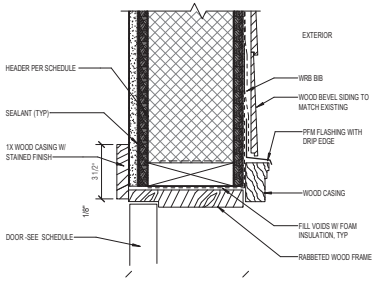


8 EXTERIOR DOOR HEAD @ SIP WALL
3" = 1'-0"

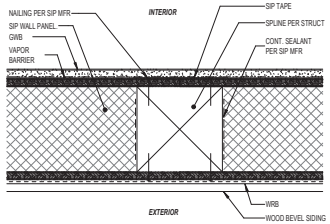


9 NEW SIP WALL & SPLINE
3" = 1'-0"

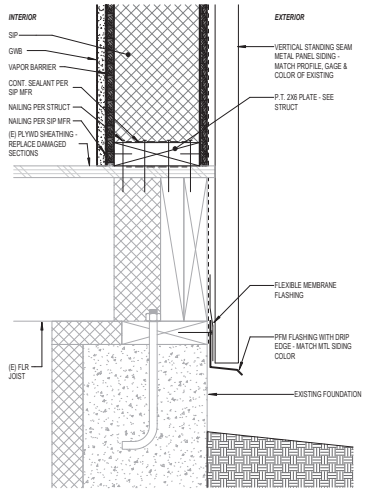


12 SIP WALL AT EXSTING FOUNDATION
3" = 1'-0"

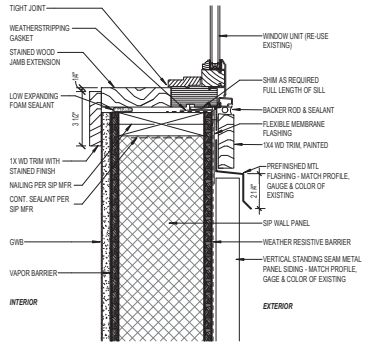

13 WINDOW SILL AT SIP
3" = 1'-0"

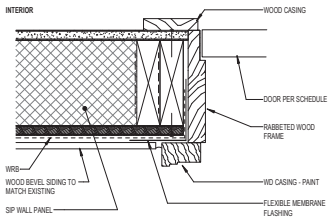

10 EXTERIOR DOOR JAMB @ SIP WALL
3" = 1'-0"

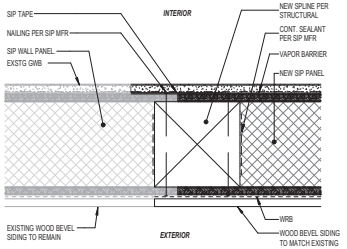

11 NEW SIP WALL & SPLINE AT EXISTING
3" = 1'-0"

mosaic
architecture-planning-design
317 Cruse Avenue Suite 201
Helena, Montana 59601
406.449.2013
www.mosaicarch.com

LICENSED ARCHITECT AR-986501
JEFFERY R. DOWNHOUR
STATE OF IDAHO

U.S. DEPARTMENT OF AGRICULTURE
FOREST SERVICE
R-1 NORTHERN REGION

POWELL DUPLEX RENOVATION

LOCHSA-POWELL RANGER DISTRICT
192 POWELL RD, LOLO, MT 59847
NEZ PERCE-CLEARWATER NATIONAL FORESTS

CONSTRUCTION DOCUMENTS

MARK	DATE	REVISION

PROJECT NO. 1240LU23F0138
DATE: 7/19/2024
Drawn By: Mosaic
Designed By: Mosaic
Checked By: Mosaic

EXTERIOR DETAILS

SHEET: **A401**


DATE STAMP - 7/19/2024 10:18:51 AM

DOOR SCHEDULE

MARK	ROOM NAME	DOOR TYPE	WIDTH	HEIGHT	THICKNESS	DOOR MAT'L	DOOR FINISH	FRAME TYPE	FRAME MAT'L	FRAME FINISH	DOOR HDWR GROUP	FIRE RAT'G	COMMENTS
103	DINING ROOM	P-SD	3' - 0"	6' - 8"	1 3/4"	STL CLAD	PAINT	A	WD	PAINT	1	-	REPAINT & REUSE EXISTING ENTRY DOOR; NEW STORM DOOR
119	DINING ROOM	P-SD	3' - 0"	6' - 8"	1 3/4"	STL CLAD	PAINT	A	WD	PAINT	1	-	NEW ENTRY DOOR & STORM DOOR

DOOR TYPES

SEE PLAN AND SCHEDULE FOR ALL DOOR SIZES

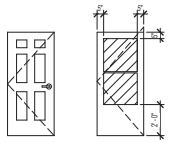


P
6-PANEL
INSULATED 24 GA. GALV STEEL CLAD PREHUNG DOOR. PRIMED

SD
STORM DOOR
WOOD CORE MID VIEW GLAZED W/ RETRACTABLE SCREEN. MFR: LARSON BISMARCK, OAE PREFINISHED: BROWN

DOOR FRAME TYPES

SEE PLAN AND SCHEDULE FOR DOOR SIZES

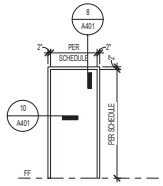

A
WD FRAME FOR PREHUNG DOOR

GENERAL DOOR NOTES

1. ALL DOOR LOCATIONS NOT SPECIFICALLY DIMENSIONED TO BE PLACED 4 INCHES FROM ADJACENT WALL SURFACE. IF THERE IS NO DIRECTLY ADJACENT SIDEWALL, CONTACT ARCHITECT FOR PROPER PLACEMENT.
2. ALL DOORS TO HAVE ADA COMPLIANT THRESHOLDS WITH 1/2" MAXIMUM RISE UNLESS SPECIFICALLY DETAILED OTHERWISE.
3. ALL METAL DOORS AND FRAMES TO BE PRIMED AND PAINTED. VERIFY COLOR WITH ARCHITECT.
4. ALL EXTERIOR DOORS TO BE FULLY INSULATED.
5. ALL EXTERIOR DOORS TO HAVE FULL PERIMETER WEATHERSTRIPPING.
6. ALL HARDWARE ON FIRE-RATED DOORS MUST BE APPROVED FOR SUCH USE AND INSTALLED AS REQUIRED TO MAINTAIN SYSTEM FIRE RATING.
7. ALL DOORS/FRAMES TO HAVE RESILIENT SILENCERS.
8. CONTRACTOR TO USE ARCHITECT'S DOOR TYPE PLAN DESIGNATION NUMBER IN ADDITION TO THE ROOM NUMBER ON ALL SHOP DRAWING SUBMITTALS
9. FIRE RATING FOR FRAMES MUST MATCH RATING FOR DOORS.
10. SEE WINDOW ELEVATIONS FOR FRAME TYPES FOR ALUMINUM FRAMES.
11. ALL EGRESS DOORS SHALL BE READILY OPENABLE FROM THE EGRESS SIDE WITHOUT THE USE OF A KEY OR SPECIAL KNOWLEDGE OR EFFORT.

GLAZING LEGEND

1/4" LAMINATED SAFETY GLAZING

ABBREVIATIONS

ALUM	ALUMINUM
ANOD	ANODIZED FINISH - DK BRONZE
FACT	FACTORY FINISH
HM	HOLLOW METAL
MFR	MANUFACTURER
SF	ALUMINUM STOREFRONT
STL	STEEL
WD	WOOD - SOLID CORE

ROOM FINISH SCHEDULE

NO.	ROOM NAME	AREA	PERIMETER	FLOOR FINISH	BASE FINISH	NORTH WALL	EAST WALL	SOUTH WALL	WEST WALL	CEILING FINISH	COMMENTS
101	ENTRY	32 SF	23'-6"	LVT	RB1						
102	LIVING ROOM	219 SF	59'-10"	LVT	RB1	-	P1	P1	01	P1	
103	DINING ROOM	170 SF	51'-11"	LVT	RB1	P1	P1	-	01	P1	
104	STAIRS	29 SF	24'-10"	LVT	RB1						
105	BATH	33 SF	23'-3"	SV1	RB1						
106	KITCHEN	163 SF	68'-11"	LVT	RB1	P1	P1	P1	01	P1	
107	LAUNDRY	17 SF	17'-0"	SV1	RB1						
108	GARAGE	272 SF	69'-7"	-	-						
109	LAUNDRY	55 SF	29'-7"	SV1	RB1						
110	GARAGE	308 SF	72'-2"	-	-						
111	BATH	80 SF	36'-9"	SV1	RB1						
112	CORRIDOR	100 SF	58'-1"	LVT	RB1	P1	P1	P1	01	P1	
113	STAIR	47 SF	36'-9"	CPT1	RB1						
114	BEDROOM	146 SF	53'-7"	LVT	RB1						
115	BEDROOM	202 SF	67'-0"	LVT	RB1						
118	KITCHEN	126 SF	54'-5"	LVT	RB1	P1	P1	-	01	P1	
119	DINING ROOM	233 SF	61'-10"	LVT	RB1	P1	P1	P1	01	P1	
120	LIVING ROOM	163 SF	53'-4"	LVT	RB1	-	P1	P1	01	P1	
121	ENTRY	33 SF	23'-9"	LVT	RB1						
201	BEDRM	185 SF	60'-1"	CPT1	RB1						
202	BEDRM	191 SF	62'-3"	CPT1	RB1						
203	BEDRM	265 SF	74'-10"	CPT1	RB1						
204	BEDRM	146 SF	53'-10"	CPT1	RB1						
205	BATH	100 SF	46'-3"	SV1	RB1						
206	HALL	63 SF	43'-3"	CPT1	RB1						
209	STORAGE	191 SF	64'-7"	-	-						
210	HALL	66 SF	48'-10"	CPT1	RB1						

ADDITIVE ALTERNATE NO. 2

BASE BID: PAINT ROOMS PER FINISH SHEDULE
ALTERNATE: PAINT ALL ROOMS (WALLS & CEILINGS, P1) EXCEPT GARAGES AND STORAGE 209

SEE FINISH SCHEDULE FOR LISTING OF MATERIALS .

GENERAL FINISH NOTES:

1. ALL PAINTING, WALLCOVERING & GYPSUM WALLBOARD FINISHING PER SPECIFICATIONS AND DECORATING CONTRACTORS OF AMERICA.
2. PROVIDE SAMPLES OF SPECIFIED FINISHES TO ARCHITECT FOR APPROVAL PRIOR TO APPLICATION
3. PROVIDE TO OWNER APPROXIMATELY 5% OF ADDITIONAL FINISH MATERIAL FOR FUTURE REPAIR AND MAINTENANCE. (I.E. - PAINT, VINYL FLOORING, RUBBER BASE, ETC.)

FLOOR FINISH NOTES:


1. IF FINISHES ARE NOT CLEARLY INDICATED FOR AN AREA, CLARIFY INTENT WITH ARCHITECT.
2. PROVIDE APPROPRIATE TRANSITION TRIM AT ALL MATERIAL CHANGES.
3. PROVIDE EXTRUDED ALUMINUM EDGE METAL AT TERMINATION OF ALL CERAMIC TILE AREAS.
4. TEST ALL SUBSTRATES TO VERIFY COMPLIANCE WITH FINISH MANUFACTURER'S SPECIFICATIONS PRIOR TO FLOORING INSTALLATION.
5. PATCH, REPAIR, AND/OR GRIND ALL SUBSTRATES TO ACCEPTABLE LEVEL OF SMOOTHNESS/LEVELNESS PRIOR TO FLOORING INSTALLATION. **IF SUBSTRATE IS WATER DAMAGED AND REQUIRES REPLACEMENT, NOTIFY CONTRACTING OFFICER.**
6. FLOORING CHANGES FROM ROOM TO ROOM TO OCCUR DIRECTLY UNDER THE DOOR LOCATION.

WALL FINISH NOTES:


1. IF FINISHES ARE NOT CLEARLY INDICATED FOR AN AREA, CLARIFY INTENT WITH ARCHITECT.
2. PROVIDE APPROPRIATE TRANSITION TRIM AT ALL MATERIAL CHANGES.
3. PROVIDE CLEAN, CONSISTENT CAULK JOINTS AT ABUTMENTS OF DISSIMILAR MATERIALS.
4. PROVIDE METAL EDGING AT ALL GYPSUM BOARD EDGES THAT ABUT DISSIMILAR MATERIALS.
5. PROVIDE BULLNOSE TILES AT ALL EXPOSED TILE EDGES.

CEILING FINISH NOTES:

1. IF FINISHES ARE NOT CLEARLY INDICATED FOR AN AREA, CLARIFY INTENT WITH ARCHITECT.
2. PROVIDE APPROPRIATE TRANSITION TRIM AT ALL MATERIAL CHANGES.
3. PROVIDE CLEAN, CONSISTENT CAULK JOINTS AT ABUTMENTS OF DISSIMILAR MATERIALS.

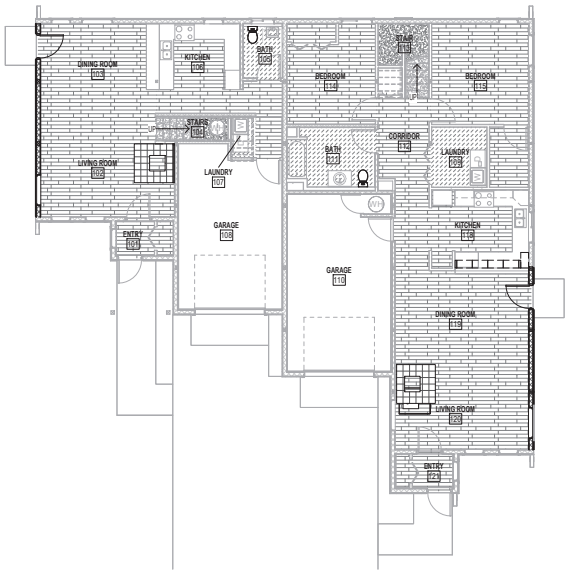

1 **LEVEL 1 FINISH PLAN**
1/8" = 1'-0"

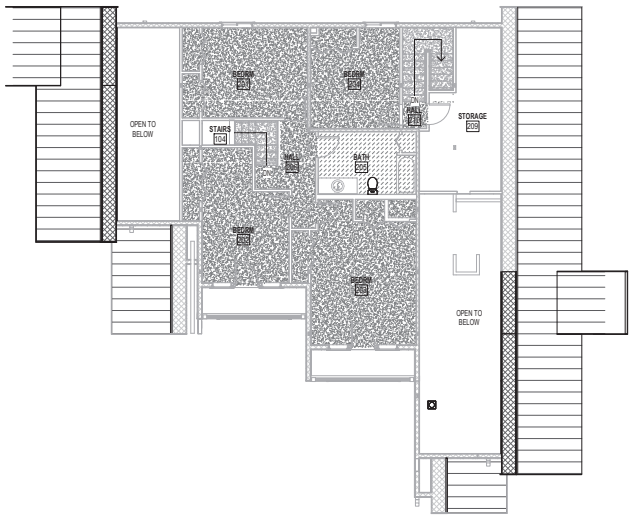

2 **LEVEL 2 FINISH PLAN**
1/8" = 1'-0"

ROOM FINISH LEGEND

FLOOR FINISHES

CPT1 LVT1 SV1 PT1 (E)

CPT1: BROADLOOM CARPET - SHAW CONTRACT, STYLE & COLOR TO BE SELECTED BY ARCH
LVT1: LUXURY VINYL TILE: SHAW CONTRACT, 22 MIL, 5 MM THICK, STYLE & COLOR TO BE SELECTED BY ARCH
SV1: SHEET FLOORING - TARKETT iQ GRANITE (HOMOGENEOUS) - COLOR TO BE SELECTED B ARCH
PT1: PORCELAIN TILE STOVE BOARD, TYPE 2
(E): EXISTING FINISH - NO WORK

BASE FINISH

RB1: 4" RUBBER BASE - TARKETT 'TIGHTLOCK' RESILIENT 4.375" - COLOR TO BE SELECTED

FLOOR AND BASE FINISH NOTES:
1. SEE SPECIFICATIONS FOR FINISH MANUFACTURER.
2. ALL FLOORING TO BE INSTALLED ON MANUFACTURERED APPROVED SUB FLOOR.
3. INSTALL FACTORY-PROVIDED TRANSITION STRIP OR AS DETAILED AT ALL FLOORING CHANGES.
4. CHANGE FLOORING WHERE INDICATED ON PLANS, CHANGE FLOOR CENTERED UNDER DOOR AT ROOM TO ROOM CHANGES, U.N.O
5. AT CASEWORK, CONTINUE BASE AROUND ENDPANELS AND TOE-KICKS, U.N.O.

CEILING FINISHES GYPSUM WALL BOARD

WALL FINISHES

PAINT NOTE: MANUFACTURERS SHOWN ARE BASIS OF DESIGN ONLY. SUBSTITUTIONS ALLOWED WITH APPROVAL; SEE SPEC SECTION ON SUBSTITUTIONS. VERIFY FINAL PAINT COLORS AND LOCATIONS W/ ARCHITECT PRIOR TO INSTALLATION.

P1: PAINT - COLOR: TO BE SELECTED BY ARCH
P2: PAINT - COLOR: TO BE SELECTED BY ARCH
PT1: PORCELAIN TILE STOVE BOARD, TYPE 2. MOUNT W/ NONCOMBUSTIBLE SPACERS FOR 1" AIR SPACE

WOOD DOOR & WINDOW FRAMES (NEW)
STAIN TO MATCH EXISTING

WALL FINISHES NOTES:
1. SEE INTERIOR ELEVATIONS AND/OR DETAILS FOR INTERIOR WINDOWS, SPECIAL WALL FINISHES, TRIM, ETC.
2. FINISH SCHEDULE APPLIES TO GENERAL AREA. THERE MAYBE SPECIFIC FINISH REQUIREMENTS SHOWN ON DETAILS, DRAWINGS OR SPECIFICATIONS.
3. SEE SPECIFICATIONS FOR LEVEL(S) OF FINISH AT GWB SURFACES.
4. ALL WALLS/CEILINGS P1 UNLESS OTHERWISE NOTED ON PLANS &/OR ELEVATIONS.

mosaic
architecture · planning · design
317 Cruse Avenue Suite 201
Helena, Montana 59601
406.449.2013
www.mosaicarch.com

LICENSED ARCHITECT
AR-986501
JEFFERY R. DOWNHOUR
STATE OF IDAHO

U.S. DEPARTMENT OF AGRICULTURE
FOREST SERVICE
R-1 NORTHERN REGION

POWELL DUPLEX RENOVATION

LOCHSA-POWELL RANGER DISTRICT
192 POWELL RD, LOLO, MT 59847
NEZ PERCE-CLEARWATER NATIONAL FORESTS

CONSTRUCTION DOCUMENTS

MARK	DATE	REVISION

PROJECT NO. 1240LU23F0138
DATE: 7/19/2024
Drawn By: Mosaic
Designed By: Mosaic
Checked By: Mosaic

DOOR & FINISH SCHEDULE

SHEET: **A701**

DATESTAMP - 7/19/2024 10:18:53 AM

GENERAL STRUCTURAL NOTES:

THESE DRAWINGS HAVE BEEN PREPARED SOLELY FOR USE IN THE CONSTRUCTION OF THE POWELL DUPLEX RENOVATION AT THE LOCATION OF LOCHSA-POWELL RANGER DISTRICT, 192 POWELL RD, LOLO, ID 59847. POSSESSION OF THESE DRAWINGS DOES NOT GRANT A LICENSE TO CONSTRUCT OR FABRICATE THE WHOLE, OR PARTS OF THIS PROJECT IN OTHER LOCATIONS.

STRUCTURAL DRAWINGS ARE A PORTION OF THE CONTRACT DOCUMENTS AND ARE INTENDED TO BE USED WITH ARCHITECTURAL, MECHANICAL, ELECTRICAL, AND SITE CIVIL DRAWINGS. THE CONTRACTOR IS RESPONSIBLE FOR COORDINATING THE REQUIREMENTS FROM THESE DRAWINGS INCLUDING BUT NOT LIMITED TO DIMENSIONS, BLOCKOUTS, OPENINGS, SLEEVES, EMBEDDED ITEMS, ETC. INTO THEIR SHOP DRAWINGS AND WORK. NOTIFY THE CONTRACTING OFFICER OF ANY DISCREPANCIES OR IF ACTUAL CONDITIONS DIFFER FROM THOSE SHOWN OR NOTED.

THESE GENERAL NOTES SUPPLEMENT THE PROJECT SPECIFICATIONS. REFER TO THE PROJECT SPECIFICATIONS FOR ADDITIONAL REQUIREMENTS. NOTES AND DETAILS ON THE STRUCTURAL DRAWINGS SHALL TAKE PRECEDENCE OVER THE GENERAL NOTES AND TYPICAL DETAILS. WHERE NO DETAILS ARE GIVEN, CONSTRUCTION SHALL BE AS SHOWN FOR SIMILAR WORK.

THE CONTRACTOR SHALL FURNISH THE PRODUCTS SPECIFIED ON THE DRAWINGS. SUBSTITUTIONS WILL BE CONSIDERED ONLY IF THE CONTRACTOR PROVIDES DOCUMENTAION TO PROVE THE ALTERNATIVE EQUALS OR EXCEEDS THE STRUCTURAL PERFORMANCE CHARACTERISTICS OF THE SPECIFIED PRODUCT.

EXTENT OF STRUCTURAL SCOPE IS REPLACMENT IN KIND OF DAMAGED STRUCTURAL MEMBERS AND ADDITIONAL OF EAST UNIT AWNING.

CODE REQUIREMENTS:
ALL WORK SHALL BE IN STRICT COMPLIANCE WITH:
- A. 2018 INTERNATIONAL BUILDING CODE (IBC) AS AMENDED BY THE STATE OF IDAHO (INTERNATIONAL BUILDING CODE, 2018 EDITION, EFFECTIVE JANUARY 1, 2021)
- B. ALL OTHER STATE AND LOCAL BUILDING REQUIREMENTS THAT APPLY.

TEMPORARY CONDITIONS:
CONTRACTOR SHALL PROVIDE ALL NECESSARY TEMPORARY SUPPORT PRIOR TO COMPLETION OF VERTICAL AND LATERAL LOAD SYSTEMS. MORRISON-MAIERLE HAS NOT BEEN RETAINED TO PROVIDE ANY SERVICES RELATED TO JOB SITE SAFETY PRECAUTIONS, OR TO REVIEW THE MEANS, METHODS, TECHNIQUES, SEQUENCES, OR PROCEDURES FOR THE CONTRACTOR TO PERFORM WORK. UNLESS WE ARE SPECIFICALLY RETAINED AND COMPENSATED TO DO OTHERWISE, OUR WORK IS LIMITED TO THE FINAL DESIGN OF THE WORK DESCRIBED ON OUR DRAWINGS FOR THIS PROJECT.

CONTRACTOR'S CONSTRUCTION AND/OR ERECTION SEQUENCES SHALL RECOGNIZE AND CONSIDER THE EFFECTS OF THERMAL MOVEMENTS OF STRUCTURAL ELEMENTS DURING THE CONSTRUCTION PERIOD.

EXISTING CONDITIONS:
EXISTING BUILDING/SITE DIMENSIONS AND ASSUMED CONDITIONS ARE TO BE VERIFIED IN THE FIELD AND ARE THE RESPONSIBILITY OF THE CONTRACTOR. THE CONTRACTOR SHALL NOTIFY THE CONTRACTING OFFICER OF ALL DISCREPANCIES WHICH REQUIRE A SIGNIFICANT CHANGE IN THE DESIGN AND/OR CONSTRUCTION FROM THAT SHOWN ON THE DRAWINGS.

REFER TO 'INITIAL SITE VISIT AND INFORMATION GATHERING' REPORT DATED NOVEMBER 9, 2022 FOR ADDITIONAL INFORMATION REGARDING THE EXISTING CONDITIONS OF THE BUILDING.

ASSUMED FUTURE CONSTRUCTION:
VERTICAL: NONE
HORIZONTAL: NONE

DESIGN CRITERIA:
DESIGN IS BASED ON THE FOLLOWING LOADING FOR THE BASIS OF STRENGTH, PERFORMANCE, AND SERVICEABILITY OF THE STRUCTURE:

DESIGN CRITERIA		
ROOF LIVE LOAD CRITERIA (IBC 1603.1.2)		
ORDINARY FLAT, PITCHED, CURVED	20 PSF (SEE SNOW LOAD)	N/A
SNOW LOAD CRITERIA (IBC 1603.1.3)		
DESIGN ROOF SNOW LOAD	60 PSF	
SNOW DRIFT	PER ASCE 7-16 AS SHOWN ON PLANS	
GROUND SNOW LOAD	Pg = 122 PSF (REF. 2015 IDAHO GROUND SNOW LOAD MAP)	
FLAT ROOF SNOW LOAD	Pf = 85.4 PSF	
SNOW EXPOSURE FACTOR	Ce = 1.0	
SNOW LOAD IMPORTANCE FACTOR	Is = 1.0	
THERMAL FACTOR	Ct = 1.0	
SLOPE FACTOR	Cs = 0.7 (SLOPE = 6/12, WARM ROOF), UNOBSTRUCTED, SLIPPERY SURFACE	
WIND LOAD CRITERIA (IBC 1603.1.4)		
BASIC DESIGN WIND SPEED	V = 105 MPH	
RISK CATEGORY	II	
WIND EXPOSURE	B	
SEISMIC LOAD CRITERIA (IBC 1603.1.5)		
RISK CATEGORY	II	
SEISMIC IMPORTANCE FACTOR	Ie = 1.0	
MAPPED SPECTRAL RESPONSE	Ss = 0.298	S1 = 0.105
SITE CLASS	D (ASSUMED)	
DESIGN SPECTRAL RESPONSE	Sds = 0.310	Sd1 = 0.167
SEISMIC DESIGN CATEGORY	C	

SUBMITTALS:
SHOP DRAWINGS SHALL BE SUBMITTED TO THE CONTRACTING OFFICER PRIOR TO FABRICATION AND CONSTRUCTION OF ALL STRUCTURAL PRODUCTS, INCLUDING THE FOLLOWING:

SUBMITTALS		
ITEM	SUBMITTAL	DEFERRED SUBMITTAL
STRUCTURAL INSULATED PANELS	X	

SHOP DRAWINGS SUBMITTALS SHALL BE SUBMITTED TO THE CONTRACTING OFFICER PRIOR TO FABRICATION AND CONSTRUCTION FOR ALL STRUCTURAL PRODUCTS DELIVERED TO THE PROJECT. IF THE SHOP DRAWINGS DEVIATE FROM OR ADD TO THE DESIGN OF THE STRUCTURAL DRAWINGS, THEY SHALL BEAR THE SEAL AND SIGNATURE OF A STRUCTURAL ENGINEER REGISTERED IN THE STATE WHERE THE PROJECT IS LOCATED. ANY CHANGES TO THE STRUCTURAL DRAWINGS SHALL BE SUBMITTED TO THE ARCHITECT AND ARE SUBJECT TO REVIEW AND ACCEPTANCE OF THE CONTRACTING OFFICER.

THE CONTRACTOR SHALL COORDINATE SEISMIC RESTRAINTS OF MECHANICAL, PLUMBING AND ELECTRICAL EQUIPMENT, MACHINERY AND ASSOCIATED PIPING WITH THE STRUCTURE. CONNECTIONS TO STRUCTURE SHALL BE DESIGNED BY AN ENGINEER REGISTERED IN THE STATE WHERE THE PROJECT IS LOCATED AND SHALL BE SUBMITTED TO THE CONTRACTING OFFICER PRIOR TO CONSTRUCTION.

FIELD ENGINEERED DETAILS DEVELOPED BY THE CONTRACTOR THAT DEVIATE FROM OR ADD TO THE STRUCTURAL DRAWINGS SHALL BEAR THE SEAL AND SIGNATURE OF A STRUCTURAL ENGINEER REGISTERED IN THE STATE WHERE THE PROJECT IS LOCATED AND SHALL BE SUBMITTED TO THE CONTRACTING OFFICER PRIOR TO CONSTRUCTION.

THE USE OF REPRODUCTIONS OR PHOTOCOPIES OF THE CONTRACT DOCUMENTS SHALL NOT BE PERMITTED. WHEN CAD OR REVIT FILES ARE PROVIDED TO THE CONTRACTOR OR SUBCONTRACTORS, IT IS THE RESPONSIBILITY OF THE DETAILERS TO REMOVE ALL INFORMATION NOT DIRECTLY RELEVANT TO THE CREATION OF THE PLACING DRAWINGS AS WELL AS ALL REFERENCES TO THE OUTSIDE SOURCE FILES.

SUBMITTAL DOCUMENTS SHALL BE REVIEWED BY THE CONTRACTOR PRIOR TO BEING SUBMITTED TO THE CONTRACTING OFFICER FOR REVIEW.

THE CONTRACTOR SHALL BE RESPONSIBLE FOR PROVIDING THE REVIEWED SUBMITTAL TO THE BUILDING DEPARTMENT FOR DEFERRED PERMIT APPLICATION. THE DEFERRED SUBMITTAL ITEMS SHALL NOT BE INSTALLED UNTIL THEIR DESIGN AND SUBMITTAL DOCUMENTS HAVE BEEN APPROVED BY THE BUILDING OFFICIAL.

DATESTAMP 7/9/2024 2:41:05 PM

CONCRETE:

CAST-IN-PLACE CONCRETE:
CONCRETE SHALL BE IN ACCORDANCE WITH ACI 301, *SPECIFICATION FOR STRUCTURAL CONCRETE*, AND ACI 117, *SPECIFICATION FOR TOLERANCES FOR CONCRETE CONSTRUCTION AND MATERIALS*, UNLESS NOTED OTHERWISE.

AVERAGE CONCRETE STRENGTH DETERMINED BY JOB CAST LAB CURED CYLINDER TO BE AS INDICATED BELOW PLUS INCREASE DEPENDING ON THE PLANT'S STANDARD DEVIATION AS SPECIFIED IN ACI 318.
MINIMUM CONCRETE PROPERTIES SHALL BE AS FOLLOWS:

CONCRETE PROPERTIES						
USE	EXPOSURE	MIN COMPRESSIVE STRENGTH	TEST AGE DAYS	AIR CONTENT	MAX WATER TO CEMENT RATIO	MAX AGGERGATE SIZE
EXTERIOR FOOTINGS AND WALLS	F2	4,500 PSI	28	6% +/- 1.5%	0.45	1"

THE CONTRACTOR SHALL SUBMIT CONCRETE MIX DESIGNS ALONG WITH TEST DATA A MINIMUM OF TWO WEEKS PRIOR TO PLACING CONCRETE.

CONDUITS EMBEDDED IN SLABS SHALL NOT BE LARGER IN OUTSIDE DIMENSION THAN ONE THIRD OF THE THICKNESS OF THE SLAB AND SHALL NOT BE SPACED CLOSER THAN THREE DIAMETERS ON CENTER.

CURING OF CONCRETE SHALL COMPLY WITH ACI 308, UNLESS NOTED OTHERWISE.

WHERE CONCRETE IS PLACED AGAINST EXISTING CONCRETE, THE EXISTING CONCRETE SURFACE SHALL BE CLEANED AND ROUGHENED TO A MINIMUM 1/4" AMPLITUDE.

PROVIDE 3/4" CHAMFERS ON ALL EXPOSED CONCRETE CORNERS UNLESS NOTED OTHERWISE.

SHORING DESIGN IS THE CONTRACTOR'S RESPONSIBILITY. SHORING FORMWORK SHALL NOT BE REMOVED FROM HORIZONTAL MEMBERS BEFORE CONCRETE STRENGTH IS AT LEAST 70 PERCENT OF DESIGN STRENGTH AS DETERMINED BY FIELD CURED CYLINDERS.

REINFORCING STEEL:
REINFORCING STEEL SHALL CONFORM TO THE FOLLOWING PROPERTIES:

REINFORCEMENT STEEL PROPERTIES		
USE	REINFORCEMENT SIZE	SPECIFICATION
GENERAL USE	ALL SIZES	ASTM A615, GRADE 60

REINFORCING STEEL TO BE WELDED SHALL USE ONLY LOW HYDROGEN ELECTRODES. ALL WELDING TO BE IN COMPLIANCE WITH AWS D1.4. WELD REINFORCING STEEL ONLY WHERE INDICATED ON THE DRAWINGS. WELDING OR TACK WELDING OF REINFORCEMENT BARS TO OTHER BARS OR STEEL COMPONENTS IS PROHIBITED.

REINFORCING STEEL IN BEAMS AND SLABS SHALL BE SUPPORTED ON CONCRETE DOBBIES, OR APPROVED CHAIRS IN SUFFICIENT NUMBERS TO SUPPORT THE BARS WITHOUT SETTLEMENT. FABRICATE AND INSTALL REINFORCING STEEL ACCORDING TO THE MANUAL OF STANDARD PRACTICE FOR DETAILING REINFORCED CONCRETE STRUCTURES - ACI STANDARD 315.

CONTACT LAP ALL REINFORCING BARS PER THE TYPICAL LAP SPLICE LENGTH SCHEDULE, EXCEPT AS NOTED ON DRAWINGS. MECHANICAL SPLICES NOTED ON THE DRAWINGS SHALL BE DAYTON SUPERIOR BAR-LOCK OR APPROVED WITH A CURRENT ICC-ES OR IAPMO-ES EVALUATION REPORT.

GRADE 60 REINFORCING STEEL LAP SPLICE LENGTH AND DEVELOPMENT LENGTH

BAR SIZE	f'c = 3,000 PSI					f'c = 4,000 PSI					f'c = 5,000 PSI				
	MISC BARS		TOP BARS (SEE NOTE 3)		HOOK BARS	MISC BARS		TOP BARS (SEE NOTE 3)		HOOK BARS	MISC BARS		TOP BARS (SEE NOTE 3)		HOOK BARS
	Ld	LAP	Ld	LAP	Ldh	Ld	LAP	Ld	LAP	Ldh	Ld	LAP	Ld	LAP	Ldh
#3	17	22	22	28	9	15	19	29	25	8	13	17	17	22	7
#4	22	29	29	38	11	19	25	25	33	10	17	23	23	29	9
#5	28	36	36	47	14	24	31	31	41	12	22	28	28	36	11

1. ALL TABULATED VALUES ARE IN INCHES, FOR GRADE 60, UNCOATED REINFORING, NORMAL WEIGHT CONCRETE WITH CLEAR SPACING AND CLEAR COVER GREATER THAN THE BAR DIAMETER.
2. IT SHALL BE PERMITTED TO INTERPOLATE BETWEEN CONCRETE STRENGTHS OR USE THE NEXT LOWER CONCRETE STRENGTH.
3. TOP BARS ARE ANY HORIZ BAR PLACED SUCH THAT MORE THAN 12" OF FRESH CONCRETE IS CAST IN THE MEMBER BELOW THE BAR IN ANY SINGLE POUR. HORIZ WALL BARS ARE CONSIDERED TOP BARS.
4. LAP SPLICES ARE FOR NON-LATERAL LOAD RESISTING ELEMENTS. FOR REBAR LAPS SPLICES AT LATERAL LOAD RESISTING ELEMENTS, REFERENCE PLANS AND ELEVATIONS.
5. Ld = DEVELOPMENT LENGTH IN TENSION OF DEFORMED BAR
   Ldh = DEVELOPMENT LENGTH IN TENSION OF DEFORMED BAR OR DEFORMED WIRE WITH A STANDARD...
   LAP = LAP SPLICE LENGTH OF DEFORMED BAR OR DEFORMED WIRE

REINFORCING STEEL SHALL BE PROTECTED BY PLACING BARS WITH A MINIMUM COVER, UNLESS NOTED OTHERWISE.

REINFORCING STEEL CONCRETE COVER	
USE	CLEAR COVER
CONCRETE CAST AGAINST EARTH	3"
CONCRETE EXPOSED TO WEATHER OR EARTH	1-1/2" (FOR #5 OR SMALLER), 2" (FOR #6 AND LARGER)

PROVIDE DOWELS FROM FOOTINGS TO MATCH ALL VERTICAL WALL, PILASTER AND COLUMN REINFORCING. PROVIDE CORNER BARS TO MATCH HORIZONTAL REINFORCING IN WALLS AND FOOTINGS AT ALL CORNERS AND INTERSECTIONS. CONTINUE HORIZONTAL WALL BARS THROUGH PILASTERS COLUMNS AND INTERSECTING WALLS.

ALL ANCHOR BOLTS, HOLDDOWNS AND OTHER REQUIRED ACCESSORIES SHALL BE SECURED IN PLACE PRIOR TO INSPECTION AND CONCRETE PLACEMENT. DO NOT STAB THE ABOVE LISTED ITEMS INTO FRESH CONCRETE AFTER PLACEMENT. PROPERLY VIBRATE AROUND INSTALLED ITEMS TO ENSURE PROPER CONSOLIDATION OF CONCRETE.

CONCRETE CONNECTORS:
UNLESS A SPECIFIC ANCHOR PRODUCT IS NOTED IN THE DRAWINGS, POST-INSTALLED ANCHORS MAY USE ONE OF THE ANCHORS LISTED BELOW FOR THE REQUIRED TYPE.

POST INSTALLED CONCRETE ANCHORS		
TYPE	PRODUCT	REPORT #
ADHESIVE ANCHORS & DOWELS	SIMPSON SET-XP	ICC-ES ESR-2508
	SIMPSON AT-XP	IAPMO-UES ER-263
	HILTI HIT-HY 200	ICC-ES ESR-3187
SCREW ANCHOR	SIMPSON TITEN HD	ICC-ES ESR-2713
	HILTI KWIK HUS-EZ	ICC-ES ESR-3027

ALL ANCHORS SHALL BE INSTALLED IN STRICT CONFORMANCE WITH THE MANUFACTURER'S RECOMMENDATIONS AND PRODUCT EVALUATION REPORTS.

EMBEDMENTS SPECIFIED ON DRAWINGS ARE "EFFECTIVE" EMBEDMENTS. REFERENCE MANUFACTURER LITERATURE FOR CORRESPONDING ACTUAL EMBEDMENT DEPTHS.

ANCHORS RODS EXPOSED TO EARTH OR WEATHER SHALL BE PROTECTED FROM CORROSION BY HOT-DIP GALVANIZING OR USE OF STAINLESS STEEL. POST INSTALLED EXPANSION AND SCREW ANCHORS EXPOSED TO EARTH OR WEATHER SHALL BE STAINLESS STEEL.

FOR POST-INSTALLED ANCHORS, LOCATE REINFORCEMENT AND CONFIRM FINAL ANCHOR LOCATIONS PRIOR TO FABRICATING PLATES, MEMBERS, OR OTHER STEEL ASSEMBLIES ATTACHED.

IF REINFORCEMENT IS ENCOUNTERED DURING DRILLING, ABANDON AND SHIFT THE HOLE LOCATION TO AVOID THE REINFORCEMENT. PROVIDE A MINIMUM OF (2) ANCHOR DIAMETERS OR 1 INCH, WHICHEVER IS LARGER, OF SOUND CONCRETE BETWEEN THE ANCHOR AND THE ABANDONED HOLE. FILL THE ABANDONED HOLE WITH NON-SHRINK GROUT. IF THE ANCHOR OR DOWEL MANY NOT BE SHIFTED AS NOTED ABOVE, SEEK GUIDANCE FROM THE CONTRACTING OFFICER.

SPECIAL INSPECTION OF ANCHOR INSTALLATION IS REQUIRED UNLESS SPECIFICALLY NOTED OTHERWISE IN DRAWINGS. SEE SPECIAL INSPECTION AND MATERIALS TESTING PROGRAM AND NOTES.

EARTHWORK:

GENERAL:
STABILITY OF CONSTRUCTION EXCAVATION AND WORKER SAFETY ARE THE RESPONSIBILITY OF THE CONTRACTOR. BASED UPON THE GEOTECHNICAL REPORT, TEMPORARY CONSTRUCTION EXCAVATIONS, ABOVE GROUNDWATER, TO BE PLANNED IN ACCORDANCE WITH OSHA PROVISIONS SHOULD ASSUME TYPE B MATERIAL FOR STIFF CLAY, AND TYPE C MATERIAL FOR SAND.

DO NOT EXCAVATE CLOSER THAN 2:1 SLOPE BELOW FOOTING EXCAVATIONS.

PRESCRIPTIVE EARTHWORK:
AT THE OWNERS DIRECTION, A GEOTECHNICAL INVESTIGATION HAS NOT BEEN PERFORMED. IF ANY OF THE FOLLOWING CONDITIONS ARE DISCOVERED DURING CONSTRUCTION AT THE BUILDING SITE, A GEOTECHNICAL INVESTIGATION SHALL BE COMMISSIONED IN ACCORDANCE WITH CHAPTER 18 OF THE INTERNATIONAL BUILDING CODE:
- A. QUESTIONABLE SOIL
- B. EXPANSIVE SOIL
- C. GROUND-WATER TABLE IS ABOVE OR WITHIN 5 FEET BELOW THE ELEVATION OF THE LOWEST FLOOR LEVEL WHERE SUCH FLOOR IS LOCATED BELOW THE FINISHED GROUND LEVEL ADJACENT TO THE FOUNDATION.
- D. ROCK STRATA OF VARIABLE OR DOUBTFUL CHARACTERISTICS
- E. EXCAVATIONS THAT WILL REMOVE THE LATERAL SUPPORT OF AN ADJACENT, EXISTING FOUNDATION
- F. USE OF COMPACTED FILL MATERIAL BELOW SHALLOW FOUNDATIONS IN EXCESS OF 12 INCHES IN DEPTH
- G. USE OF CONTROLLED LOW-STRENGTH MATERIAL (CLSM)

THE SITE WORK DESCRIBED BELOW IS BASED ON RECOMMENDATIONS FROM THE PRESCRIPTIVE REQUIREMENTS IN THE INTERNATIONAL BUILDING CODE CHAPTER 18.
- A. REMOVE ALL ORGANIC MATERIAL AND TOPSOIL FROM AREAS UNDER THE BUILDING OR UNDER PAVED AREAS.
- B. FOUNDATIONS SHALL BE BUILT ON UNDISTURBED SOIL OR COMPACTED FILL MATERIAL 12 INCHES OR LESS IN DEPTH. IF PROVIDED, COMPACTED FILL MATERIAL SHALL BE PLACED IN LIFTS NOT TO EXCEED 8" AND HAVE AN IN-PLACE DRY DENSITY NOT LESS THAN 95 PERCENT OF THE MAXIMUM DRY DENSITY AT OPTIMUM MOISTURE CONTENT DETERMINED IN ACCORDANCE WITH ASTM D1557. IF THE COMPACTED FILL MATERIAL EXCEEDS 12 INCHES IN DEPTH OR CLSM IS USED, PLACEMENT SHALL COMPLY WITH THE PROVISIONS OF AN APPROVED GEOTECHNICAL INVESTIGATION AND REPORT.
- C. THE BOTTOM OF ALL EXTERIOR FOOTINGS AND FOOTINGS SUSCEPTIBLE TO FROST HEAVE SHALL EXTEND A MINIMUM DEPTH BELOW LOWEST ADJACENT FINISHED GRADE OF 42 INCHES.
- D. THE EXCAVATION OUTSIDE THE FOUNDATION SHALL BE BACKFILLED WITH SOIL THAT IS FREE OF ORGANIC MATERIAL, CONSTRUCTION DEBRIS, COBBLES AND BOULDERS, OR WITH CLSM. THE BACKFILL SHALL BE PLACED IN LIFTS AND COMPACTED IN A MANNER THAT DOES NOT DAMAGE THE FOUNDATION OR THE WATERPROOFING OR DAMPPROOFING MATERIAL, IF PRESENT. CLSM NEED NOT BE COMPACTED.
- E. DAMPPROOFING, WATERPROOFING, AND FOUNDATION DRAINS: COMPLY WITH SECTION 1805 OF THE IBC. DESIGN/SPECIFICATION OF THESE SYSTEMS IS TO BE BY OTHERS.

WOOD AND WOOD PRODUCTS:

SAWN LUMBER:
SAWN LUMBER SHALL CONFORM TO THE REQUIREMENTS AS INDICATED IN THE NATIONAL DESIGN SPECIFICATION (NDS) DESIGN VALUES FOR WOOD CONSTRUCTION AND CONFORMING TO THE WEST COAST LUMBER INSPECTION BUREAU OR WESTERN WOOD PRODUCTS ASSOCIATION GRADING RULES OR APPROVED EQUIVALENT. ALL LUMBER SHALL BE MARKED BY THE GRADING AGENCY EXCEPT FOR ARCHITECTURAL/ EXPOSED MEMBERS. A CERTIFICATE OF COMPLIANCE BY THE MANUFACTURER SHALL BE PROVIDED IN LIEU OF MARKING. LUMBER SHALL BE THE SPECIES, AND GRADE NOTED BELOW UNLESS NOTED OTHERWISE ON DRAWINGS:

SAWN LUMBER	
USE	SPECIES AND GRADE
BUCKS, BLOCKING, BRIDGING AND MISCELLANEOUS	DOUGLAS FIR-LARCH OR HEM FIR #3
SILLS, LEDGERS, ETC. IN CONTACT WITH CONCRETE	PRESSURE TREATED HEM FIR #2
HORIZONTAL PLATES, AND HEADERS	KILN DRIED DOUGLAS FIR-LARCH #2 & BETTER
POSTS, COLUMNS (5x AND GREATER)	DOUGLAS FIR-LARCH #1

DIMENSIONAL LUMBER SHALL BE DELIVERED WITH MOISTURE CONTENT LESS THAN 19% AND SURFACED S4S. TIMBERS SHALL BE DELIVERED WITH MOISTURE CONTENT LESS THAN 15%. ALL LUMBER DELIVERED TO THE SITE SHALL BE STACKED OR STORED OFF THE GROUND AND PROPERLY PROTECTED AGAINST WEATHER.

ALL LUMBER IN CONTACT WITH CONCRETE OR MASONRY SHALL BE PRESSURE TREATED, UNLESS AN APPROVED MOISTURE BARRIER IS PROVIDED.

FASTEN BUILT-UP STUDS COLUMNS AND JAMBS WITH (1) ROW OF 10D NAILS AT 6" ON CENTER, STAGGERED, BETWEEN EACH LAMINATION FOR 2x4 STUDS AND (2) ROWS OF 10D NAILS AT 8" ON CENTER, BETWEEN EACH LAMINATION FOR 2x6 STUDS.

ALL NON-BEARING PARTITION WALLS SHALL BE INSTALLED WITH A GAP BETWEEN THE TOP PLATE OF THE WALL AND FLOOR OR ROOF FRAMING. THE PARTITIONS SHALL BE ANCHORED TO THE FRAMING WITH A CONNECTOR THAT BRACES THE WALL WHILE PERMITTING THE FRAMING TO FREELY DEFLECT.

UNLESS NOTED OTHERWISE PROVIDE SOLID SAWN OR BUILT-UP POSTS UNDER BEAMS WITH A MINIMUM WIDTH EQUAL TO THE BEAM WIDTH AND A DEPTH EQUAL TO THE WALL THICKNESS. PROVIDE SIMPSON 'LPC' POST CAP.

GLUED-LAMINATED TIMBER:
GLUED-LAMINATED (GLULAM) MEMBERS SHALL BE FABRICATED IN CONFORMANCE WITH ANSI STANDARD A190.1. EACH MEMBER SHALL BEAR AN IDENTIFICATION MARK OR BE ACCOMPANIED BY A CERTIFICATE OF CONFORMANCE. GLUED-LAMINATED TIMBER SHALL CONFORM TO THE COMBINATION NOTED BELOW:

GLUED-LAMINATED MEMBERS			
USE	COMBINATION SYMBOL	FLEXURAL STRESS Fb (PSI)	MODULUS OF ELASTICITY (PSI)
SIMPLE SPAN BEAMS	24F-V4 (DF/DF)	+2,400 / -1,850	1,800,000
CONTINUOUS AND CANTILEVER BEAMS	24F-V8 (DF/DF)	+/-2,400	1,800,000
COLUMNS AND TRUSS MEMBERS	2-DF-L2	+/-1,300	1,600,000

EXPOSED GLUED-LAMINATED MEMBERS SHALL CONFORM TO AITC, ARCHITECTURAL APPEARANCE GRADE WHILE CONCEALED MEMBERS SHALL CONFORM TO AITC, INDUSTRIAL GRADE. GLUED-LAMINATED MEMBERS THAT ARE OUTSIDE OF A CONDITIONED BUILDING ENVELOPE SHALL UTILIZE WET-USE EXTERIOR WATERPROOF ADHESIVES.

GLUED-LAMINATED MEMBERS SHALL BE MANUFACTURED BETWEEN 3,500 AND 5,000 FOOT STANDARD MILL CAMBER WITH TOLERANCES AS ALLOWED BY ANSI A190. THE DRAWINGS WILL INDICATE WHETHER ADDITIONAL CAMBER IS REQUIRED.

mosaic
architecture-planning-design
317 Cruse Avenue Suite 201
Helena, Montana 59601
406.449.2013
www.mosaicarch.com

PROFESSIONAL ENGINEER LICENSED Eric Heidel P-22358 STATE OF IDAHO ERIC THOMAS HEIDEBRECHT
7/17/2024

FOREST SERVICE U.S. DEPARTMENT OF AGRICULTURE
U.S. DEPARTMENT OF AGRICULTURE
FOREST SERVICE
R-1 NORTHERN REGION

Morrison Maierle
engineers · surveyors · planners · scientists
1 Engineer Place
Helena, MT 59602
406.442.3050
www.m-m.net

COPYRIGHT © MORRISON-MAIERLE, 2022

POWELL DUPLEX RENOVATION

LOCHSA-POWELL RANGER DISTRICT,
192 POWELL RD,
LOLO, ID 59847

CONSTRUCTION DOCUMENTS

MARK	DATE	REVISION

PROJECT NO. 1240L023F0138
DATE: 7/19/2024
Drawn By: SH
Designed By: AY
Checked By: EH

GENERAL STRUCTURAL NOTES

SHEET: **S001**

WOOD AND WOOD PRODUCTS:

WOOD CONNECTIONS:
FRAMING ACCESSORIES SHALL BE MANUFACTURED BY SIMPSON STRONG TIE (OR APPROVED EQUAL) AND OF THE TYPE AND SIZE SHOWN ON THE DRAWINGS. FULLY FASTEN ACCORDING TO MANUFACTURER'S SCHEDULE USING LARGEST SIZE SHOWN AND INSTALL FOLLOWING ALL MANUFACTURES REQUIREMENTS, UNLESS NOTED OTHERWISE.

ALL FRAMING NAILS SHALL BE 'COMMON' NAILS OF THE SIZE AND QUANTITY INDICATED ON THE DRAWINGS. USE OF SMALLER DIAMETER "BOX" NAILS FREQUENTLY USED IN NAIL GUNS REQUIRES USE OF LARGER PENNY WEIGHT TO PROVIDE AN EQUIVALENT DIAMETER/LENGTH NAIL. ALL NAILING SHALL COMPLY WITH IBC FASTENING SCHEDULE PER CHAPTER 23. OBTAIN CONTRACTING OFFICER'S APPROVAL OF ALL PROPRIETARY NAILING SYSTEMS.

BOLTS AND LAG SCREWS SHALL BE ASTM A307 AND CONFORM TO ANSI/ASME STANDARD B18.2.1. ALL BOLTS AND LAG SCREWS BEARING ON WOOD SHALL BE INSTALLED WITH STANDARD CUT WASHERS. BOLT HOLES IN WOOD MEMBERS SHALL NOT EXCEED 1/16" LARGER THAN THE BOLT DIAMETER. AT EXPOSED CONNECTIONS CUT OFF EXTENDED BOLT AND 'KNICK' THREADS TO PRECLUDE LOOSENING. LAG SCREWS HOLE CLEARANCE SHALL BE THE SAME DIAMETER AS THE SHANK AND THE SAME DEPTH AS THE UNTHREADED SHANK. THE LEAD HOLE SHALL BE 60 PERCENT OF THE SHANK DIAMETER AND A LENGTH EQUAL TO THE THREADED PORTION.

ANCHOR RODS SHALL CONFORM TO ASTM F1554, GRADE 36 UNLESS NOTED OTHERWISE. ANCHOR RODS TO BE WELDED SHALL CONFORM TO ASTM F1554, GRADE 55. THREADED RODS SHALL CONFORM TO ASTM A36 UNLESS NOTED OTHERWISE.

CUTTING AND NOTCHING OF JOISTS AND STUDS SHALL CONFORM TO THE TYPICAL WOOD DETAILS PROVIDED.

STEEL CONNECTION PLATE MATERIAL SHALL CONFORM TO ASTM A36. WELDING SHALL CONFORM TO AWS D1.1.

PROVIDE SHEAR PLATES OF THE SIZE AND MATERIAL INDICATED. SHEAR PLATE DIMENSIONS, GROOVES, DAPS, AND BOLT HOLES SHALL CONFORM TO APPENDIX K OF THE NATIONAL DESIGN SPECIFICATION FOR WOOD CONSTRUCTION (NDS). PRESSED STEEL TYPE CONNECTORS ARE TO BE MANUFACTURED FROM SAE 1010 HOT ROLLED CARBON STEEL. MALLEABLE IRON SHEAR PLATES ARE TO BE MANUFACTURED WITH ASTM A47 GRADE 32510 MATERIAL.

CONFIRM REQUIRED CORROSION PROTECTION FOR HARDWARE AND FASTENERS WITH SPECIFIC RECOMMENDATIONS FROM PRESSURE TREATING MANUFACTURER OR HANGER MANUFACTURER (USE MOST CONSERVATIVE) FOR SPECIFIC WOOD TREATMENTS USED. MINIMUM CORROSION PROTECTION ON METAL CONNECTORS EXPOSED TO THE ENVIRONMENT OR PRESSURE TREATED LUMBER TO BE PER ASTM A653 CLASS 185 (SIMPSON ZMAX) OR ASTM A123. FINISH FOR EXPOSED CONNECTION HARDWARE SHALL BE EPOXY-BASED CORROSION RESISTANT PAINT WITH COLOR AS CHOSEN BY ARCHITECT.

FASTENERS FOR PRESSURE TREATED LUMBER MUST BE HOT-DIP GALVANIZED, STAINLESS STEEL, SILICON BRONZE OR COPPER. HOT-DIP GALVANIZED HARDWARE AND FASTENERS MUST COMPLY WITH ASTM A153, STAINLESS STEEL FASTENERS TO BE TYPE 304 OR TYPE 316. HARDWARE AND FASTENERS USED TOGETHER MUST BE THE SAME TYPE (E.G. HOT-DIP GALVANIZED NAILS WITH HOT-DIP GALVANIZED HANGERS).

WOOD STRUCTURAL PANELS:
WOOD STRUCTURAL PANELS SHALL BE IN ACCORDANCE PS 1, STRUCTURAL PLYWOOD, AND/OR PS 2, PERFORMANCE STANDARD FOR WOOD-BASED STRUCTURAL-USE PANELS. ALL WOOD STRUCTURAL PANELS SHALL BE APA RATED SHEATHING, EXPOSURE 1 PLYWOOD OR OSB, WITH SPAN RATINGS, THICKNESS & NAILING FOR SHEATHING AS SHOWN ON THE DRAWINGS. PANELS SHALL BE STAMPED WITH THE APA TRADEMARK.

ALL SHEATHING DELIVERED TO THE SITE SHALL BE STACKED OR STORED OFF THE GROUND AND PROPERLY PROTECTED AGAINST WEATHER.

WOOD STRUCTURAL PANEL INSTALLATION SHALL BE IN CONFORMANCE WITH APA RECOMMENDATIONS. ALLOW 1/8" SPACING AT PANEL ENDS AND EDGES, UNLESS OTHERWISE RECOMMENDED BY THE PANEL MANUFACTURER.

ALL ROOF SHEATHING SHALL BE INSTALLED WITH FACE GRAIN OR STRENGTH AXIS PERPENDICULAR TO SUPPORTS AND STAGGERED 48", EXCEPT AS INDICATED ON THE DRAWINGS. ROOF SHEATHING SHALL EITHER BE BLOCKED, TONGUE-AND-GROOVE, OR HAVE EDGES SUPPORTED BY PLYCLIPS. WHERE BLOCKING IS SPECIFICALLY INDICATED ON THE DRAWINGS, T&G EDGES OR PLYCLIPS MAY NOT BE SUBSTITUTED. SHEATHING SHALL BE UNBLOCKED, EXCEPT AS INDICATED ON DRAWINGS. ROOF SHEATHING SHALL HAVE 8D FASTENERS AT 6" ON CENTER AT PANEL EDGES AND 12" ON CENTER IN THE FIELD.

SHEAR WALL SHEATHING SHALL BE INSTALLED EITHER HORIZONTALLY OR VERTICALLY AND BE BLOCKED AT ALL PANEL EDGES. NO INDIVIDUAL PIECE OF SHEATHING SHALL BE SMALLER THAN 2'-0" x 2'-0".

DRIVE SHEATHING NAILS (OR OTHER SPECIFIED ATTACHMENTS) FLUSH WITH BUT NOT FRACTURING, THE WOOD PANEL SURFACE.

STRUCTURAL INSULATED PANELS:
PROVIDE "R-CONTROL" BY AFM CORP. OR EQUIVALENT APPROVED BY THE STRUCTURAL ENGINEER OF RECORD CONSISTING OF LAMINATED COMPOSITES OF APPROVED ORIENTED STRAND BOARD (OSB) AND EXPANDED POLYSTYRENE (EPS) INSULATION, WITH MANUFACTURER SUPPLIED CONNECTING SPLINES AND APPROVED FASTENERS.

SUBMIT SHOP DRAWINGS SHOWING LAYOUT, PROFILES, PRODUCT COMPONENTS AND ACCESSORIES. STRUCTURAL INSULATED PANELS SHALL BE OF THE SIZE AND TYPE SHOWN ON THE DRAWINGS.

MANUFACTURE, FABRICATE AND INSTALL PANELS TO MAINTAIN THE WARRANTIED PERFORMANCE CRITERIA ESTABLISHED BY THE MANUFACTURER WITHOUT DEFECTS, DAMAGE, OR FAILURE. COMPLY WITH ALL QUALITY ASSURANCE, PRODUCT HANDLING, AND STORAGE PROCEDURES SPECIFIED BY THE PANEL MANUFACTURER. STRUCTURAL PANEL MANUFACTURER SHALL SUBMIT THEIR STANDARD WARRANTY DOCUMENTS FOR REVIEW AND APPROVAL BY THE CONTRACTING OFFICER.

CONFIRM ALL DIMENSIONS, OUTLINES, ELEVATIONS, AND DETAILS WITH ARCHITECTURAL DRAWINGS AND EXISTING CONDITIONS/DIMENSIONS. COORDINATE ALL PENETRATIONS / CHASES WITH ARCHITECTURAL, MECHANICAL, ELECTRICAL AND PLUMBING DRAWINGS. AFFIX AUTHORIZED LABEL TO ALL MEMBERS SUPPLIED. ALSO IDENTIFY EACH MEMBER WITH MARK NUMBER.

STRUCTURAL INSULATED PANEL MANUFACTURER TO INSPECT ALL PANELS AND PANEL ACCESSORIES AFTER THEY HAVE BEEN ERECTED AND FLOOR AND/OR ROOF MEMBERS, CONNECTORS, BRIDGING, BLOCKING, ETC., HAS BEEN INSTALLED. MANUFACTURER TO SUBMIT CERTIFICATE TO THE CONTRACTING OFFICER THAT THE INSPECTION WAS MADE AND THAT PANELS AND PANEL ACCESSORIES ARE IN ACCEPTABLE CONDITION AND MEET THE MANUFACTURER'S INSTALLATION REQUIREMENTS.

SYMBOL/ANNOTATION	DESCRIPTION	SYMBOL/ANNOTATION	DESCRIPTION
F# XX'-XX"	CONCRETE CONTINUOUS FOOTING MARK (SEE SCHEDULE)	1 S4.1	ELEVATION CALLOUT
C#	CONCRETE WALL MARK (SEE SCHEDULE)	1 S4.1	SECTION CALLOUT
S#	SIP SHEARWALL MARK (SEE SCHEDULE)	TOF = 97' - 0"	COMPONENT ELEVATION
	EARTH/SOIL HATCH		SLAB/DECK/WALL OPENING
	GRANULAR FILL/GRAVEL HATCH		SAWN LUMBER COLUMN
	CONCRETE HATCH		GLULAM BEAM
	GROUT HATCH		WOOD BLOCKING
	WOOD STRUCTURAL PANEL HATCH		SIP SHEAR WALL (GRAY HATCH)
	SIP WALL HATCH		SIP BEARING WALL BELOW
	RIGID INSULATION HATCH		NONSTRUCTURAL PARTITION WALL EXTENDING TO FLOOR ABOVE
	NORTH ARROW	PLS	WOOD TOP PLATE ELEVATION STEP
1 S5.1	DETAIL CALLOUT (90 DEGREE ORIENTATION TO CURRENT VIEW) VIEW ORIENTED TOWARD ARROW		SIP ROOF PANEL
2 S5.1	DETAIL CALLOUT (MATCHES ORIENTATION OF CURRENT VIEW) ENLARGED VIEW		

SYMBOLS & ANNOTATIONS

ABV	ABOVE	J	JOIST
ADDL	ADDITIONAL		
AA	ADHESIVE ANCHOR	LAM	LAMINATED
AD	ADHESIVE DOWEL	LVL	LAMINATED VENEER LUMBER
ALT	ALTERNATE	LF	LINEAR FEET
ACI	AMERICAN CONCRETE INSTITUTE	LL	LIVE LOAD
AISC	AMERICAN INSTITUTE OF STEEL CONSTRUCTION	LLH	LONG LEG HORIZONTAL
		LLV	LONG LEG VERTICAL
ANSI	AMERICAN NATIONAL STANDARDS INSTITUTE	MFR	MANUFACTURER
APA	AMERICAN PLYWOOD ASSOCIATION	M	MASONRY
ASCE	AMERICAN SOCIETY OF CIVIL ENGINEERS	ML	MASONRY LINTEL
		MP	MASONRY PIER
ASTM	AMERICAN SOCIETY OF TESTING AND MATERIALS	MATL	MATERIAL
		MAX	MAXIMUM
AB	ANCHOR BOLT	MECH	MECHANICAL
AR	ANCHOR ROD	MBR	MEMBER
L	ANGLE	MTL	METAL
ARCH	ARCHITECT	MD	METAL DECK
		MEZZ	MEZZANINE
B PL	BASE PLATE	MIN	MINIMUM
BSMT	BASEMENT	MISC	MISCELLANEOUS
BM	BEAM		
BRG	BEARING	NLB	NONLOAD BEARING
BLW	BELOW	N	NORTH
BTWN	BETWEEN	NA	NOT APPLICABLE
BLKG	BLOCKING	NTS	NOT TO SCALE
BOT	BOTTOM	NO	NUMBER
BC	BOTTOM CHORD		
BLDG	BUILDING	OC	ON CENTER
BU	BUILT UP	OPNG	OPENING
		OWJ	OPEN WEB JOIST
CANTIL	CANTILEVER	OPP	OPPOSITE
CB	CARRIAGE BOLT		
CIP	CAST IN PLACE	PAR	PARALLEL
CTR	CENTER	PERP	PERPENDICULAR
CTRD	CENTERED	PREFAB	PREFABRICATE
CL	CENTERLINE	PH	PHASE
C	CHANNEL	PC	PIER CAP/CONCRETE PILE
CLR	CLEAR	PL	PLATE
CFMF	COLD FORMED METAL FRAMING	PLYWD	PLYWOOD
COL	COLUMN	LBS	POUND
CONC	CONCRETE	PLF	POUNDS PER LINEAR FOOT
CC	CONCRETE COLUMN	PSF	POUNDS PER SQUARE FOOT
CMU	CONCRETE MASONRY UNIT	PSI	POUNDS PER SQUARE INCH
CONN	CONNECTION	PAF	POWER-ACTUATED FASTENERS
CD	CONSTRUCTION DOCUMENTS	PT	PRESSURE TREATED
CJ	CONSTRUCTION JOINT		
CONT	CONTINUOUS/ CONTINUED	QA	QUALITY ASSURANCE
CF	CONTINUOUS CONCRETE FOOTING		
CONTR	CONTRACTOR	R	RADIUS
CO	CONTRACTING OFFICER	REF	REFERENCE
CJ	CONTROL JOINT	REINF	REINFORCE, REINFORCING
COORD	COORDINATE	REBAR	REINFORCING STEEL BARS
X BRACE	CROSS BRACE	REQT	REQUIREMENT
		REV	REVISION
D	PENNY (NAIL) OR DEPTH	RT	RIGHT
DL	DEAD LOAD	RGD INS	RIGID INSULATION
DEG	DEGREE	RD	ROUND
DEMO	DEMOLITION		
DET	DETAIL	SCHED	SCHEDULE
DIM	DIMENSION	SA	SCREW ANCHOR
DIST	DISTANCE	SHTHG	SHEATHING
DOUG FIR	DOUGLAS FIR	SIM	SIMILAR
DWL	DOWEL	SCJ	SLAB CONTRACTION JOINT
DWG	DRAWING	SQ	SQUARE
		SF	SQUARE FEET
EA	EACH	SI	SQUARE INCH
EW	EACH WAY	SPEC	SPECIFICATION
ELEV	ELEVATOR	STD	STANDARD
ENGR	ENGINEER	STL	STEEL
EQ	EQUAL/ EQUALLY	SD	STEEL DECK
EQUIP	EQUIPMENT	STL JST	STEEL JOIST
EXST	EXISTING	STIF	STIFFENER
EXP	EXPANSION	STRUCT	STRUCTURAL
EXP BT	EXPANSION BOLT	SIP	STRUCTURAL INSULATED PANEL
EXT	EXTERIOR	SUB FLR	SUBFLOOR
		SUB	SUBSTITUTE
FO	FACE OF		
FSTNR	FASTENER	KIP	THOUSAND POUNDS
FT	FEET	TB	THROUGH BOLT
FLR	FLOOR	TMBR	TIMBER
FDTN	FOUNDATION	T&G	TONGUE AND GROOVE
FTG	FOOTING	T&B	TOP AND BOTTOM
FS	FOOTING STEP	TOB	TOP OF BEAM
		TOC	TOP OF CONCRETE
GALV	GALVANIZED	TOD	TOP OF DECK/SHEATHING
GA	GAUGE	TOF	TOP OF FOOTING
GC	GENERAL CONTRACTOR	TOM	TOP OF MASONRY
GL	GLUE LAMINATED	TOS	TOP OF STEEL
GLB	GLUE LAMINATED BEAM	TOW	TOP OF WALL
GR	GRADE	TJI	TRUSS JOIST
GR BM	GRADE BEAM	TYP	TYPICAL
GT	GROUT		
GYP	GYPSUM	UNO	UNLESS NOTED OTHERWISE
HGR	HANGER	VIF	VERIFY IN FIELD
HSA	HEADED STUD ANCHOR	VERT	VERTICAL
HDR	HEADER		
HT	HEIGHT	WLD	WELD/WELDED
H	HIGH	WWF	WELDED WIRE FABRIC
HD	HOLD-DOWN	W	WIDE
HSS	HOLLOW STRUCTURAL SECTION	WF	WIDE FLANGE
HK	HOOK	WL	WIND LOAD
HORIZ	HORIZONTAL	W/	WITH
		W/O	WITHOUT
INFO	INFORMATION	WD	WOOD
INT	INTERIOR	HG	WOOD BEAM HANGER
IBC	INTERNATIONAL BUILDING CODE	WSP	WOOD STRUCTURAL PANEL
		WP	WORKING POINT

STRUCTURAL ABBREVIATIONS

mosaic
architecture-planning-design
317 Cruse Avenue Suite 201
Helena, Montana 59601
406.449.2013
www.mosaicarch.com

PROFESSIONAL ENGINEER LICENSED Eric Heidel P-22358 STATE OF IDAHO ERIC THOMAS HEIDEBRECHT 7/17/2024

FOREST SERVICE U.S. DEPARTMENT OF AGRICULTURE

U.S. DEPARTMENT OF AGRICULTURE
FOREST SERVICE
R-1 NORTHERN REGION

Morrison Maierle
engineers · surveyors · planners · scientists
1 Engineer Place
Helena, MT 59602
406.442.3050
www.m-m.net

COPYRIGHT © MORRISON-MAIERLE, 2022

POWELL DUPLEX RENOVATION

LOCHSA-POWELL RANGER DISTRICT,
192 POWELL RD,
LOLO, ID 59847

CONSTRUCTION DOCUMENTS


MARK	DATE	REVISION

PROJECT NO. 1240LU23F0138
DATE: 7/19/2024
Drawn By: SH
Designed By: AY
Checked By: EH

GENERAL STRUCTURAL NOTES, ANNOTATIONS AND SYMBOLS & ABBREVIATIONS

SHEET: **S002**

DATESTAMP 7/02/2024 2:41:06 PM

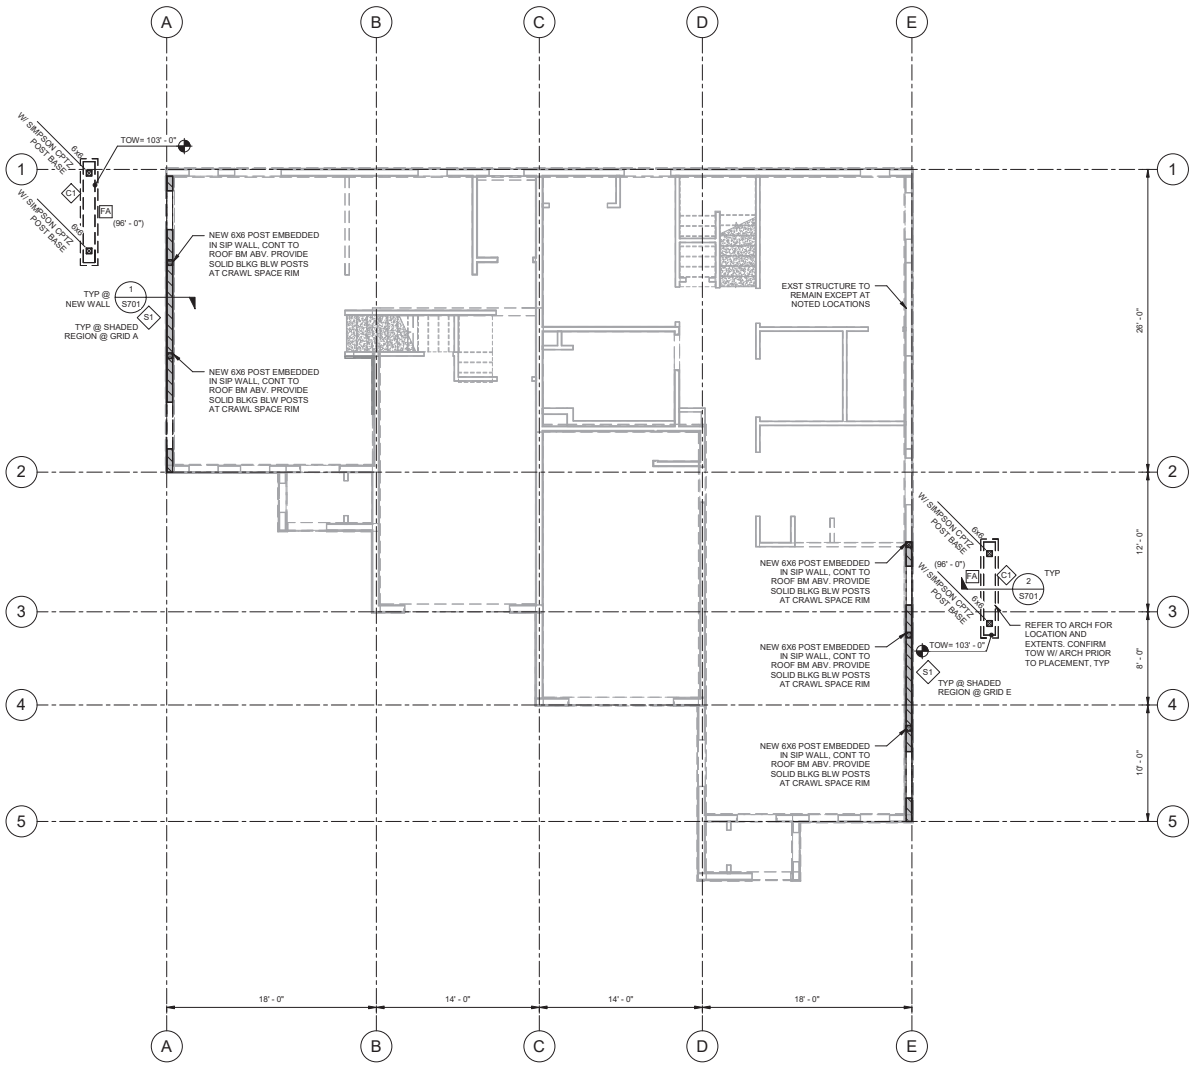

1 MAIN FLOOR STRUCTURAL PLAN
3/16" = 1'-0"

PLAN NOTES

1. PROJECT DATUM ELEVATION = 100' - 0" AT TOP OF MAIN LEVEL FLOOR SHEATHING (SEE CIVIL DRAWINGS FOR ABSOLUTE ELEVATION). ALL SPOT ELEVATIONS ARE IN REFERENCE TO THE DATUM ELEVATION.
2. REFER TO THE GENERAL NOTES FOR ADDITIONAL REQUIREMENTS.
3. REFER TO THE DRAWING ANNOTATIONS & SYMBOLS FOR EXPLANATION OF DRAWING CONVENTIONS.
4. REFER TO S701 FOR TYPICAL DETAILS. TYPICAL DETAILS ARE NOT NECESSARILY REFERENCED BY CALLOUTS ON PLAN; IT IS THE CONTRACTOR'S RESPONSIBILITY TO FOLLOW THE REQUIREMENTS OF THE DETAILS AT THE LOCATION AT WHICH THEY OCCUR.
5. COORDINATE THE FOLLOWING ITEMS WITH DRAWINGS OF OTHER DISCIPLINES:
   - SUBGRADE PREPARATION REQUIREMENTS BELOW FOOTINGS AND SLABS ON GRADE AND BACKFILL REQUIREMENTS BEHIND BASEMENT AND RETAINING WALLS; SEE THE PRESCRIPTIVE EARTHWORK SECTION OF THE GENERAL STRUCTURAL NOTES.
   - SIZES AND LOCATIONS OF OPENINGS AND PENETRATIONS THROUGH WALLS AND FLOORS; SEE ARCHITECTURAL, ELECTRICAL, MECHANICAL, AND PLUMBING DRAWINGS.
   - EXTERIOR CONCRETE, INCLUDING SLABS AND SITE RETAINING WALLS; SEE ARCHITECTURAL, CIVIL, AND LANDSCAPE DRAWINGS.
   - LOCATIONS AND REQUIREMENTS FOR NON-BEARING / NON-STRUCTURAL PARTITION WALLS; SEE ARCHITECTURAL DRAWINGS.
   - LOCATION, SIZE, AND ANCHORAGE OF ELECTRICAL MECHANICAL, AND PLUMBING EQUIPMENT; SEE ELECTRICAL, MECHANICAL, AND PLUMBING DRAWINGS.
6. EXTERIOR GRIDLINES ARE ALIGNED TO THE FACE OF FOUNDATION WALL AND INTERIOR GRIDLINES ARE ALIGNED TO THE CENTER OF COLUMN OR WALL, UNLESS NOTED OTHERWISE.
7. PROVIDE NEW SOLID BLOCKING THROUGH RIM JOIST SPACE BELOW POSTS OR BUILT-UP STUDS.

CONTINUOUS FOOTINGS - SCHEDULE

MARK	WIDTH	THICKNESS	LONG REINF
FA	1' - 6"	10"	(2) #4

CONCRETE WALLS - SCHEDULE

MARK	THICKNESS	HORIZ REINF	VERT REINF
C1	1' - 0"	#4 @ 16" OC EF	#4 @16" OC DOWELS EF

SHEATHED SHEARWALL - SCHEDULE

MARK	PANEL SIZE	SHEAR PANEL ATTACHMENT	FRMG AT PANEL EDGES	SILL PLATE NAILING
S1	6 1/2" SIP	8d BOX NAIL @ 6" OC	SURFACE BLOCK SPLINE	(3) 16d @ EA JOIST (16" OC)

mosaic
architecture-planning-design
317 Cruse Avenue Suite 201
Helena, Montana 59601
406.449.2013
www.mosaicarch.com

PROFESSIONAL ENGINEER LICENSED Eric Heidel P-22358 STATE OF IDAHO ERIC THOMAS HEIDEBRECHT 7/17/2024

FOREST SERVICE U.S. DEPARTMENT OF AGRICULTURE

U.S. DEPARTMENT OF AGRICULTURE
FOREST SERVICE
R-1 NORTHERN REGION

Morrison Maierle
engineers · surveyors · planners · scientists
1 Engineer Place
Helena, MT 59602
406.442.3050
www.m-m.net

COPYRIGHT © MORRISON-MAIERLE, 2022

POWELL DUPLEX RENOVATION

LOCHSA-POWELL RANGER DISTRICT,
192 POWELL RD,
LOLO, ID 59847

CONSTRUCTION DOCUMENTS


MARK	DATE	REVISION

PROJECT NO. 1240LU23F0138
DATE: 7/19/2024
Drawn By: SH
Designed By: AY
Checked By: EH

FOUNDATION/MAIN FLOOR STRUCTURAL PLAN

SHEET: **S101**

DATESTAMP 7/17/2024 2:44:07 PM

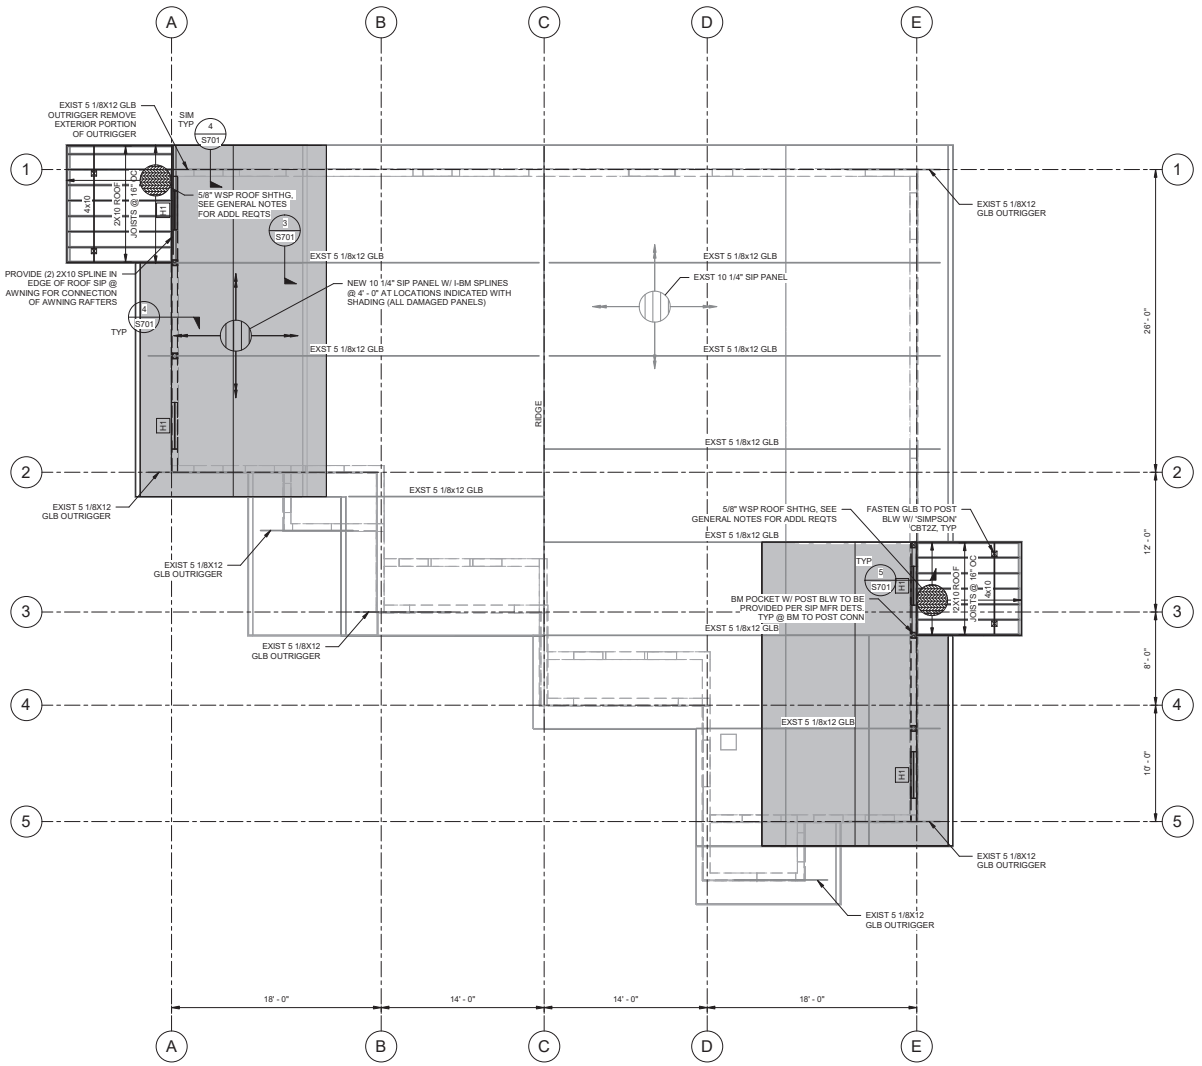

1 ROOF STRUCTURAL PLAN
3/16" = 1'-0"

PLAN NOTES

1. PROJECT DATUM ELEVATION = 100' - 0" AT TOP OF MAIN LEVEL FLOOR SHEATHING (SEE CIVIL DRAWINGS FOR ABSOLUTE ELEVATION). ALL SPOT ELEVATIONS ARE IN REFERENCE TO THE DATUM ELEVATION.
2. REFER TO THE GENERAL NOTES FOR ADDITIONAL REQUIREMENTS.
3. REFER TO THE DRAWING ANNOTATIONS & SYMBOLS FOR EXPLANATION OF DRAWING CONVENTIONS.
4. REFER TO S701 FOR TYPICAL DETAILS. TYPICAL DETAILS ARE NOT NECESSARILY REFERENCED BY CALLOUTS ON PLAN; IT IS THE CONTRACTOR'S RESPONSIBILITY TO FOLLOW THE REQUIREMENTS OF THE DETAILS AT THE LOCATION AT WHICH THEY OCCUR.
5. COORDINATE THE FOLLOWING ITEMS WITH DRAWINGS OF OTHER DISCIPLINES:
   - SIZES AND LOCATIONS OF OPENINGS AND PENETRATIONS THROUGH WALLS AND FLOORS; SEE ARCHITECTURAL, ELECTRICAL, MECHANICAL, AND PLUMBING DRAWINGS.
   - WINDOW AND DOOR LOCATIONS AND ROUGH OPENING SIZES IN WALLS; SEE ARCHITECTURAL DRAWINGS.
   - LOCATION, SIZE, AND ANCHORAGE OF ELECTRICAL MECHANICAL, AND PLUMBING EQUIPMENT; SEE ELECTRICAL, MECHANICAL, AND PLUMBING DRAWINGS.
6. CONTRACTOR TO REPLACE ANYJALL ROOF BEAMS EXHIBITING DAMAGE OR DEGRADATION DUE TO WATER INFILTRATION IN KIND.
7. CONTACT THE STRUCTURAL ENGINEER OF RECORD IF ANY DAMAGE OR DEGRADATION OUTSIDE OF THAT INDENTIFIED ON PLAN IS DISCOVERED DURING CONSTRUCTION/DEMOLITION.

HEADER SCHEDULE

MARK	HEADER SIZE	TRIMMER STUD	KING STUD	KING STUD TO HEADER ATTACHMENT
H1	12" SIP HDR	PER MFR	PER MFR	PER MFR

NOTES:
1. SEE ARCHITECTURAL PLANS FOR OPENING LOCATIONS AND SIZES.
2. SEE GENERAL STRUCTURAL NOTES AND MANUFACTURER TYPICAL DETAILS FOR ADDITIONAL REQUIREMENTS.
3. PROVIDE INSULATION IN HEADER PER ARCHITECTURAL DRAWINGS AND MANUFACTURER.

mosaic
architecture-planning-design
317 Cruse Avenue Suite 201
Helena, Montana 59601
406.449.2013
www.mosaicarch.com

PROFESSIONAL ENGINEER LICENSED Eric Heidel P-22358 STATE OF IDAHO ERIC THOMAS HEIDEBRECHT
7/17/2024

FOREST SERVICE U.S. DEPARTMENT OF AGRICULTURE

U.S. DEPARTMENT OF AGRICULTURE
FOREST SERVICE
R-1 NORTHERN REGION

Morrison Maierle
engineers · surveyors · planners · scientists
1 Engineer Place
Helena, MT 59602
406.442.3050
www.m-m.net

COPYRIGHT © MORRISON-MAIERLE, 2022

POWELL DUPLEX RENOVATION

LOCHSA-POWELL RANGER DISTRICT,
192 POWELL RD,
LOLO, ID 59847

CONSTRUCTION DOCUMENTS


MARK	DATE	REVISION

PROJECT NO. 1240L023F0138
DATE: 7/19/2024
Drawn By: SH
Designed By: AY
Checked By: EH


ROOF STRUCTURAL PLAN

SHEET: S102


DATESTAMP 7/02/2024 2:44:07 PM

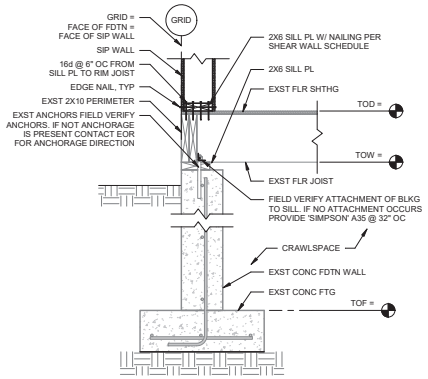


1 EXT WALL TO CONC STEM WALL
1" = 1'-0"

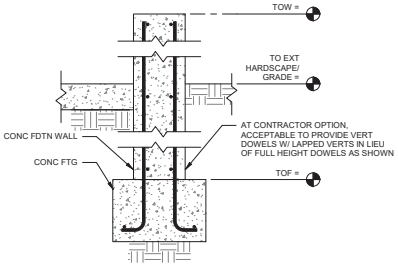


2 EXT AWNING FDTN TO FTG
1" = 1'-0"

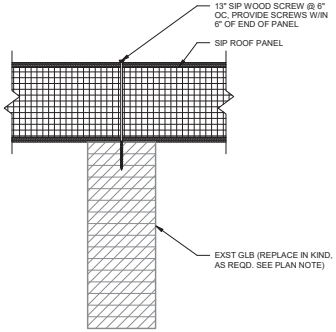

3 TYP SIP ROOF TO GLB
1 1/2" = 1'-0"

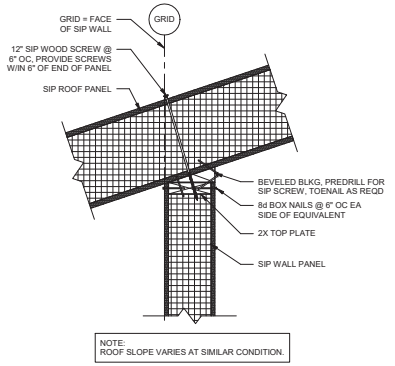

4 TYP SIP ROOF TO SIP WALL
1 1/2" = 1'-0"

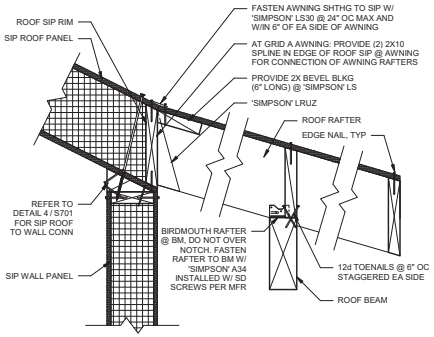

5 NEW AWNING TO ROOF/BM
1 1/2" = 1'-0"

DATESTAMP 7/02/2024 2:44:08 PM

mosaic
architecture-planning-design
317 Cruse Avenue Suite 201
Helena, Montana 59601
406.449.2013
www.mosaicarch.com

PROFESSIONAL ENGINEER LICENSED Eric Heidel P-22358 STATE OF IDAHO ERIC THOMAS HEIDEBRECHT
7/17/2024

FOREST SERVICE U.S. DEPARTMENT OF AGRICULTURE

U.S. DEPARTMENT OF
AGRICULTURE
FOREST SERVICE
R-1 NORTHERN
REGION

Morrison Maierle
engineers · surveyors · planners · scientists
1 Engineer Place
Helena, MT 59602
406.442.3050
www.m-m.net

COPYRIGHT © MORRISON-MAIERLE, 2022

POWELL DUPLEX RENOVATION

LOCHSA-POWELL RANGER DISTRICT,
192 POWELL RD,
LOLO, ID 59847

CONSTRUCTION DOCUMENTS

MARK	DATE	REVISION

PROJECT NO. 1240LU23F0138
DATE: 7/19/2024
Drawn By: SH
Designed By: AY
Checked By: EH

TYPICAL DETAILS

SHEET: **S701**

ABBREVIATIONS

ACC	AIR COOLED CONDENSER
ACU	AIR CONDITIONING UNIT
AD	ACCESS DOOR
ADJ	ADJUSTABLE
AF	AIR FOIL
AFF	ABOVE FINISHED FLOOR
AFG	ABOVE FINISHED GRADE
AFR	ABOVE FINISHED ROOF
AFS	AIR FLOW STATION
AHU	AIR HANDLING UNIT
AP	ACCESS PANEL
ATC	AUTOMATIC TEMPERATURE CONTROL
ATM	ATMOSPHERE
AWG	AMERICAN WIRE GAUGE
B	BOILER
BB	BASEBOARD
BC	BACKWARD CURVED
BD	BACKDRAFT DAMPER
BF	BOILER FEED
BHP	BRAKE HORSEPOWER
BI	BACKWARD INCLINED
BMS	BUILDING MANAGEMENT SYSTEM
BOD	BOTTOM OF DUCT
BOJ	BOTTOM OF JOIST
BOS	BOTTOM OF STEEL
BTU	BRITISH THERMAL UNIT
C	COMMON
CAV	CONSTANT AIR VOLUME
CC	COOLING COIL
CCW	COUNTER CLOCKWISE
CFM	CUBIC FEET PER MINUTE
CH	CHILLER
C&I	CONTROLS & INSTRUMENTATION
CLG	CEILING
CMU	CONCRETE MASONRY UNIT
CND	CONDENSATE
CONT	CONTINUATION
CORR	CORRIDOR
CT	COOLING TOWER
CU	CONDENSING UNIT
CH	CABINET HEATER
CV	CONTROL VALVE
CVS	CONTROL VALVE STATION
CW	CLOCKWISE
dB	DECIBEL
DB	DRY BULB TEMPERATURE (°F)
DDC	DIRECT DIGITAL CONTROL
DH	DUCT HEATER
DP	DEW POINT TEMPERATURE (°F)
DX	DIRECT EXPANSION
E	EXHAUST
EA	EXHAUST AIR
EAT	ENTERING AIR TEMPERATURE (°F)
EC	ELECTRICAL CONTRACTOR
EDR	EQUIVALENT DIRECT RADIATION
EER	ENERGY EFFICIENCY RATIO
EF	EXHAUST FAN
EFF	EFFICIENCY
EH	ELECTRIC HEATER
ELEV	ELEVATION
ERV	ENERGY RECOVERY VENTILATOR
ESP	EXTERNAL STATIC PRESSURE
ET	EXPANSION TANK
EWH	ELECTRIC WALL HEATER
EWT	ENTERING WATER TEMPERATURE (°F)
F&T	FLOAT & THERMOSTATIC
FC	FORWARD CURVED
FC	FAN COIL
FP	FIRE PROTECTION
FPM	FEET PER MINUTE
FT	FEET
GA	GAUGE OR GAGE
GC	GENERAL CONTRACTOR
GEN	GENERATOR
GH	GRAVITY HOOD
GPD	GALLONS PER DAY
GPH	GALLONS PER HOUR
GPM	GALLONS PER MINUTE
H	HUMIDIFIER
HC	HEATING COIL
HOA	HAND-OFF-AUTOMATIC
HP	HORSEPOWER
HR	HOUR
HEX	HEAT EXCHANGER
ID	INSIDE DIAMETER
IFB	INTEGRAL FACE & BYPASS
IGV	INLET GUIDE VANES
IPS	IRON PIPE SIZE
IU	INDUCTION UNIT
KW	KILOWATTS
KWH	KILOWATT HOUR
LAT	LEAVING AIR TEMPERATURE (°F)
LF	LINEAR FEET
LWT	LEAVING WATER TEMPERATURE (°F)
M	MOTOR OPERATED
MAU	MAKEUP AIR UNIT
MB	MIXING BOX
MBH	1000 BTU/HR
MC	MECHANICAL CONTRACTOR
MFR	MANUFACTURER
MS	MINI-SPLIT
NC	NOISE CRITERIA
NC	NORMALLY CLOSED
NIC	NOT IN CONTRACT
NO	NORMALLY OPEN
NPS	NOMINAL PIPE SIZE
OA	OUTSIDE AIR
OAD	OUTSIDE AIR DAMPER
OBD	OPPOSED BLADE DAMPER
P	PUMP
PC	PLUMBING CONTRACTOR
PD	PRESSURE DROP
PH	PHASE
PHC	PREHEAT COIL
PPM	PART PER MILLION
PROP	PROPELLER
PRV	PRESSURE REDUCING VALVE
PSIA	PSI, ABSOLUTE
PSIG	PSI, GAUGE
QTY	QUANTITY
R	REGISTER
RA	RETURN AIR
RD	RADIAL DAMPER
RF	RETURN/RELIEF AIR FAN
RH	RELATIVE HUMIDITY
RHC	REHEAT COIL
SA	SUPPLY AIR
SAF	SUPPLY AIR FAN
SC	SENSIBLE COOLER
SCFM	CFM, STANDARD CONDITIONS
SD	SMOKE DETECTOR
SEER	SEASONAL ENERGY EFFICIENCY RATIO
SENS	SENSIBLE
SP	STATIC PRESSURE
SPS	STATIC PRESSURE SENSOR
SS	STAINLESS STEEL
T	THERMOSTAT
TA	TRANSFER AIR
TCC	TEMPERATURE CONTROL CONTRACTOR
TCP	TEMPERATURE CONTROL PANEL
TF	TRANSFER FAN
TG	TRANSFER GRILL
TOD	TOP OF DUCT
TOP	TOP OF PIPE
TOS	TOP OF STEEL
TSP	TOTAL STATIC PRESSURE
TYP	TYPICAL
UH	UNIT HEATER
UNC	UNDERCUT
UV	UNIT VENTILATOR
VA	VOLT-AMPERE
VAV	VARIABLE AIR VOLUME
VD	VOLUME DAMPER
VEL	VELOCITY
VFD	VARIABLE FREQUENCY DRIVE
VRF	VARIABLE REFRIGERANT FLOW
WB	WET BULB TEMPERATURE (°F)
WC	WATER COLUMN
WG	WATER GAUGE
WSHP	WATER SOURCE HEAT PUMP
ΔT	TEMPERATURE DIFFERENCE (°F)

MECHANICAL LEGEND

ANNOTATION SYMBOLS

- 3D VIEW NUMBER / SHEET NUMBER
- DETAIL NUMBER / SHEET NUMBER
- SECTION NUMBER / SHEET NUMBER
- AIR DEVICE MARK AND CFM
- AIR DEVICE MARK AND CFM - PROVIDE OPPOSED BLADE DAMPER
- AIR DEVICE MARK AND CFM - PROVIDE RADIAL DAMPER
- ME-# — MECHANICAL EQUIPMENT MARK
- (E) ME-# — EXISTING MECHANICAL EQUIPMENT
- (D) ME-# — DEMOLISHED MECHANICAL EQUIPMENT
- POINT OF NEW CONNECTION
- POINT OF DISCONNECTION

HVAC CONTROL SYMBOLS

- THERMOSTAT
- ZONED THERMOSTAT
- ZONED THERMOSTAT - MASTER
- THERMOSTAT W/ LOCKABLE COVER
- WALL SWITCH
- HUMIDISTAT
- ROOM TEMPERATURE SENSOR
- ADJUSTABLE ROOM TEMPERATURE SENSOR
- COMBO ROOM TEMPERATURE & CO2 SENSOR
- ADJUSTABLE COMBO ROOM TEMP & CO2 SENSOR
- ROOM HUMIDITY SENSOR
- ROOM CO2 SENSOR
- BUILDING PRESSURE SENSOR
- STATIC PRESSURE SENSOR
- DIFFERENTIAL PRESSURE SENSOR
- CARBON MONOXIDE / NITRIC OXIDE SENSOR

NOTE: THIS IS A STANDARD LEGEND. NOT ALL PIPE TYPES AND SYMBOLS ARE NECESSARILY UTILIZED IN THE DRAWINGS.

HVAC DUCTWORK

- W"xD" — RECTANGULAR DUCT WIDTH x DEPTH
- X"ø — ROUND DUCT DIAMETER
- W"/D" — OVAL DUCT WIDTH/DEPTH
- X"ø — FLEXIBLE DUCT DIAMETER
- FLOOR/CEILING SUPPLY DIFFUSER
- FLOOR/CEILING RETURN GRILLE
- FLOOR/CEILING EXHAUST GRILLE
- SIDEWALL SUPPLY DIFFUSER
- SIDEWALL RETURN/EXHAUST GRILLE
- SUPPLY DUCT (SECTION VIEW)
- RETURN DUCT (SECTION VIEW)
- EXHAUST DUCT (SECTION VIEW)
- OUTDOOR AIR DUCT (SECTION VIEW)
- DUCT UP (PLAN VIEW)
- DUCT DOWN (PLAN VIEW)
- R — INCLINED RISE - IN DIRECTION OF AIRFLOW
- D — INCLINED DROP - IN DIRECTION OF AIRFLOW
- INTERNAL DUCT LINING
- ELBOW WITH TURNING VANES
- RADIUS ELBOW
- MANUAL VOLUME DAMPER
- MVD — REMOTE VOLUME DAMPER
- BD — BACKDRAFT DAMPER
- ZD — ZONE DAMPER
- BP — BYPASS DAMPER
- MD — MOTORIZED DAMPER
- FD — FIRE DAMPER
- FSD — FIRE/SMOKE DAMPER
- SD — SMOKE DAMPER

GENERAL

- (E) NAME — EXISTING PIPE TO REMAIN
- (D) NAME — EXISTING PIPE TO BE DEMOLISHED
- NAME — NEW PIPING
- DIRECTION OF FLOW

HVAC PIPING

- HWS — HEATING WATER SUPPLY
- HWR — HEATING WATER RETURN
- CWS — CHILLED WATER SUPPLY
- CWR — CHILLED WATER RETURN
- CTS — COOLING TOWER SUPPLY
- CTR — COOLING TOWER RETURN
- HPWS — HEAT PUMP WATER SUPPLY
- HPWR — HEAT PUMP WATER RETURN
- HPS — HIGH PRESSURE STEAM
- MPS — MEDIUM PRESSURE STEAM
- LPS — LOW PRESSURE STEAM
- CND — STEAM CONDENSATE RETURN
- ATV — ATMOSPHERIC VENT
- REF — REFRIGERANT (LIQUID AND SUCTION)
- NG — NATURAL GAS
- LPG — LIQUIFIED PETROLEUM GAS

PIPE FITTINGS

- ELBOW
- PIPE BREAK
- PIPE UP
- PIPE DOWN
- CHANGE IN ELEVATION OF PIPE
- SIDE CONNECTION OR TEE FITTING
- TOP CONNECTION
- BOTTOM CONNECTION
- UNION
- FLANGE
- CAPPED OUTLET
- BLIND FLANGE

VALVES

- COMBINATION Y-STRAINER & SHUTOFF VALVE
- COMBINATION AUTOFLOW & SHUTOFF VALVE
- MANUAL BALANCING VALVE
- AUTOFLOW VALVE
- ISOLATION VALVE - SEE SPECIFICATIONS FOR TYPE
- 3-WAY VALVE
- BUTTERFLY VALVE
- HOSE END DRAIN
- STRAINER
- MANUAL BALANCING VALVE
- AUTOFLOW VALVE
- CHECK VALVE
- BACKFLOW PREVENTER
- PRESSURE REDUCING VALVE
- TEMPERATURE AND PRESSURE RELIEF VALVE
- SOLENOID VALVE
- 2-WAY TEMPERATURE CONTROL VALVE
- 3-WAY TEMPERATURE CONTROL VALVE

PIPING SPECIALTIES

- AUTOMATIC AIR VENT
- MANUAL AIR VENT - 1/4" BALL VALVE WITH 12" SOFT COPPER TUBE
- PRESSURE / TEMPERATURE PORT
- DDC TEMPERATURE SENSOR
- DDC PRESSURE SENSOR
- PIPE WELL - EMPTY
- FS — FLOW SWITCH
- PS — PRESSURE SWITCH
- PRESSURE GAUGE
- PRESSURE GAUGE & COCK
- TEMPERATURE GAUGE
- SCHEMATIC PUMP
- FLEXIBLE CONNECTOR
- PIPE GUIDES
- ANCHOR
- THERMAL EXPANSION LOOP

MECH. SHEET INDEX

NUMBER	SHEET NAME
M000	MECHANICAL LEGEND AND NOTES
M001	MECHANICAL SCHEDULES
M101	LEVEL 1 MECHANICAL DEMOLITION PLAN
M102	LEVEL 2 MECHANICAL DEMOLITION PLAN
M201	LEVEL 1 MECHANICAL PLAN
M202	LEVEL 2 MECHANICAL PLAN

MECHANICAL GENERAL NOTES

INSTALLATION:

A. NEW PIPING, DUCTWORK AND EQUIPMENT TO BE INSTALLED IN ACCORDANCE WITH THE CURRENTLY ADOPTED INTERNATIONAL MECHANICAL AND INTERNATIONAL BUILDING CODES.
B. EQUIPMENT SHALL BE INSTALLED LEVEL, PLUMB, AND FIRMLY ANCHORED IN LOCATIONS INDICATED ON PLAN. OBSERVE MANUFACTURER'S INSTALLATION INSTRUCTIONS AND RECOGNIZED INDUSTRY PRACTICES TO ENSURE THAT PRODUCTS SERVE THEIR INTENDED FUNCTION.
C. INSTALL EQUIPMENT, DUCTWORK, AND PIPING SO AS TO MAINTAIN CODE REQUIRED CLEARANCES FOR ELECTRICAL AND TELECOMMUNICATION EQUIPMENT.
D. ELEMENTS PENETRATING BUILDING COMPONENTS (ROOF ASSEMBLIES, WALL ASSEMBLIES, ETC.) SHALL BE SEALED WEATHER AND WATER TIGHT. COORDINATE PENETRATIONS WITH GENERAL CONTRACTOR TO PATCH TO THE SATISFACTION OF THE ARCHITECT OR ENGINEER.
E. EQUIPMENT MANUFACTURED AFTER 1/1/2023 SHALL MEET MINIMUM SEER2 RATINGS.

COORDINATION:

A. IT SHALL BE THE RESPONSIBILITY OF THE MECHANICAL CONTRACTOR TO FIELD COORDINATE THE LOCATION OF EQUIPMENT, ROUTING OF DUCTWORK, AND ROUTING OF PIPING WITH OTHER TRADES.
B. IT SHALL BE THE RESPONSIBILITY OF THE MECHANICAL CONTRACTOR TO REVIEW THE DRAWINGS OF OTHER DISCIPLINES AND PROVIDE THE NECESSARY LABOR AND MATERIALS REQUIRED FOR A COMPLETE INSTALLATION.
C. COORDINATE THE INSTALLATION OF GRILLES, REGISTERS AND DIFFUSERS WITH THE ARCHITECTURAL REFLECTED CEILING PLANS, THE ELECTRICAL LIGHTING PLANS, AND IF RELEVANT, THE TELECOMMUNICATION AND FIRE SPRINKLER PLANS.

ELECTRICAL COORDINATION:

A. SEE THE MEP COORDINATION SCHEDULE FOR ELECTRICAL INFORMATION. COORDINATE WITH OTHER TRADES TO ENSURE THAT ELECTRICAL DISCONNECTS, MOTOR STARTERS, VARIABLE FREQUENCY DRIVES, CONTROLS, AND ELECTRICAL ACCESSORIES ARE FURNISHED AND/OR INSTALLED BY THE APPROPRIATE TRADE.

SITE ELEVATION:

A. EQUIPMENT SHALL BE SELECTED FOR THE PROJECT ELEVATION OF 3,413'.

mosaic
architecture-planning-design
317 Cruse Avenue Suite 201
Helena, Montana 59601
406.449.2013
www.mosaicarch.com

PROFESSIONAL ENGINEER LICENSED 22020 STATE OF IDAHO ROSS BALFOUR
06/26/2024

U.S. DEPARTMENT OF AGRICULTURE
FOREST SERVICE
R-1 NORTHERN REGION

Morrison Maierle
engineers · surveyors · planners · scientists
1 Engineer Place
Helena, MT 59602
406.442.3050
www.m-m.net

COPYRIGHT © MORRISON-MAIERLE, 2022

POWELL DUPLEX RENOVATION

LOCHSA-POWELL RANGER DISTRICT,
192 POWELL RD,
LOLO, ID 59847

CONSTRUCTION DOCUMENTS

MARK	DATE	REVISION

PROJECT NO. 1240LU23F0138
DATE: 7/19/2024
Drawn By: MRR
Designed By: JDB
Checked By: LHP

MECHANICAL LEGEND AND NOTES

SHEET: M000

DATE STAMP 7/19/2024 9:11:51 AM

MEP COORDINATION SCHEDULE

CONTROL TYPE:

BAS	BUILDING AUTOMATION SYSTEM
CO	CARBON MONOXIDE DETECTOR
CONT	CONTINUOUS OPERATION
EF	INTERLOCK WITH EXHAUST FAN
HCP	HOOD CONTROL PANEL
INT	INTEGRAL
L	LIGHT SWITCH
MS	MANUAL SWITCH
OS	OCCUPANCY SENSOR
PS	PRESSURE SWITCH
T	THERMOSTAT
TC	TIME CLOCK
UC	UNIT CONTROLLER
VE	VEHICLE EXHAUST DETECTION
N/A	SYSTEM...

DISCONNECT/STARTER TYPE:

CB	PANELBOARD CIRCUIT BREAKER WITHIN SIGHT OF EQUIPMENT
CSFD	COMBINATION STARTER/DISCONNECT - HOA
FD	FUSED DISCONNECT
FST	FUSTAT
FW	FACTORY-WIRED SINGLE POINT CONNECTION
MOCP	MOTOR OVER-CURRENT PROTECTION
MSS	MANUAL STARTER SWITCH WITH THERMAL OVERLOADS (1-, 2- OR 3-POLE AS REQUIRED)
NFD	NON-FUSED DISCONNECT
RCPT	20A DUPLEX RECEPTACLE (GFCI PROTECTED AS REQUIRED), CORD AND PLUG
RVSS	REDUCED VOLTAGE SOLID-STATE
VFD	VARIABLE FREQUENCY DRIVE - HOA
N/A	NOT APPLICABLE

DIVISION OF RESPONSIBILITIES:

22/22	FURNISHED AND INSTALLED BY DIV. 22, WIRED BY DIV. 22
22/26	FURNISHED AND INSTALLED BY DIV. 22, WIRED BY DIV. 26
23/23	FURNISHED AND INSTALLED BY DIV. 23, WIRED BY DIV. 23
23/26	FURNISHED AND INSTALLED BY DIV. 23, WIRED BY DIV. 26
26/26	FURNISHED AND INSTALLED BY DIV. 26, WIRED BY DIV. 26

NOTES:

1. INTEGRAL DISCONNECTS AND OVERLOADS
2. INTEGRAL OVERLOADS
3. SINGLE POINT CONNECTION
4. PROVIDE RECEPTACLE AND DATA CONNECTION FOR PANEL
5. MOUNT ON UNI-STRUT IN FRONT OF UNIT
6. SIZE FUSES IN ACCORDANCE WITH MANUFACTURER'S GUIDELINES FOR INSTALLED EQUIPMENT
7. INTEGRAL VARIABLE FREQUENCY DRIVE
8. DUCT SMOKE DETECTOR(S) REQUIRED

GENERAL NOTES:

A. CONTROL WIRING SHALL BE CONCEALED WITHIN WALL CONSTRUCTION, ABOVE CEILING, OR RUN IN CONDUIT. EXPOSED CONTROL WIRING IS UNACCEPTABLE.
B. UNLESS SPECIFICALLY NOTED, ALL FEEDERS SHALL INCLUDE A FULL SIZE NEUTRAL. IT IS THE CONTRACTOR'S RESPONSIBILITY TO VERIFY WITH THE MANUFACTURER OF THE ACTUAL EQUIPMENT BEING SUPPLIED WHETHER A NEUTRAL IS
C. REQUIRED PRIOR TO ROUGH-IN.
ALL DUCT SMOKE DETECTORS FURNISHED BY DIV. 26, INSTALLED BY DIV. 23, AND WIRED BY DIV. 26. DIV. 26 SHALL WIRE ALL FANS TO SHUT DOWN WHEN ALARM IS INITIATED BY ANY DUCT SMOKE DETECTOR.

MARK	DESCRIPTION	ELECTRICAL DATA		CONTROL		NOTES	DISCONNECT / STARTER		DISCONNECT				FEEDER	
		LOAD	VOLT-PHASE	TYPE	DIV		TYPE	DIV	SIZE (NEMA)	SWITCH (AMPS)	FUSE (AMPS)	ENCLOSURE (NEMA)	COPPER WIRE (AWG)	CONDUIT (INCHES)
BB-1	ELECTRIC BASEBOARD	2000 W	240 - 1	T	23 / 26	3	FW	23/26	--	--	20	1	12	3/4
BB-2	ELECTRIC BASEBOARD	2000 W	240 - 1	T	23 / 26	3	FW	23/26	--	--	20	1	12	3/4

ELECTRIC BASEBOARD SCHEDULE

ACCESSORIES:
1. PROVIDE WITH REMOTE WIRED THERMOSTAT.
2. PROVIDE INTEGRAL DISCONNECTING MEANS AND THERMAL OVERLOADS.

ELECTRICAL DATA:
SEE MEP COORDINATION SCHEDULE FOR STARTER/DISCONNECT AND ALL OTHER ELECTRICAL DATA.

MARK	MANUF.	MODEL	VOLTAGE-PH	WATTS	EFFECTIVE WATTAGE	FINISH	MOUNTING	PHYSICAL DATA		
								LENGTH (IN)	DEPTH (IN)	HEIGHT (IN)
BB-1	MARLEY	CBD	240 - 1	2000	- -	WHITE	WALL	94	2-15/16	8-3/8
BB-2	MARLEY	CBD	240 - 1	2000	- -	WHITE	WALL	94	2-15/16	8-3/8

DATE/STAMP 7/11/2024 10:33:21 AM

mosaic
architecture-planning-design
317 Cruse Avenue Suite 201
Helena, Montana 59601
406.449.2013
www.mosaicarch.com

PROFESSIONAL ENGINEER LICENSED 22020 STATE OF IDAHO ROSS BALFOUR

06/26/2024

U.S. DEPARTMENT OF AGRICULTURE
FOREST SERVICE
R-1 NORTHERN REGION

Morrison Maierle
engineers · surveyors · planners · scientists
1 Engineer Place
Helena, MT 59602
406.442.3050
www.m-m.net

COPYRIGHT © MORRISON-MAIERLE, 2022

POWELL DUPLEX RENOVATION

LOCHSA-POWELL RANGER DISTRICT,
192 POWELL RD,
LOLO, ID 59847


CONSTRUCTION DOCUMENTS

MARK	DATE	REVISION

PROJECT NO. 1240LU23F0138
DATE: 7/19/2024
Drawn By: MRR
Designed By: JDB
Checked By: LHP

MECHANICAL SCHEDULES

SHEET: **M001**

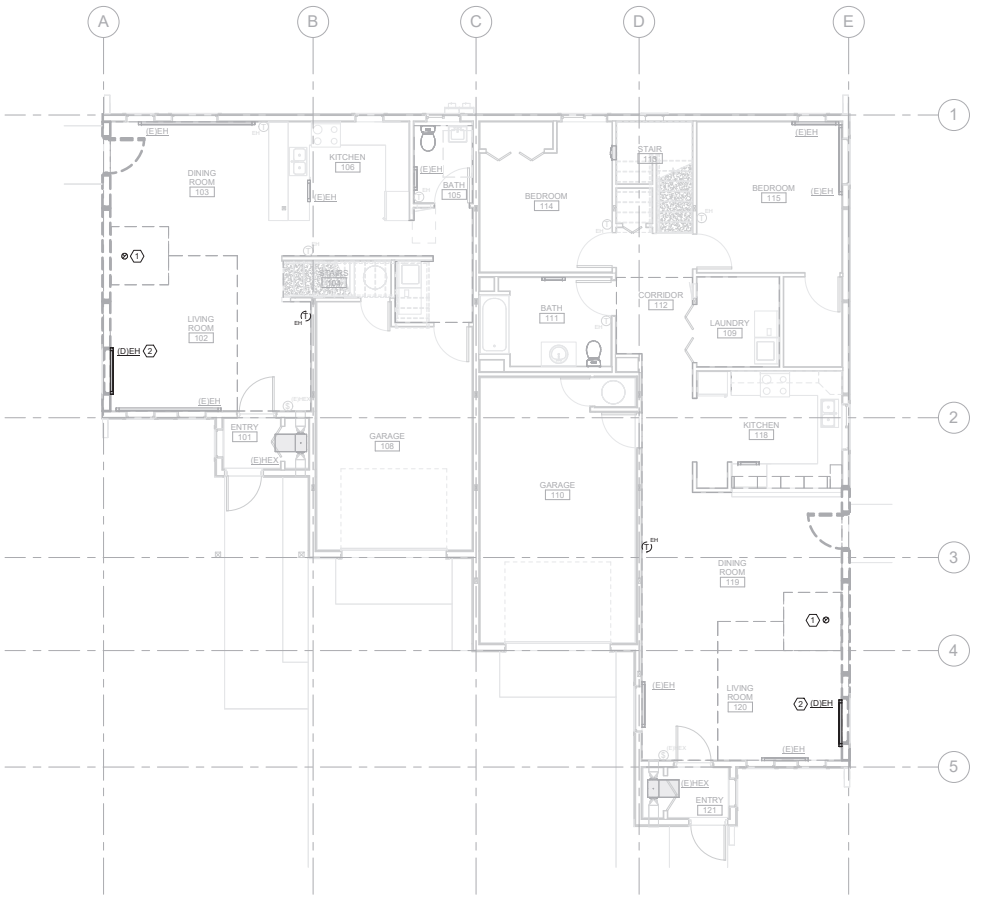

1 LEVEL 1 - MECHANICAL DEMOLITION PLAN
3/16" = 1'-0"

MECHANICAL DEMO NOTES

A. LOCATIONS AND DIMENSIONS OF EXISTING FACILITIES IDENTIFIED ON THIS DRAWING ARE APPROXIMATE AND REPRESENT THE BEST AVAILABLE INFORMATION BASED ON A COMBINATION OF FIELD INVESTIGATIONS AND VARIOUS DESIGN AND RECORD DRAWINGS AVAILABLE AT THE TIME OF THE DESIGN. FIELD VERIFY LOCATIONS AND DIMENSIONS PRIOR TO AND DURING PERFORMANCE OF THE WORK. PROVIDE DEMOLITION WORK NECESSARY TO COMPLETE THE SCOPE OUTLINED IN THE CONSTRUCTION DOCUMENTS.
B. EXISTING MECHANICAL EQUIPMENT, DUCTWORK, AND PIPING SHOWN AS DARK AND DASHED SHALL BE DEMOLISHED. EXISTING MECHANICAL EQUIPMENT, DUCTWORK, AND PIPING SHOWN LIGHT SHALL REMAIN UNCHANGED.
C. THE MECHANICAL CONTRACTOR SHALL COORDINATE SALVAGE OF REMOVED EQUIPMENT IN GOOD CONDITION WITH THE OWNER. THE MECHANICAL CONTRACTOR SHALL DISPOSE OF UNWANTED EQUIPMENT.
D. COORDINATE UTILITY OUTAGES WITH THE GENERAL CONTRACTOR THROUGHOUT THE DURATION OF CONSTRUCTION. NOTIFICATION MUST BE GIVEN TO THE OWNER AT LEAST A WEEK PRIOR TO ANY PLANNED OUTAGES.
E. COORDINATE WITH THE GENERAL CONTRACTOR TO PATCH AND REPAIR ROOF, WALL, CEILING, OR FLOOR PENETRATIONS ASSOCIATED WITH THE DEMOLITION OF THE EXISTING MECHANICAL SYSTEMS.

KEY NOTES:

1. LOCATION FOR THE FLUE VENT PIPE FROM THE WOOD FIRED STOVE. THE OWNER HAS PREVIOUSLY DEMOLISHED THE FLUE VENT PIPE FROM THE WOOD FIRED STOVE UP THROUGH THE ROOF COMPLETE UP TO AND INCLUDING THE TERMINATION CAP AND ANY SUPPORT WIRES. NO ADDITIONAL WORK REQUIRED.
2. DEMOLISH THE EXISTING ELECTRIC HEATER (EH). COORDINATE WITH ELECTRICAL. THE EXTERIOR WALL SHALL BE REMOVED AND REPLACED, COORDINATE WITH GENERAL CONTRACTOR FOR NEW ELECTRIC HEATER.

mosaic
architecture-planning-design
317 Cruse Avenue Suite 201
Helena, Montana 59601
406.449.2013
www.mosaicarch.com

PROFESSIONAL ENGINEER LICENSED 22020 STATE OF IDAHO ROSS BALFOUR
06/26/2024

U.S. DEPARTMENT OF AGRICULTURE
FOREST SERVICE
R-1 NORTHERN REGION

Morrison Maierle
engineers · surveyors · planners · scientists
1 Engineer Place
Helena, MT 59602
406.442.3050
www.m-m.net

COPYRIGHT © MORRISON-MAIERLE, 2022

POWELL DUPLEX RENOVATION

LOCHSA-POWELL RANGER DISTRICT,
192 POWELL RD,
LOLO, ID 59847

CONSTRUCTION DOCUMENTS


MARK	DATE	REVISION

PROJECT NO. 1240LU23F0138
DATE: 7/19/2024
Drawn By: MRR
Designed By: JDB
Checked By: LHP

LEVEL 1 MECHANICAL DEMOLITION PLAN

SHEET: **M101**

DATESTAMP 7/17/2024 10:33:22 AM

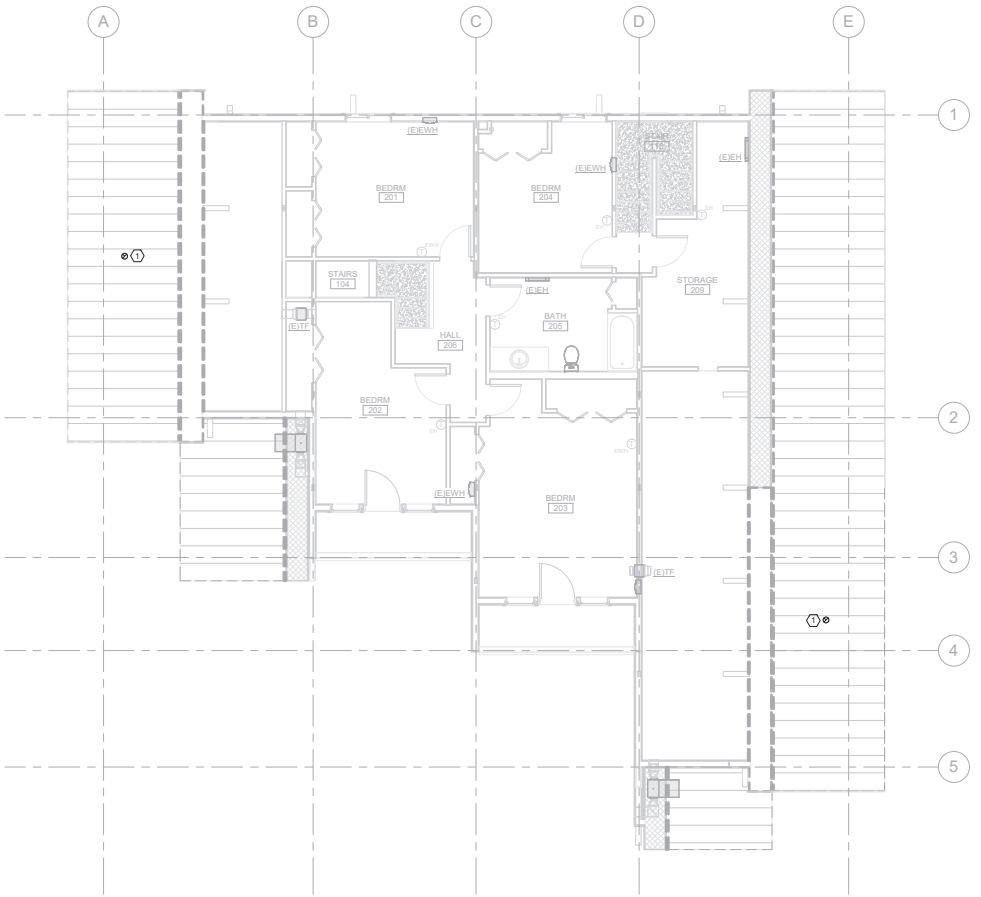

1 LEVEL 2 - MECHANICAL DEMOLITION PLAN
3/16" = 1'-0"

MECHANICAL DEMO NOTES

A. LOCATIONS AND DIMENSIONS OF EXISTING FACILITIES IDENTIFIED ON THIS DRAWING ARE APPROXIMATE AND REPRESENT THE BEST AVAILABLE INFORMATION BASED ON A COMBINATION OF FIELD INVESTIGATIONS AND VARIOUS DESIGN AND RECORD DRAWINGS AVAILABLE AT THE TIME OF THE DESIGN. FIELD VERIFY LOCATIONS AND DIMENSIONS PRIOR TO AND DURING PERFORMANCE OF THE WORK. PROVIDE DEMOLITION WORK NECESSARY TO COMPLETE THE SCOPE OUTLINED IN THE CONSTRUCTION DOCUMENTS.
B. EXISTING MECHANICAL EQUIPMENT, DUCTWORK, AND PIPING SHOWN AS DARK AND DASHED SHALL BE DEMOLISHED. EXISTING MECHANICAL EQUIPMENT, DUCTWORK, AND PIPING SHOWN LIGHT SHALL REMAIN UNCHANGED.
C. THE MECHANICAL CONTRACTOR SHALL COORDINATE SALVAGE OF REMOVED EQUIPMENT IN GOOD CONDITION WITH THE OWNER. THE MECHANICAL CONTRACTOR SHALL DISPOSE OF UNWANTED EQUIPMENT.
D. COORDINATE UTILITY OUTAGES WITH THE GENERAL CONTRACTOR THROUGHOUT THE DURATION OF CONSTRUCTION. NOTIFICATION MUST BE GIVEN TO THE OWNER AT LEAST A WEEK PRIOR TO ANY PLANNED OUTAGES.
E. COORDINATE WITH THE GENERAL CONTRACTOR TO PATCH AND REPAIR ROOF, WALL, CEILING, OR FLOOR PENETRATIONS ASSOCIATED WITH THE DEMOLITION OF THE EXISTING MECHANICAL SYSTEMS.

KEY NOTES:

1. LOCATION FOR THE FLUE VENT PIPE FROM THE WOOD FIRED STOVE. THE OWNER HAS PREVIOUSLY DEMOLISHED THE FLUE VENT PIPE FROM THE WOOD FIRED STOVE UP THROUGH THE ROOF COMPLETE UP TO AND INCLUDING THE TERMINATION CAP AND ANY SUPPORT WIRES. NO ADDITIONAL WORK REQUIRED.

mosaic
architecture-planning-design
317 Cruse Avenue Suite 201
Helena, Montana 59601
406.449.2013
www.mosaicarch.com

PROFESSIONAL ENGINEER LICENSED 22020 STATE OF IDAHO ROSS BALFOUR
06/26/2024

FOREST SERVICE U.S. DEPARTMENT OF AGRICULTURE
U.S. DEPARTMENT OF AGRICULTURE
FOREST SERVICE
R-1 NORTHERN REGION

Morrison Maierle
engineers · surveyors · planners · scientists
1 Engineer Place
Helena, MT 59602
406.442.3050
www.m-m.net

COPYRIGHT © MORRISON-MAIERLE, 2022

POWELL DUPLEX RENOVATION

LOCHSA-POWELL RANGER DISTRICT,
192 POWELL RD,
LOLO, ID 59847

CONSTRUCTION DOCUMENTS


MARK	DATE	REVISION

PROJECT NO. 1240L023F0138
DATE: 7/19/2024
Drawn By: MRR
Designed By: JDB
Checked By: LHP

LEVEL 2 MECHANICAL DEMOLITION PLAN

SHEET: **M102**

DATESTAMP 7/17/2024 10:33:23 AM

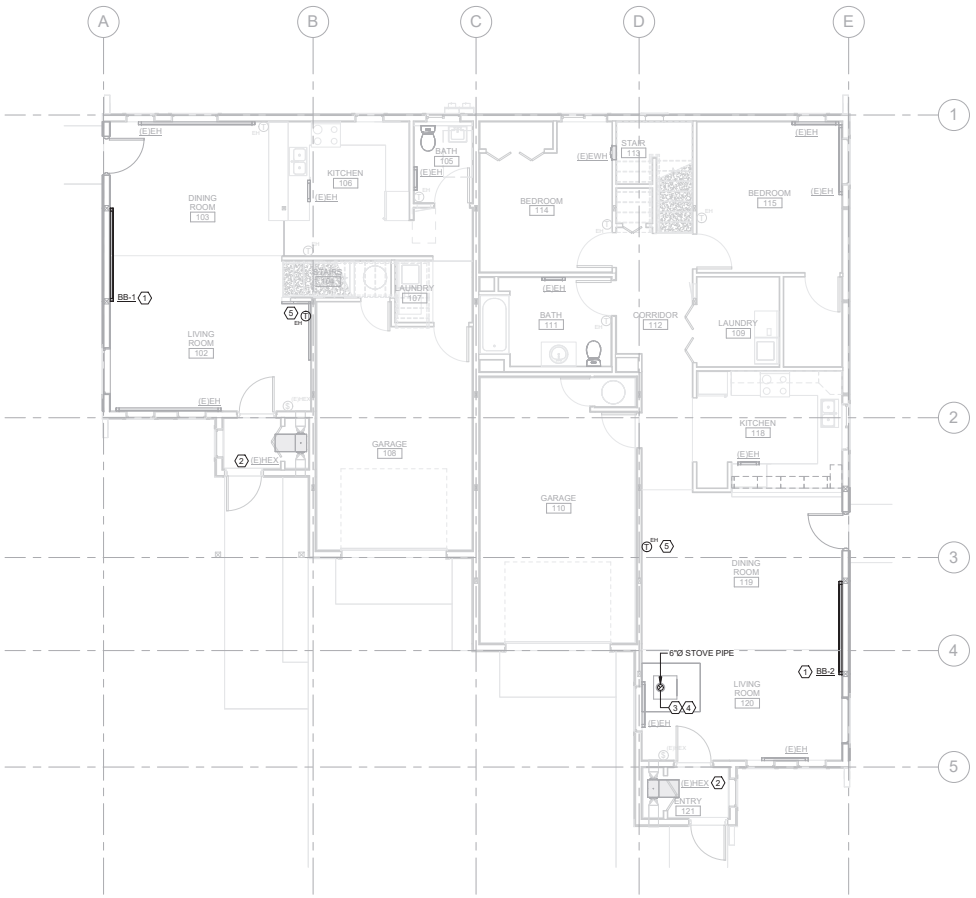

1 LEVEL 1 - MECHANICAL PLAN
3/16" = 1'-0"

MECHANICAL PLAN NOTES

A. VERIFY THE LOCATION OF THERMOSTATS AND SENSORS WITH THE ARCHITECT AND ENGINEER PRIOR TO INSTALLATION. INSTALL THERMOSTATS 48" ABOVE FINISHED FLOOR PER ABA REQUIREMENTS.
B. PROVIDE AND INSTALL SEISMIC BRACING FOR EQUIPMENT, DUCTWORK AND PIPING PER THE REQUIREMENTS OF THE CURRENTLY ADOPTED INTERNATIONAL BUILDING CODE.
C. FLEXIBLE DUCTWORK BETWEEN BRANCH DUCTS AND GRILLES, REGISTERS, OR DIFFUSERS SHALL BE LIMITED TO 5 FT. FLEXIBLE DUCT SHALL NOT BE USED IN PLACE OF ELBOWS.
D. PROVIDE AND INSTALL FIRE, SMOKE, OR COMBINATION FIRE/SMOKE DAMPERS WHERE DUCTWORK PASSES THROUGH RATED ASSEMBLIES. ASSOCIATED DUCT DETECTORS SHALL BE ADDRESSABLE. SMOKE DAMPERS AND COMBINATION SMOKE/FIRE DAMPERS SHALL INCLUDE A KEYED REMOTE TEST SWITCH LOCATED IN AN ACCESSIBLE LOCATION. FIELD COORDINATE THE LOCATION OF TEST SWITCHES WITH THE ARCHITECT AND ENGINEER PRIOR TO INSTALLATION.
E. SEAL DUCT AND PIPE PENETRATIONS THROUGH FIRE RATED ASSEMBLIES WITH A UL-APPROVED FIRE STOP SYSTEM.
F. MAINTAIN THE INTEGRITY OF DRAFTSTOPPING WHERE DUCTWORK AND PIPING PENETRATE DRAFTSTOPPING MATERIALS.
G. PROVIDE ACCESS DOORS TO ALLOW SERVICE AND INSPECTION OF EQUIPMENT, VALVES, DAMPERS AND DEVICES INSTALLED ABOVE NON-REMOVABLE CEILINGS. COORDINATE SUCH INSTALLATIONS WITH THE ARCHITECT AND ENGINEER.
H. PIPING SHALL BE IDENTIFIED WITH PIPE LABELS MARKED AT A MAXIMUM OF EVERY 25 FT. VALVES SHALL BE IDENTIFIED WITH BRASS OR ALUMINUM VALVE TAGS.
I. PROVIDE AND INSTALL PIPE GUIDES, EXPANSION JOINTS, AND HANGERS PER MANUFACTURER'S RECOMMENDATIONS.
J. PIPING WALL PENETRATIONS SHALL SHALL BE FINISHED WITH A CHROME ESCUTCHEON PLATE.
K. MINIMUM TERMINAL DEVICE BRANCH PIPE SIZE IS 3/4"ø UNLESS OTHERWISE NOTED.
L. PROVIDE HIGH POINT AIR VENTS, LOW POINT DRAINS (WITH CAPPED HOSE CONNECTIONS), AND SLOPE PIPING AS NECESSARY TO ALLOW FOR COMPLETE DRAINAGE OF THE HYDRONIC SYSTEMS.
M. EXPOSED DUCTWORK TO BE HOT DIPPED GALVANIZED STEEL AND PAINTED PER ARCHITECTURAL. CONTRACTOR TO CLEAN AND DRY DUCTWORK PRIOR TO PAINTING.

KEY NOTES:

1. COORDINATE INSTALLATION OF NEW ELECTRIC BASEBOAD WITH GENERAL CONTRACTOR. EXTERIOR WALL IS A NEW SECTION.
2. NO WORK WITH THIS EQUIPMENT.
3. CONNECT CONTRACTOR-FURNISHED CONTRACTOR INSTALLED CLASS 'A' STOVE PIPE TO OWNER-FURNISHED OWNER-INSTALLED WOOD STOVE PER MANUFACTURER'S INSTALLATION INSTRUCTIONS.
4. FURNISH AND INSTALL CLASS 'A' FLOOR SUPPORT BRACKET AT FLOOR/CEILING ASSEMBLY.
5. NEW ELECTRIC BASEBOARD THERMOSTAT TO REPLACE EXISTING.

mosaic
architecture-planning-design
317 Cruse Avenue Suite 201
Helena, Montana 59601
406.449.2013
www.mosaicarch.com

PROFESSIONAL ENGINEER LICENSED 22020 STATE OF IDAHO ROSS BALFOUR
06/26/2024

U.S. DEPARTMENT OF AGRICULTURE
FOREST SERVICE
R-1 NORTHERN REGION

Morrison Maierle
engineers · surveyors · planners · scientists
1 Engineer Place
Helena, MT 59602
406.442.3050
www.m-m.net

COPYRIGHT © MORRISON-MAIERLE, 2022

POWELL DUPLEX RENOVATION

LOCHSA-POWELL RANGER DISTRICT,
192 POWELL RD,
LOLO, ID 59847

CONSTRUCTION DOCUMENTS


MARK	DATE	REVISION

PROJECT NO. 1240LU23F0138
DATE: 7/19/2024
Drawn By: MRR
Designed By: JDB
Checked By: LHP

LEVEL 1 MECHANICAL PLAN

SHEET: **M201**

DATESTAMP 7/17/2024 10:33:24 AM

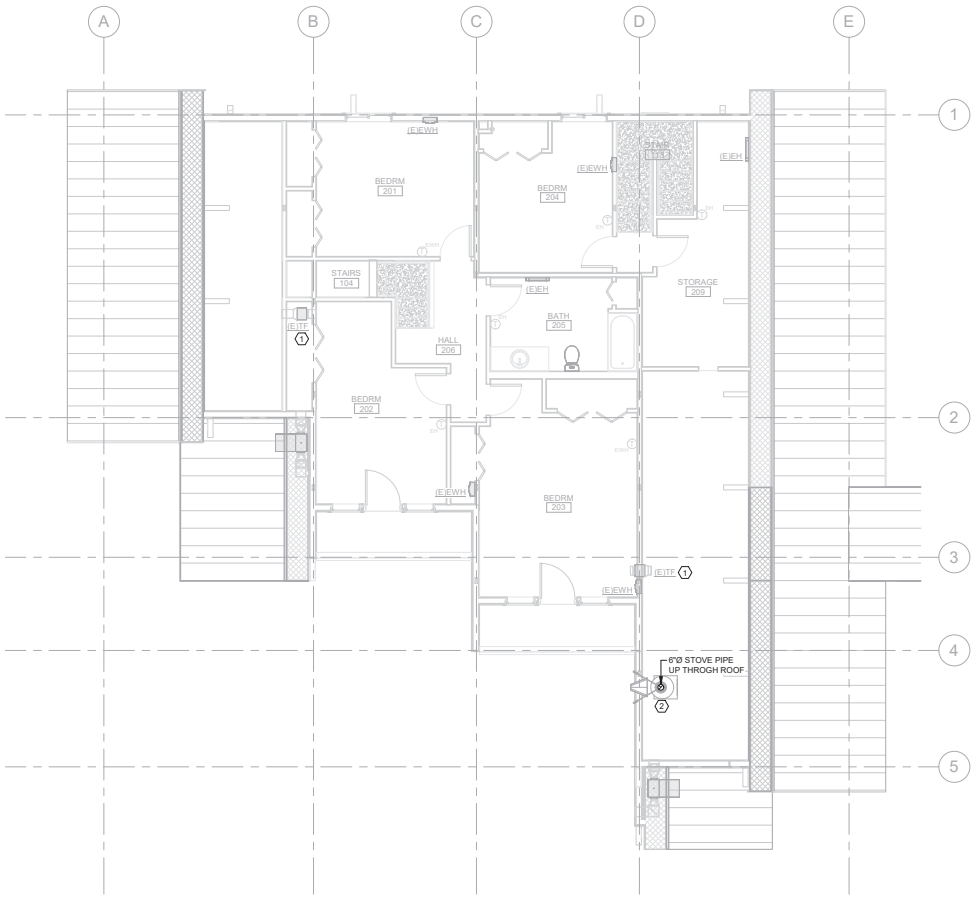


1 LEVEL 2 - MECHANICAL PLAN
3/16" = 1'-0"

MECHANICAL PLAN NOTES

A. VERIFY THE LOCATION OF THERMOSTATS AND SENSORS WITH THE ARCHITECT AND ENGINEER PRIOR TO INSTALLATION. INSTALL THERMOSTATS 48" ABOVE FINISHED FLOOR PER ABA REQUIREMENTS.
B. PROVIDE AND INSTALL SEISMIC BRACING FOR EQUIPMENT, DUCTWORK AND PIPING PER THE REQUIREMENTS OF THE CURRENTLY ADOPTED INTERNATIONAL BUILDING CODE.
C. FLEXIBLE DUCTWORK BETWEEN BRANCH DUCTS AND GRILLES, REGISTERS, OR DIFFUSERS SHALL BE LIMITED TO 5 FT. FLEXIBLE DUCT SHALL NOT BE USED IN PLACE OF ELBOWS.
D. PROVIDE AND INSTALL FIRE, SMOKE, OR COMBINATION FIRE/SMOKE DAMPERS WHERE DUCTWORK PASSES THROUGH RATED ASSEMBLIES. ASSOCIATED DUCT DETECTORS SHALL BE ADDRESSABLE. SMOKE DAMPERS AND COMBINATION SMOKE/FIRE DAMPERS SHALL INCLUDE A KEYED REMOTE TEST SWITCH LOCATED IN AN ACCESSIBLE LOCATION. FIELD COORDINATE THE LOCATION OF TEST SWITCHES WITH THE ARCHITECT AND ENGINEER PRIOR TO INSTALLATION.
E. SEAL DUCT AND PIPE PENETRATIONS THROUGH FIRE RATED ASSEMBLIES WITH A UL-APPROVED FIRE STOP SYSTEM.
F. MAINTAIN THE INTEGRITY OF DRAFTSTOPPING WHERE DUCTWORK AND PIPING PENETRATE DRAFTSTOPPING MATERIALS.
G. PROVIDE ACCESS DOORS TO ALLOW SERVICE AND INSPECTION OF EQUIPMENT, VALVES, DAMPERS AND DEVICES INSTALLED ABOVE NON-REMOVABLE CEILINGS. COORDINATE SUCH INSTALLATIONS WITH THE ARCHITECT AND ENGINEER.
H. PIPING SHALL BE IDENTIFIED WITH PIPE LABELS MARKED AT A MAXIMUM OF EVERY 25 FT. VALVES SHALL BE IDENTIFIED WITH BRASS OR ALUMINUM VALVE TAGS.
I. PROVIDE AND INSTALL PIPE GUIDES, EXPANSION JOINTS, AND HANGERS PER MANUFACTURER'S RECOMMENDATIONS.
J. PIPING WALL PENETRATIONS SHALL SHALL BE FINISHED WITH A CHROME ESCUTCHEON PLATE.
K. MINIMUM TERMINAL DEVICE BRANCH PIPE SIZE IS 3/4"ø UNLESS OTHERWISE NOTED.
L. PROVIDE HIGH POINT AIR VENTS, LOW POINT DRAINS (WITH CAPPED HOSE CONNECTIONS), AND SLOPE PIPING AS NECESSARY TO ALLOW FOR COMPLETE DRAINAGE OF THE HYDRONIC SYSTEMS.
M. EXPOSED DUCTWORK TO BE HOT DIPPED GALVANIZED STEEL AND PAINTED PER ARCHITECTURAL. CONTRACTOR TO CLEAN AND DRY DUCTWORK PRIOR TO PAINTING.

KEY NOTES:

1. NO WORK WITH THIS EQUIPMENT.
2. FURNISH AND INSTALL CLASS 'A' ROOF SUPPORT BRACKET AT BOTTOM OF THE ROOF PANEL ASSEMBLY. MAINTAIN 2" OF CLEARANCE TO COMBUSTIBLE MATERIALS.

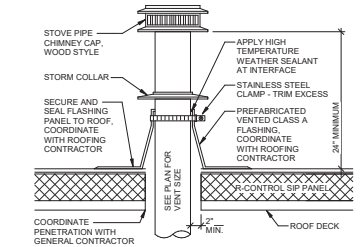

2 STOVE PIPE UP THRU ROOF DETAIL
N.T.S.

mosaic
architecture-planning-design
317 Cruse Avenue Suite 201
Helena, Montana 59601
406.449.2013
www.mosaicarch.com

PROFESSIONAL ENGINEER LICENSED 22020 STATE OF IDAHO ROSS BALFOUR
06/26/2024

FOREST SERVICE U.S. DEPARTMENT OF AGRICULTURE

U.S. DEPARTMENT OF AGRICULTURE
FOREST SERVICE
R-1 NORTHERN REGION

Morrison Maierle
engineers · surveyors · planners · scientists
1 Engineer Place
Helena, MT 59602
406.442.3050
www.m-m.net

COPYRIGHT © MORRISON-MAIERLE, 2022

POWELL DUPLEX RENOVATION

LOCHSA-POWELL RANGER DISTRICT,
192 POWELL RD,
LOLO, ID 59847

CONSTRUCTION DOCUMENTS

MARK	DATE	REVISION

PROJECT NO. 1240LU23F0138
DATE: 7/19/2024
Drawn By: MRR
Designed By: JDB
Checked By: LHP

LEVEL 2 MECHANICAL PLAN

SHEET: **M202**

DATESTAMP 7/17/2024 10:33:24 AM

ABBREVIATIONS

ACC	AIR COOLED CONDENSER
ACU	AIR CONDITIONING UNIT
AD	ACCESS DOOR
ADJ	ADJUSTABLE
AF	AIR FOIL
AFF	ABOVE FINISHED FLOOR
AFG	ABOVE FINISHED GRADE
AFR	ABOVE FINISHED ROOF
AFS	AIR FLOW STATION
AHU	AIR HANDLING UNIT
AP	ACCESS PANEL
ATC	AUTOMATIC TEMPERATURE CONTROL
ATM	ATMOSPHERE
AWG	AMERICAN WIRE GAUGE
B	BOILER
BB	BASEBOARD
BC	BACKWARD CURVED
BD	BACKDRAFT DAMPER
BF	BOILER FEED
BHP	BRAKE HORSEPOWER
BI	BACKWARD INCLINED
BMS	BUILDING MANAGEMENT SYSTEM
BOD	BOTTOM OF DUCT
BOJ	BOTTOM OF JOIST
BOS	BOTTOM OF STEEL
BTU	BRITISH THERMAL UNIT
C	COMMON
CAV	CONSTANT AIR VOLUME
CC	COOLING COIL
CCW	COUNTER CLOCKWISE
CFM	CUBIC FEET PER MINUTE
CH	CHILLER
C&I	CONTROLS & INSTRUMENTATION
CLG	CEILING
CMU	CONCRETE MASONRY UNIT
CND	CONDENSATE
CONT	CONTINUATION
CORR	CORRIDOR
COTG	CLEANOUT TO GRADE
CT	COOLING TOWER
CU	CONDENSING UNIT
CH	CABINET HEATER
CV	CONTROL VALVE
CVS	CONTROL VALVE STATION
CW	CLOCKWISE
dB	DECIBEL
DB	DRY BULB TEMPERATURE (°F)
DDC	DIRECT DIGITAL CONTROL
DH	DUCT HEATER
DP	DEW POINT TEMPERATURE (°F)
DX	DIRECT EXPANSION
E	EXHAUST
EA	EXHAUST AIR
EAT	ENTERING AIR TEMPERATURE (°F)
EC	ELECTRICAL CONTRACTOR
ECO	EXTERIOR CLEANOUT
EDR	EQUIVALENT DIRECT RADIATION
EER	ENERGY EFFICIENCY RATIO
EF	EXHAUST FAN
EFF	EFFICIENCY
ELEV	ELEVATION
ERV	ENERGY RECOVERY VENTILATOR
ESP	EXTERNAL STATIC PRESSURE
ET	EXPANSION TANK
EWT	ENTERING WATER TEMPERATURE (°F)
F&T	FLOAT & THERMOSTATIC
FA	FACE AREA
FC	FAN COIL
FP	FIRE PROTECTION
FPM	FEET PER MINUTE
FT	FEET
GA	GAUGE OR GAGE
GC	GENERAL CONTRACTOR
GEN	GENERATOR
GH	GRAVITY HOOD
GPD	GALLONS PER DAY
GPH	GALLONS PER HOUR
GPM	GALLONS PER MINUTE
H	HUMIDIFIER
HC	HEATING COIL
HG	MERCURY
HP	HORSEPOWER
HR	HOUR
HX	HEAT EXCHANGER
ID	INSIDE DIAMETER
IFB	INTEGRAL FACE & BYPASS
IGV	INLET GUIDE VANES
IPS	IRON PIPE SIZE
IU	INDUCTION UNIT
KW	KILOWATTS
KWH	KILOWATT HOUR
LAT	LEAVING AIR TEMPERATURE (°F)
LF	LINEAR FEET
LWT	LEAVING WATER TEMPERATURE (°F)
M	MOTOR OPERATED
MAU	MAKEUP AIR UNIT
MB	MIXING BOX
MBH	1000 BTU/HR
MC	MECHANICAL CONTRACTOR
MFR	MANUFACTURER
MS	MINI-SPLIT
NC	NOISE CRITERIA
NC	NORMALLY CLOSED
NIC	NOT IN CONTRACT
NO	NORMALLY OPEN
NPS	NOMINAL PIPE SIZE
OA	OUTSIDE AIR
OAD	OUTSIDE AIR DAMPER
OBD	OPPOSED BLADE DAMPER
P	PUMP
PC	PLUMBING CONTRACTOR
PD	PRESSURE DROP
PH	PHASE
PHC	PREHEAT COIL
PPM	PART PER MILLION
PROP	PROPELLER
PRV	PRESSURE REDUCING VALVE
PSIA	PSI, ABSOLUTE
PSIG	PSI, GAUGE
QTY	QUANTITY
R	REGISTER
RA	RETURN AIR
RD	RADIAL DAMPER
RF	RETURN/RELIEF AIR FAN
RH	RELATIVE HUMIDITY
RHC	REHEAT COIL
SA	SUPPLY AIR
SAF	SUPPLY AIR FAN
SC	SENSIBLE COOLER
SCFM	CFM, STANDARD CONDITIONS
SD	SMOKE DETECTOR
SEER	SEASONAL ENERGY EFFICIENCY RATIO
SENS	SENSIBLE
SP	STATIC PRESSURE
SPS	STATIC PRESSURE SENSOR
SS	STAINLESS STEEL
T	THERMOSTAT
TA	TRANSFER AIR
TCC	TEMPERATURE CONTROL CONTRACTOR
TCP	TEMPERATURE CONTROL PANEL
TG	TRANSFER GRILL
TOD	TOP OF DUCT
TOP	TOP OF PIPE
TOS	TOP OF STEEL
TSP	TOTAL STATIC PRESSURE
TYP	TYPICAL
UH	UNIT HEATER
UNC	UNDERCUT
UV	UNIT VENTILATOR
VA	VOLT-AMPERE
VAV	VARIABLE AIR VOLUME
VD	VOLUME DAMPER
VEL	VELOCITY
VFD	VARIABLE FREQUENCY DRIVE
VRF	VARIABLE REFRIGERANT FLOW
VTR	VENT THROUGH ROOF
WB	WET BULB TEMPERATURE (°F)
WC	WATER COLUMN
WG	WATER GAUGE
WSHP	WATER SOURCE HEAT PUMP
ΔT	TEMPERATURE DIFFERENCE (°F)

PLUMBING LEGEND

ANNOTATION SYMBOLS

- 3D VIEW NUMBER / SHEET NUMBER
- DETAIL NUMBER / SHEET NUMBER
- SECTION NUMBER / SHEET NUMBER
- PF-# — PLUMBING FIXTURE / EQUIPMENT MARK
- (PF-#) — PLUMBING FIXTURE (LOCATED ON FLOOR ABOVE)
- (E) PF-# — EXISTING PLUMBING FIXTURE / EQUIPMENT
- (D) PF-# — DEMOLISHED PLUMBING FIXTURE / EQUIPMENT
- POINT OF NEW CONNECTION
- POINT OF DISCONNECTION
- 1/4" SLOPE — DIRECTION OF FLOW AND SLOPE PER FOOT

GENERAL

- NAME (E) — EXISTING PIPE TO REMAIN
- NAME (D) — EXISTING PIPE TO BE DEMOLISHED
- NAME — NEW PIPING
- DIRECTION OF FLOW

PLUMBING

- DCW — DOMESTIC COLD WATER
- DHW — DOMESTIC HOT WATER (120°F)
- DHWR — DOMESTIC HOT WATER RECIRC.
- HTHW — HIGH TEMPERATURE HOT WATER (140°F)
- IRR — IRRIGATION
- RO — REVERSE OSMOSIS TREATED
- SAN — SANITARY WASTE
- V — SANITARY VENT
- GW — GREASE WASTE
- AW — ACID WASTE
- AV — ACID VENT
- RWL — RAIN WATER LEADER
- ORL — RAIN WATER OVERFLOW
- CND — CONDENSATE DRAIN
- CA — COMPRESSED AIR

PIPE FITTINGS

- ELBOW
- PIPE BREAK
- PIPE UP
- PIPE DOWN
- CHANGE IN ELEVATION OF PIPE
- SIDE CONNECTION OR TEE FITTING
- TOP CONNECTION
- BOTTOM CONNECTION
- UNION
- FLANGE
- CAPPED OUTLET
- BLIND FLANGE

VALVES

- COMBINATION Y-STRAINER & SHUTOFF VALVE
- COMBINATION AUTOFLOW & SHUTOFF VALVE
- MANUAL BALANCING VALVE
- AUTOFLOW VALVE
- ISOLATION VALVE - SEE SPECIFICATIONS FOR TYPE
- 3-WAY VALVE
- BUTTERFLY VALVE
- HOSE END DRAIN
- STRAINER
- MANUAL BALANCING VALVE
- AUTOFLOW VALVE
- CHECK VALVE
- BACKFLOW PREVENTER
- PRESSURE REDUCING VALVE
- TEMPERATURE AND PRESSURE RELIEF VALVE
- SOLENOID VALVE
- 2-WAY TEMPERATURE CONTROL VALVE
- 3-WAY TEMPERATURE CONTROL VALVE

PIPING SPECIALTIES

- AUTOMATIC AIR VENT
- MANUAL AIR VENT - 1/4" BALL VALVE WITH 12" SOFT COPPER TUBE
- PRESSURE / TEMPERATURE PORT
- DDC TEMP SENSOR
- DDC PRESSURE SENSOR
- PIPE WELL - EMPTY
- FLOW SWITCH
- PRESSURE SWITCH
- PRESSURE GAUGE
- PRESSURE GAUGE & COCK
- TEMPERATURE GAUGE
- SCHEMATIC PUMP
- FLEXIBLE CONNECTOR
- PIPE GUIDES
- ANCHOR
- THERMAL EXPANSION LOOP
- WATER METER
- FLOOR CLEAN OUT
- WALL CLEAN OUT
- WATER HAMMER ARRESTER
- HOSE BIBB
- WALL HYDRANT
- IRRIGATION BLOWOUT PORT

NOTE: THIS IS A STANDARD LEGEND. NOT ALL PIPE TYPES AND SYMBOLS ARE NECESSARILY UTILIZED IN THE DRAWINGS.

PLUMBING SHEET INDEX

NUMBER	SHEET NAME
P000	PLUMBING LEGEND AND NOTES
P001	PLUMBING SCHEDULES
P101	LEVEL 1 PLUMBING DEMOLITION PLAN
P102	LEVEL 2 PLUMBING DEMOLITION PLAN
P201	LEVEL 1 PLUMBING PLAN
P202	LEVEL 2 PLUMBING PLAN

PLUMBING GENERAL NOTES

INSTALLATION:

A. NEW PIPING AND EQUIPMENT TO BE INSTALLED IN ACCORDANCE WITH THE CURRENTLY ADOPTED INTERNATIONAL PLUMBING AND INTERNATIONAL BUILDING CODES.

B. EQUIPMENT SHALL BE INSTALLED LEVEL, PLUMB, AND FIRMLY ANCHORED IN LOCATIONS INDICATED. OBSERVE MANUFACTURER'S INSTALLATION INSTRUCTIONS AND RECOGNIZED INDUSTRY PRACTICES TO ENSURE THAT PRODUCTS SERVE THEIR INTENDED FUNCTION.

C. DRAWINGS ARE DIAGRAMMATIC IN NATURE. THE PURPOSE OF THESE PLANS IS TO INDICATE THE INTENDED SIZES, APPROXIMATE LOCATION AND ROUTING OF MAJOR COMPONENTS. ACTUAL CONDITIONS AND LOCATIONS SHALL BE FIELD VERIFIED AND ADJUSTED IF NECESSARY.

D. PROVIDE AND INSTALL SEISMIC BRACING FOR EQUIPMENT AND PIPING PER THE REQUIREMENTS OF THE CURRENTLY ADOPTED INTERNATIONAL BUILDING CODE.

E. ELEMENTS PENETRATING BUILDING COMPONENTS (ROOF ASSEMBLIES, WALL ASSEMBLIES, ETC.) SHALL BE SEALED WEATHER AND WATER TIGHT. COORDINATE PENETRATIONS WITH GENERAL CONTRACTOR TO PATCH TO THE SATISFACTION OF THE ARCHITECT OR ENGINEER.

F. MATERIAL THAT IS IN CONTACT WITH POTABLE DOMESTIC WATER SHALL BE NSF CERTIFIED LEAD FREE.

COORDINATION:

A. IT SHALL BE THE RESPONSIBILITY OF THE PLUMBING CONTRACTOR TO FIELD COORDINATE THE LOCATION OF EQUIPMENT AND ROUTING OF PIPING WITH OTHER TRADES.

B. IT SHALL BE THE RESPONSIBILITY OF THE PLUMBING CONTRACTOR TO REVIEW THE DRAWINGS OF OTHER DISCIPLINES AND PROVIDE LABOR AND MATERIALS REQUIRED FOR A COMPLETE INSTALLATION.

ELECTRICAL COORDINATION:

A. SEE THE MEP COORDINATION SCHEDULE FOR ELECTRICAL INFORMATION. COORDINATE WITH OTHER TRADES TO ENSURE THAT ELECTRICAL DISCONNECTS, MOTOR STARTERS, VARIABLE FREQUENCY DRIVES, CONTROLS, AND ELECTRICAL ACCESSORIES ARE FURNISHED AND/OR INSTALLED BY THE APPROPRIATE TRADE.

SITE ELEVATION:

A. EQUIPMENT SHALL BE SELECTED FOR THE PROJECT ELEVATION OF 3,413'.

mosaic
architecture-planning-design
317 Cruse Avenue Suite 201
Helena, Montana 59601
406.449.2013
www.mosaicarch.com

PROFESSIONAL ENGINEER LICENSED 22020 STATE OF IDAHO ROSS BALFOUR

06/26/2024

U.S. DEPARTMENT OF AGRICULTURE
FOREST SERVICE
R-1 NORTHERN REGION

Morrison Maierle
engineers · surveyors · planners · scientists
1 Engineer Place
Helena, MT 59602
406.442.3050
www.m-m.net

COPYRIGHT © MORRISON-MAIERLE, 2022

POWELL DUPLEX RENOVATION

LOCHSA-POWELL RANGER DISTRICT,
192 POWELL RD,
LOLO, ID 59847

CONSTRUCTION DOCUMENTS

MARK	DATE	REVISION

PROJECT NO.	1240LU23F0138
DATE:	7/19/2024
Drawn By:	MRR
Designed By:	JDB
Checked By:	LHP

PLUMBING LEGEND AND NOTES

SHEET: **P000**

DATESTAMP 7/17/2024 10:15:14 AM

PLUMBING FIXTURE SCHEDULE

REMARKS:
1. PROVIDE ALL FIXTURES WITH APPROPRIATE COMMERCIAL GRADE SUPPORTS/CARRIERS, P-TRAPS, STOP VALVES, BRAIDED FLEXIBLE SUPPLIES, UNDER FIXTURE PIPING INSULATION AND HAMMER ARRESTORS.
2. PROVIDE AND INSTALL TRAP PRIMERS FOR ALL FLOOR DRAINS AND FLOOR SINKS UNLESS OTHERWISE INDICATED.
3. INSTALL ALL TRAP PRIMERS IN RECESSED WALL MOUNTED BOXES IN AN ACCESSIBLE LOCATION.
4. FIELD COORDINATE INSTALLATION LOCATION OF TRAP PRIMER WALL BOXES, WATER CLOSETS, LAVATORIES, AND URINALS FOR ADA COMPLIANCY WITH ARCHITECT/ENGINEER.

MARK	FIXTURE						TRIM				ROUGH-IN SIZE (IN)				REMARKS
	DESCRIPTION	ADA	MANUF.	MODEL	MATERIAL / FINISH	MOUNTING / HEIGHT	DESCRIPTION	MANUF.	MODEL	MATERIAL / FINISH	WASTE	VENT	COLD	HOT	
WC-1	WATER CLOSET - FLOOR MOUNTED - TANK	NO	KOHLER	K-3978	VITREOUS CHINA	FLOOR / RIM 15"	OPEN FRONT ELONGATED TOILET SEAT	KOHLER	K-4670-C	POLYPROPYLENE	3"	2"	1/2"	- -	PROVIDE WITH QUARTER TURN CHROME ANGLE STOP, SUPPLY FLEX, CLOSET FLANGE, WAX RING, AND CLOSET BOLTS.

MEP COORDINATION SCHEDULE

CONTROL TYPE:

BAS	BUILDING AUTOMATION SYSTEM
CO	CARBON MONOXIDE DETECTOR
CONT	CONTINUOUS OPERATION
EF	INTERLOCK WITH EXHAUST FAN
HCP	HOOD CONTROL PANEL
INT	INTEGRAL
L	LIGHT SWITCH
MS	MANUAL SWITCH
OS	OCCUPANCY SENSOR
PS	PRESSURE SWITCH
T	THERMOSTAT
TC	TIME CLOCK
UC	UNIT CONTROLLER
VE	VEHICLE EXHAUST DETECTION
N/A	SYSTEM...

DISCONNECT/STARTER TYPE:

CB	PANELBOARD CIRCUIT BREAKER WITHIN SIGHT OF EQUIPMENT
CSFD	COMBINATION STARTER/DISCONNECT - HOA
FD	FUSED DISCONNECT
FST	FUSTAT
FW	FACTORY-WIRED SINGLE POINT CONNECTION
MOCP	MOTOR OVER-CURRENT PROTECTION
MSS	MANUAL STARTER SWITCH WITH THERMAL OVERLOADS (1-, 2- OR 3-POLE AS REQUIRED)
NFD	NON-FUSED DISCONNECT
RCPT	20A DUPLEX RECEPTACLE (GFCI PROTECTED AS REQUIRED), CORD AND PLUG
RVSS	REDUCED VOLTAGE SOLID-STATE
VFD	VARIABLE FREQUENCY DRIVE - HOA
N/A	NOT APPLICABLE

DIVISION OF RESPONSIBILITIES:

22/22	FURNISHED AND INSTALLED BY DIV. 22, WIRED BY DIV. 22
22/26	FURNISHED AND INSTALLED BY DIV. 22, WIRED BY DIV. 26
23/23	FURNISHED AND INSTALLED BY DIV. 23, WIRED BY DIV. 23
23/26	FURNISHED AND INSTALLED BY DIV. 23, WIRED BY DIV. 26
26/26	FURNISHED AND INSTALLED BY DIV. 26, WIRED BY DIV. 26

NOTES:
1. INTEGRAL DISCONNECTS AND OVERLOADS
2. INTEGRAL OVERLOADS
3. SINGLE POINT CONNECTION
4. PROVIDE RECEPTACLE AND DATA CONNECTION FOR PANEL
5. MOUNT ON UNI-STRUT IN FRONT OF UNIT
6. SIZE FUSES IN ACCORDANCE WITH MANUFACTURER'S GUIDELINES FOR INSTALLED EQUIPMENT
7. INTEGRAL VARIABLE FREQUENCY DRIVE
8. DUCT SMOKE DETECTOR(S) REQUIRED

GENERAL NOTES:
A. CONTROL WIRING SHALL BE CONCEALED WITHIN WALL CONSTRUCTION, ABOVE CEILING, OR RUN IN CONDUIT. EXPOSED CONTROL WIRING IS UNACCEPTABLE.
B. UNLESS SPECIFICALLY NOTED, ALL FEEDERS SHALL INCLUDE A FULL SIZE NEUTRAL. IT IS THE CONTRACTOR'S RESPONSIBILITY TO VERIFY WITH THE MANUFACTURER OF THE ACTUAL EQUIPMENT BEING SUPPLIED WHETHER A NEUTRAL IS
C. REQUIRED PRIOR TO ROUGH-IN.
ALL DUCT SMOKE DETECTORS FURNISHED BY DIV. 26, INSTALLED BY DIV. 23, AND WIRED BY DIV. 26. DIV. 26 SHALL WIRE ALL FANS TO SHUT DOWN WHEN ALARM IS INITIATED BY ANY DUCT SMOKE DETECTOR.

MARK	DESCRIPTION	ELECTRICAL DATA		CONTROL		NOTES	DISCONNECT / STARTER		DISCONNECT				FEEDER	
		LOAD	VOLT-PHASE	TYPE	DIV		TYPE	DIV	SIZE (NEMA)	SWITCH (AMPS)	FUSE (AMPS)	ENCLOSURE (NEMA)	COPPER WIRE (AWG)	CONDUIT (INCHES)
BB-1	ELECTRIC BASEBOARD	2000 W	240 - 1	T	23 / 26	3	FW	23/26	--	--	20	1	12	3/4
BB-2	ELECTRIC BASEBOARD	2000 W	240 - 1	T	23 / 26	3	FW	23/26	--	--	20	1	12	3/4

DATE/STAMP 7/17/2024 10:15:15 AM

mosaic
architecture-planning-design
317 Cruse Avenue Suite 201
Helena, Montana 59601
406.449.2013
www.mosaicarch.com

PROFESSIONAL ENGINEER LICENSED 22020 STATE OF IDAHO ROSS BALFOUR
06/26/2024

U.S. DEPARTMENT OF AGRICULTURE
FOREST SERVICE
R-1 NORTHERN REGION

Morrison Maierle
engineers · surveyors · planners · scientists
1 Engineer Place
Helena, MT 59602
406.442.3050
www.m-m.net

COPYRIGHT © MORRISON-MAIERLE, 2022

POWELL DUPLEX RENOVATION
LOCHSA-POWELL RANGER DISTRICT,
192 POWELL RD,
LOLO, ID 59847
CONSTRUCTION DOCUMENTS

MARK DATE REVISION

PROJECT NO. 1240LU23F0138
DATE: 7/19/2024
Drawn By: MRR
Designed By: JDB
Checked By: LHP

PLUMBING SCHEDULES

SHEET: **P001**



1 LEVEL 1 - PLUMBING DEMOLITION PLAN
3/16" = 1'-0"

PLUMBING DEMO NOTES

A. LOCATIONS AND DIMENSIONS OF EXISTING FACILITIES IDENTIFIED ON THIS DRAWING ARE APPROXIMATE AND REPRESENT THE BEST AVAILABLE INFORMATION BASED ON A COMBINATION OF FIELD INVESTIGATIONS AND VARIOUS DESIGN AND RECORD DRAWINGS AVAILABLE AT THE TIME OF DESIGN. FIELD VERIFY LOCATIONS AND DIMENSIONS PRIOR TO ORDERING EQUIPMENT AND DURING PERFORMANCE OF THE WORK. PROVIDE DEMOLITION WORK, NECESSARY FITTINGS, TRANSITIONS, AND OTHER COMPONENTS AS REQUIRED FOR A COMPLETE AND FUNCTIONAL INSTALLATION OF NEW SYSTEMS AT NO ADDITIONAL COST TO THE OWNER.
B. EXISTING PLUMBING EQUIPMENT, FIXTURES, AND PIPING SHOWN AS DARK AND DASHED SHALL BE DEMOLISHED. EXISTING PLUMBING EQUIPMENT, FIXTURES, AND PIPING SHOWN LIGHT SHALL REMAIN UNCHANGED.
C. THE PLUMBING CONTRACTOR SHALL COORDINATE SALVAGE OF REMOVED EQUIPMENT IN GOOD CONDITION WITH THE OWNER. THE PLUMBING CONTRACTOR SHALL DISPOSE OF UNWANTED EQUIPMENT.
D. COORDINATE WITH GENERAL CONTRACTOR TO PATCH AND REPAIR ROOF AND WALL ASSEMBLIES ASSOCIATED WITH PLUMBING DEMOLITION.
E. CONCRETE SLAB CUTTING REGIONS SHOWN ON DRAWINGS ARE APPROXIMATE AND MUST BE FIELD COORDINATED PRIOR TO THE CUTTING OF THE SLAB.
F. PROTECT EXISTING BUILDING ELEMENTS DURING DEMOLITION WORK. COORDINATE WITH OTHER TRADES TO ENSURE NO EXISTING EQUIPMENT/PIPING TO REMAIN IS DAMAGED DURING THE DEMOLITION WORK.

KEY NOTES:

1. INCLUDE WORK IN BID ALTERNATE. SEE ARCHITECTURAL FOR A COMPLETE SCOPE OF WORK FOR BID ALTERNATE.

mosaic
architecture-planning-design
317 Cruse Avenue Suite 201
Helena, Montana 59601
406.449.2013
www.mosaicarch.com

PROFESSIONAL ENGINEER LICENSED 22020 STATE OF IDAHO ROSS BALFOUR
06/26/2024

U.S. DEPARTMENT OF AGRICULTURE
FOREST SERVICE
R-1 NORTHERN REGION

Morrison Maierle
engineers · surveyors · planners · scientists
1 Engineer Place
Helena, MT 59602
406.442.3050
www.m-m.net

COPYRIGHT © MORRISON-MAIERLE, 2022

POWELL DUPLEX RENOVATION

LOCHSA-POWELL RANGER DISTRICT,
192 POWELL RD,
LOLO, ID 59847

CONSTRUCTION DOCUMENTS


MARK	DATE	REVISION

PROJECT NO. 1240L023F0138
DATE: 7/19/2024
Drawn By: MRR
Designed By: JDB
Checked By: LHP

LEVEL 1 PLUMBING DEMOLITION PLAN

SHEET: **P101**

DATESTAMP 7/17/2024 10:15:15 AM

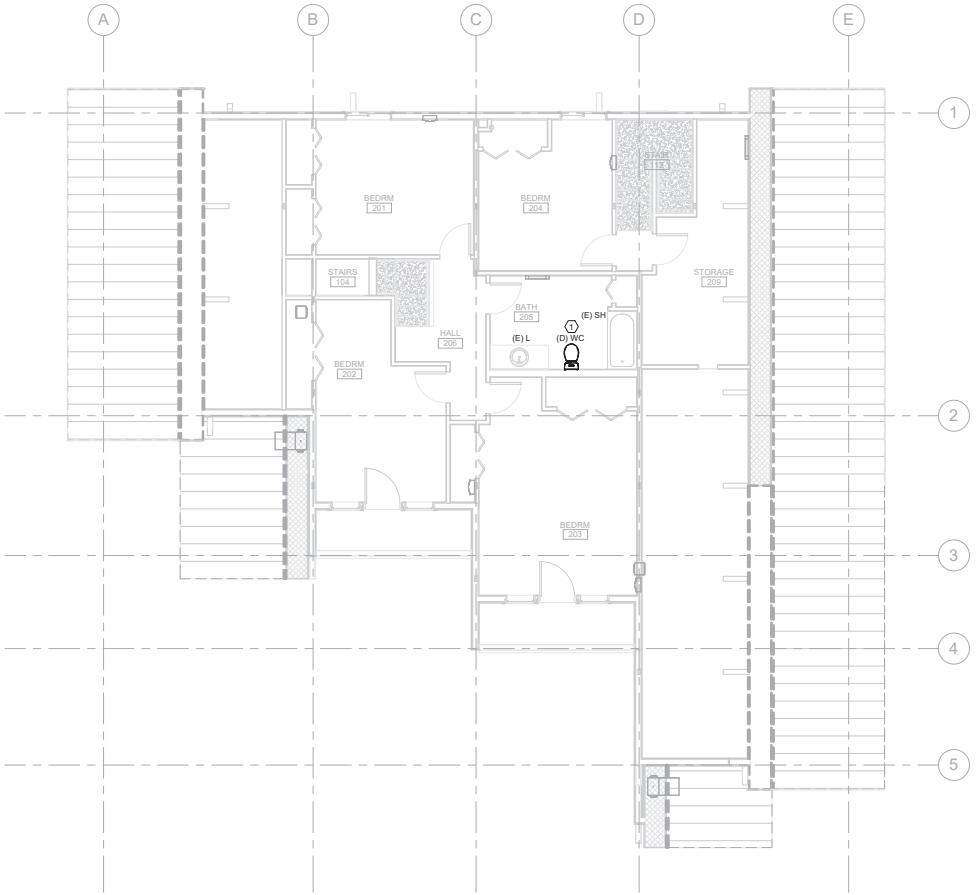

1 LEVEL 2 - PLUMBING DEMOLITION PLAN
3/16" = 1'-0"

PLUMBING DEMO NOTES

A. LOCATIONS AND DIMENSIONS OF EXISTING FACILITIES IDENTIFIED ON THIS DRAWING ARE APPROXIMATE AND REPRESENT THE BEST AVAILABLE INFORMATION BASED ON A COMBINATION OF FIELD INVESTIGATIONS AND VARIOUS DESIGN AND RECORD DRAWINGS AVAILABLE AT THE TIME OF DESIGN. FIELD VERIFY LOCATIONS AND DIMENSIONS PRIOR TO ORDERING EQUIPMENT AND DURING PERFORMANCE OF THE WORK. PROVIDE DEMOLITION WORK, NECESSARY FITTINGS, TRANSITIONS, AND OTHER COMPONENTS AS REQUIRED FOR A COMPLETE AND FUNCTIONAL INSTALLATION OF NEW SYSTEMS AT NO ADDITIONAL COST TO THE OWNER.
B. EXISTING PLUMBING EQUIPMENT, FIXTURES, AND PIPING SHOWN AS DARK AND DASHED SHALL BE DEMOLISHED. EXISTING PLUMBING EQUIPMENT, FIXTURES, AND PIPING SHOWN LIGHT SHALL REMAIN UNCHANGED.
C. THE PLUMBING CONTRACTOR SHALL COORDINATE SALVAGE OF REMOVED EQUIPMENT IN GOOD CONDITION WITH THE OWNER. THE PLUMBING CONTRACTOR SHALL DISPOSE OF UNWANTED EQUIPMENT.
D. COORDINATE WITH GENERAL CONTRACTOR TO PATCH AND REPAIR ROOF AND WALL ASSEMBLIES ASSOCIATED WITH PLUMBING DEMOLITION.
E. CONCRETE SLAB CUTTING REGIONS SHOWN ON DRAWINGS ARE APPROXIMATE AND MUST BE FIELD COORDINATED PRIOR TO THE CUTTING OF THE SLAB.
F. PROTECT EXISTING BUILDING ELEMENTS DURING DEMOLITION WORK. COORDINATE WITH OTHER TRADES TO ENSURE NO EXISTING EQUIPMENT/PIPING TO REMAIN IS DAMAGED DURING THE DEMOLITION WORK.

KEY NOTES:

1. INCLUDE WORK IN BID ALTERNATE. SEE ARCHITECTURAL FOR A COMPLETE SCOPE OF WORK FOR BID ALTERNATE.

mosaic
architecture-planning-design
317 Cruse Avenue Suite 201
Helena, Montana 59601
406.449.2013
www.mosaicarch.com

PROFESSIONAL ENGINEER LICENSED 22020 STATE OF IDAHO ROSS BALFOUR
06/26/2024

FOREST SERVICE U.S. DEPARTMENT OF AGRICULTURE

U.S. DEPARTMENT OF AGRICULTURE
FOREST SERVICE
R-1 NORTHERN REGION

Morrison Maierle
engineers · surveyors · planners · scientists
1 Engineer Place
Helena, MT 59602
406.442.3050
www.m-m.net

COPYRIGHT © MORRISON-MAIERLE, 2022

POWELL DUPLEX RENOVATION

LOCHSA-POWELL RANGER DISTRICT,
192 POWELL RD,
LOLO, ID 59847

CONSTRUCTION DOCUMENTS


MARK	DATE	REVISION

PROJECT NO. 1240LU23F0138
DATE: 7/19/2024
Drawn By: MRR
Designed By: JDB
Checked By: LHP

LEVEL 2 PLUMBING DEMOLITION PLAN

SHEET: **P102**

DATESTAMP 7/17/2024 10:15:16 AM

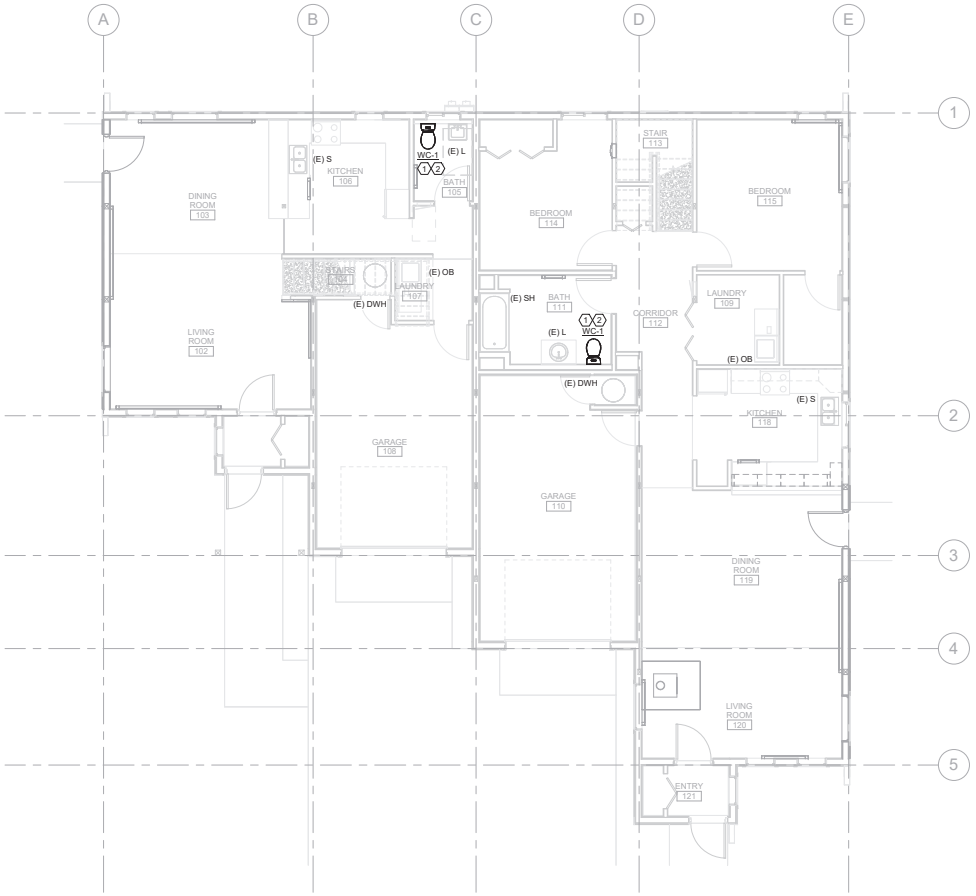

1 LEVEL 1 - PLUMBING PLAN
3/16" = 1'-0"

PLUMBING PLAN NOTES

A. PROVIDE ACCESS DOORS TO ALLOW SERVICE AND INSPECTION OF EQUIPMENT, VALVES, AND OTHER DEVICES INSTALLED ABOVE NON-REMOVABLE CEILINGS. COORDINATE SUCH INSTALLATIONS WITH ARCHITECT AND ENGINEER.
B. PROVIDE TRAP SEALS AND TRAP PRIMERS FOR FLOOR DRAINS, FLOOR SINKS, AND OTHER FLOOR RECEPTORS.
C. INSTALL ACCESSIBLE PLUMBING FIXTURES IN COMPLIANCE WITH ABA REQUIREMENTS. INSULATE EXPOSED PIPING BELOW ADA ACCESSIBLE FIXTURES.
D. INSTALL FLOOR DRAIN STRAINERS AND CLEANOUT COVERS FLUSH AND LEVEL WITH FINISHED FLOOR.
E. PIPING SHALL BE IDENTIFIED WITH PIPE LABELS MARKED AT A MAXIMUM OF EVERY 25 FT. VALVES SHALL BE IDENTIFIED WITH BRASS OR ALUMINUM VALVE TAGS.
F. PROVIDE AND INSTALL PIPE GUIDES, EXPANSION JOINTS, AND HANGERS PER MANUFACTURER'S RECOMMENDATIONS.
G. PIPING WALL PENETRATIONS SHALL BE FINISHED WITH A CHROME ESCUTCHEON PLATE.
H. MAINTAIN THE INTEGRITY OF DRAFTSTOPPING WHERE PIPES PENETRATE DRAFTSTOPPING MATERIALS.
I. NO FITTINGS OR PIPING CONNECTIONS SHALL BE INSTALLED UNDERSLAB.
J. GAS PIPING IS TO BE WELDED IN CONCEALED SPACES.
K. REFER TO THE PLUMBING FIXTURE SCHEDULE FOR PIPE SIZES TO INDIVIDUAL FIXTURES.
L. COORDINATE CONCRETE PENETRATIONS WITH STRUCTURAL DRAWINGS TO VERIFY HOW AND WHERE CONCRETE CAN BE CUT.
M. EXPOSED PIPING SHALL BE PAINTED PER ARCHITECTURAL OR PROVIDED WITH A PVC COATED JACKET IN THE COLOR OF THE ARCHITECT'S CHOOSING. CONTRACTOR TO CLEAN AND DRY PIPING PRIOR TO PAINTING.
N. SANITARY SEWER, RAINWATER, AND OTHER DRAIN PIPING SHALL BE INSTALLED AT A MINIMUM 1/4" PER FOOT (2%) SLOPE IN DIRECTION OF FLOW. UNLESS OTHERWISE INDICATED ON THE DRAWINGS.

KEY NOTES:

1. INCLUDE WORK IN BID ALTERNATE. SEE ARCHITECTURAL FOR A COMPLETE SCOPE OF WORK FOR BID ALTERNATE.
2. CONNECT NEW FIXTURE TO EXISTING SERVICES.

mosaic
architecture-planning-design
317 Cruse Avenue Suite 201
Helena, Montana 59601
406.449.2013
www.mosaicarch.com

PROFESSIONAL ENGINEER LICENSED 22020 STATE OF IDAHO ROSS BALFOUR
06/26/2024

U.S. DEPARTMENT OF AGRICULTURE
FOREST SERVICE
R-1 NORTHERN REGION

Morrison Maierle
engineers · surveyors · planners · scientists
1 Engineer Place
Helena, MT 59602
406.442.3050
www.m-m.net

COPYRIGHT © MORRISON-MAIERLE, 2022

POWELL DUPLEX RENOVATION

LOCHSA-POWELL RANGER DISTRICT,
192 POWELL RD,
LOLO, ID 59847

CONSTRUCTION DOCUMENTS


MARK	DATE	REVISION

PROJECT NO. 1240LU23F0138
DATE: 7/19/2024
Drawn By: MRR
Designed By: JDB
Checked By: LHP

LEVEL 1 PLUMBING PLAN

SHEET: P201

DATESTAMP 7/17/2024 10:15:16 AM

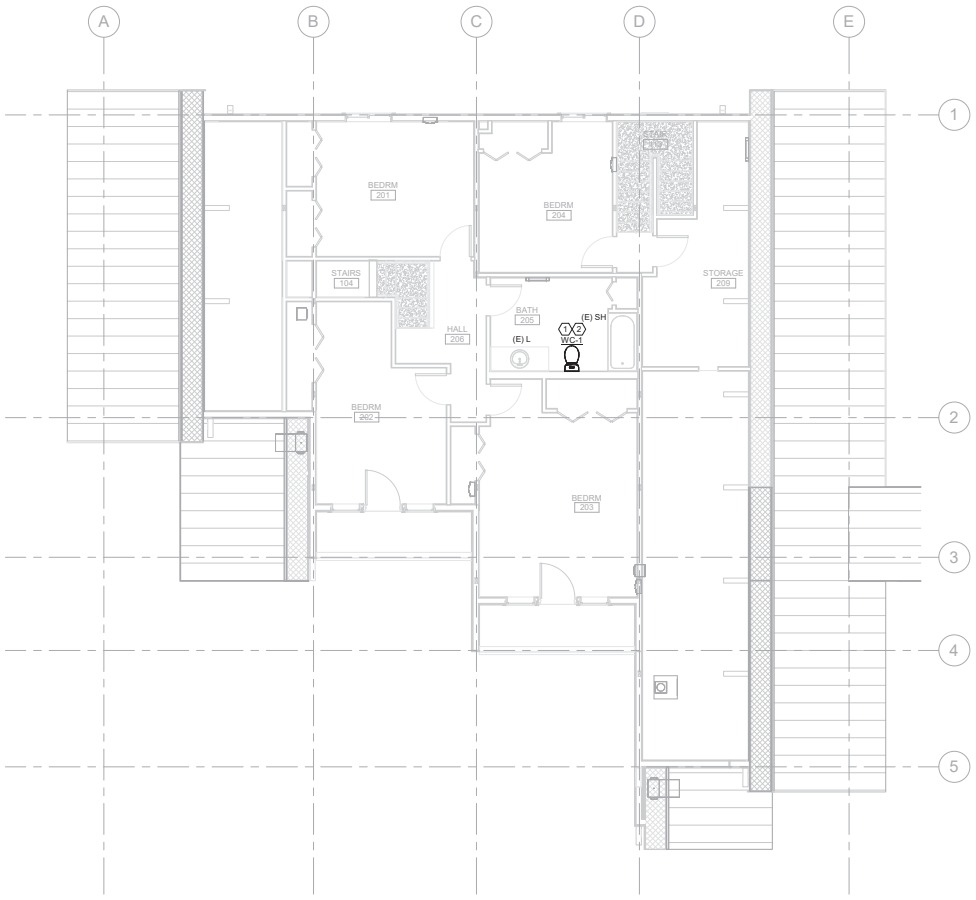

1 LEVEL 2 - PLUMBING PLAN
3/16" = 1'-0"

PLUMBING PLAN NOTES

A. PROVIDE ACCESS DOORS TO ALLOW SERVICE AND INSPECTION OF EQUIPMENT, VALVES, AND OTHER DEVICES INSTALLED ABOVE NON-REMOVABLE CEILINGS. COORDINATE SUCH INSTALLATIONS WITH ARCHITECT AND ENGINEER.
B. PROVIDE TRAP SEALS AND TRAP PRIMERS FOR FLOOR DRAINS, FLOOR SINKS, AND OTHER FLOOR RECEPTORS.
C. INSTALL ACCESSIBLE PLUMBING FIXTURES IN COMPLIANCE WITH ABA REQUIREMENTS. INSULATE EXPOSED PIPING BELOW ADA ACCESSIBLE FIXTURES.
D. INSTALL FLOOR DRAIN STRAINERS AND CLEANOUT COVERS FLUSH AND LEVEL WITH FINISHED FLOOR.
E. PIPING SHALL BE IDENTIFIED WITH PIPE LABELS MARKED AT A MAXIMUM OF EVERY 25 FT. VALVES SHALL BE IDENTIFIED WITH BRASS OR ALUMINUM VALVE TAGS.
F. PROVIDE AND INSTALL PIPE GUIDES, EXPANSION JOINTS, AND HANGERS PER MANUFACTURER'S RECOMMENDATIONS.
G. PIPING WALL PENETRATIONS SHALL BE FINISHED WITH A CHROME ESCUTCHEON PLATE.
H. MAINTAIN THE INTEGRITY OF DRAFTSTOPPING WHERE PIPES PENETRATE DRAFTSTOPPING MATERIALS.
I. NO FITTINGS OR PIPING CONNECTIONS SHALL BE INSTALLED UNDERSLAB.
J. GAS PIPING IS TO BE WELDED IN CONCEALED SPACES.
K. REFER TO THE PLUMBING FIXTURE SCHEDULE FOR PIPE SIZES TO INDIVIDUAL FIXTURES.
L. COORDINATE CONCRETE PENETRATIONS WITH STRUCTURAL DRAWINGS TO VERIFY HOW AND WHERE CONCRETE CAN BE CUT.
M. EXPOSED PIPING SHALL BE PAINTED PER ARCHITECTURAL OR PROVIDED WITH A PVC COATED JACKET IN THE COLOR OF THE ARCHITECT'S CHOOSING. CONTRACTOR TO CLEAN AND DRY PIPING PRIOR TO PAINTING.
N. SANITARY SEWER, RAINWATER, AND OTHER DRAIN PIPING SHALL BE INSTALLED AT A MINIMUM 1/4" PER FOOT (2%) SLOPE IN DIRECTION OF FLOW. UNLESS OTHERWISE INDICATED ON THE DRAWINGS.

KEY NOTES:

1. INCLUDE WORK IN BID ALTERNATE. SEE ARCHITECTURAL FOR A COMPLETE SCOPE OF WORK FOR BID ALTERNATE.
2. CONNECT NEW FIXTURE TO EXISTING SERVICES.

mosaic
architecture-planning-design
317 Cruse Avenue Suite 201
Helena, Montana 59601
406.449.2013
www.mosaicarch.com

PROFESSIONAL ENGINEER LICENSED 22020 STATE OF IDAHO ROSS BALFOUR

06/26/2024

U.S. DEPARTMENT OF AGRICULTURE
FOREST SERVICE
R-1 NORTHERN REGION

Morrison Maierle
engineers · surveyors · planners · scientists
1 Engineer Place
Helena, MT 59602
406.442.3050
www.m-m.net

COPYRIGHT © MORRISON-MAIERLE, 2022

POWELL DUPLEX RENOVATION

LOCHSA-POWELL RANGER DISTRICT,
192 POWELL RD,
LOLO, ID 59847

CONSTRUCTION DOCUMENTS

MARK	DATE	REVISION

PROJECT NO. 1240LU23F0138
DATE: 7/19/2024
Drawn By: MRR
Designed By: JDB
Checked By: LHP

LEVEL 2 PLUMBING PLAN

SHEET: P202

DATESTAMP 7/17/2024 10:15:17 AM

ELECTRICAL ABBREVIATIONS LEGEND

A, AMP	AMPERES
AC	ALTERNATING CURRENT
A/C	AIR CONDITIONING
AF	AMP FUSE
AFC	AVAILABLE FAULT CURRENT
AFCI	ARC FAULT CIRCUIT INTERRUPTER
AFF	ABOVE FINISHED FLOOR
AFG	ABOVE FINISHED GRADE
AHU	AIR HANDLING UNIT
AL	ALUMINUM
AS	AMP SWITCH
ATS	AUTOMATIC TRANSFER SWITCH
BAS	BUILDING AUTOMATION SYSTEM
BKR	BREAKER
BOF	BOTTOM OF FIXTURE
C	RACEWAY/CONDUIT
CB	CIRCUIT BREAKER
CCT	COLOR RENDERING TEMPERATURE
CCTV	CLOSED CIRCUIT TELEVISION
CKT	CIRCUIT
CLG	CEILING
C.O.	CONTRACTING OFFICER
CO	RACEWAY/CONDUIT ONLY, WITH PULL STRING
COD	CENTER OF DEVICE
CNTRL	CONTROL
CU	COPPER
(D)	EXISTING TO BE DEMOLISHED
DISC	DISCONNECT
DIST	DISTRIBUTION
DPDT	DOUBLE POLE DOUBLE THROW
DWG	DRAWING
EA	EACH
EC	ELECTRICAL CONTRACTOR
EF	EXHAUST FAN
ELEC	ELECTRIC
EMT	ELECTRICAL METALLIC TUBING
EQUIP	EQUIPMENT
EX, EXIST	EXISTING
FA	FIRE ALARM
FAA	FIRE ALARM ANNUNCIATOR
FACP	FIRE ALARM CONTROL PANEL
FD	FUSED DISCONNECT
FLR	FLOOR
FO	FIBER OPTIC
FSD	FIRE SMOKE DAMPER RELAY, CONTROLLED BY ASSOCIATED SMOKE DETECTOR AND CIRCUITED BACK TO FACP
FVNR	FULL VOLTAGE NON-REVERSING
FVR	FULL VOLTAGE REVERSING
GEC	GROUNDED ELECTRODE CONDUCTOR
GFCI	GROUND FAULT CIRCUIT INTERRUPTER
GFI	GROUND FAULT INTERRUPTER
GFP	GROUND FAULT PROTECTION
GND	GROUND
GRC	GALVANIZED RIGID CONDUIT
HID	HIGH INTENSITY DISCHARGE
HOA	HAND-OFF-AUTOMATIC
HP	HORSEPOWER
HPS	HIGH PRESSURE SODIUM
HTR	HEATER
HVAC	HEATING, VENTILATION & AIR CONDITIONING
HZ	HERTZ
J-BOX	JUNCTION BOX
KVA	KILOVOLT-AMPERES
KW	KILOWATTS
LCP	LIGHTING CONTROL PANEL
LPW	LUMENS PER WATT
LTG	LIGHTING
LM	LUMENS
LV	LOW VOLTAGE
MAG	MAGNETIC STARTER
MAN	MANUAL
MAX	MAXIMUM
MC	MECHANICAL CONTRACTOR
MCA	MINIMUM CIRCUIT AMPACITY
MCC	MOTOR CONTROL CENTER
MDP	MAIN DISTRIBUTION PANEL
MECH	MECHANICAL
MEP	MECHANICAL, ELECTRICAL, PLUMBING
MH	METAL HALIDE
MIN	MINIMUM
MSS	MOTOR STARTER SWITCH WITH THERMAL OVERLOADS
N	NEUTRAL
NC	NORMALLY CLOSED
NEC	NATIONAL ELECTRIC CODE
NEMA	NATIONAL ELECTRICAL MANUFACTURERS ASSOCIATION
NFD	NON-FUSED DISCONNECT
NL	NIGHT LIGHT, UN-SWITCHED 24/7 OPERATION
NIC	NOT IN CONTRACT
NO	NORMALLY OPEN
#	NUMBER
OAE	OR APPROVED EQUAL
OC	ON CENTER
OCPD	OVERCURRENT PROTECTIVE DEVICE
OH	OVERHEAD
P	POLE
PB	PUSHBUTTON
PC	PLUMBING CONTRACTOR
PH	PHASE
PNL	PANEL
PVC	POLYVINYL CHLORIDE CONDUIT
PWR	POWER
(R)	EXISTING TO REMAIN
RCPT	RECEPTACLE
RECEPT	RECEPTACLE
RGS	RIGID GALVANIZED STEEL
RM	ROOM
RVNR	REDUCED VOLTAGE NON-REVERSING
RVR	REDUCED VOLTAGE REVERSING
SP	SINGLE POLE TOGGLE SWITCH
SPD	SURGE PROTECTIVE DEVICE (TVSS)
SPEC	SPECIFICATION
SPST	SINGLE POLE SINGLE THROW
SSPB	START-STOP PUSHBUTTON
SW	SWITCH
SWBD	SWITCHBOARD
SWGR	SWITCHGEAR
TB	TELEPHONE BOARD
TC	TIME CLOCK
TD	TIME DELAY
TEL	TELEPHONE
TR	TAMPER RESISTANT
TSP	TWISTED SHIELDED PAIR
TTB	TELEPHONE TERMINAL BOARD
TYP	TYPICAL
UG	UNDERGROUND
UH	UNIT HEATER
UNO	UNLESS NOTED OTHERWISE
V	VOLT
VA	VOLT-AMPERES
VFD	VARIABLE FREQUENCY DRIVE
W	WATTS
WAO	WORK AREA OUTLET
WP	WEATHERPROOF
W/O	WITHOUT
XFMR	TRANSFORMER
Y	WYE-CONNECTED
Δ	DELTA-CONNECTED
ø	PHASE

ELECTRICAL LIGHTING FIXTURE LEGEND

- RECESSED LED FIXTURE - "a" & "b" DESIGNATES SWITCH
- RECESSED EMERGENCY LED FIXTURE - "a" & "b" DESIGNATES SWITCH
- SURFACE LED FIXTURE - "a" & "b" DESIGNATES SWITCH
- SURFACE EMERGENCY LED FIXTURE - "a" & "b" DESIGNATES SWITCH
- SURFACE WALL MOUNT LED FIXTURE
- LED STRIP OR INDUSTRIAL, SURFACE OR CHAIN HUNG
- EMERGENCY LED STRIP OR INDUSTRIAL, SURFACE OR CHAIN HUNG
- POLE MOUNTED FIXTURE
- LIGHTED BOLLARD
- PENDANT FIXTURE; HIGH BAY, LOW BAY, DECORATIVE
- EXIT SIGN - WALL MOUNT, CEILING MOUNT. ARROW INDICATES DIRECTION OF TRAVEL, SHADING INDICATES LIGHTED FACE.
- COMBINATION EXIT SIGN/ EGRESS LIGHTING UNIT - WALL MOUNT, CEILING MOUNT. ARROW INDICATES DIRECTION OF TRAVEL, SHADING INDICATES LIGHTED FACE.
- DUAL HEAD EMERGENCY EGRESS BATTERY PACK, WALL MOUNT OR CEILING MOUNT
- WALL MOUNTED SCONCE
- SURFACE DOWNLIGHT
- SURFACE EMERGENCY DOWNLIGHT
- RECESSED CAN DOWNLIGHT
- RECESSED CAN EMERGENCY DOWNLIGHT
- RECESSED CAN WALL WASHER
- TRACK LIGHTING. SEE FIXTURE SCHEDULE AND LIGHTING PLANS.

ELECTRICAL ONE-LINE LEGEND

- CT AND CUSTOMER POWER METER
- MOTOR
- UTILITY ELECTRIC METER AND BASE (BASE BY CUSTOMER)
- SURGE PROTECTION DEVICE
- LIGHTNING ARRESTER, TYPE 1 SPD, MOUNTED ON EXTERIOR OF MAIN SWITCHGEAR (SQUARE D. SDSA SERIES, OAE)
- STRESS RELIEF CONE
- PFC POWER FACTOR CORRECTION CAPACITOR
- $_X EQUIPMENT TOGGLE DISCONNECT SWITCH
  "X" INDICATES TYPE:
  F - FUSTAT
  M - MOTOR STARTER SWITCH W/ THERMAL OVERLOADS
- CONTACTOR NORMALLY OPEN, NORMALLY CLOSED
- TRANSFORMER, 3-PH, 3-WIRE DELTA CONNECTION
- TRANSFORMER, 3-PH, 4-WIRE GROUNDED WYE CONNECTION
- AUTOMATIC TRANSFER SWITCH
- VFD VARIABLE FREQUENCY DRIVE
- FIXED MOUNT LV BREAKER
- FUSED SWITCH ("XXAS/XXAF" - SW AND FUSE AMP RATING)
- GENERATOR
- CB WALL MOUNTED BREAKER
- THERMAL OVERLOAD ELEMENT
- DISCONNECT SWITCH ("XXAS" = SWITCH AMP RATING)
- FUSED DISCONNECT SWITCH ("XXAS/XXAF" = SW AND FUSE AMP RATING)
- COMBINATION MOTOR STARTER (STR SIZE, TYP, AS, AF, SEE MEP COORDINATION SCHEDULE)
- SWITCHBOARD OR PANELBOARD; NAME, VOLTAGE, PHASE, NUMBER OF WIRES WHEN INDICATED

ELECTRICAL POWER LEGEND

- D-1 ^{X} PANEL AND CIRCUIT DESIGNATION ARE NEXT TO EACH DEVICE (PANEL NAME - CIRCUIT NUMBER). MINIMUM BRANCH CIRCUIT WIRE SIZE IS #12, UNO. A SINGLE INSULATED GREEN GROUND CONDUCTOR SHALL BE PROVIDED WITH EACH HOME RUN. PROVIDE A SEPARATE NEUTRAL FOR EACH CIRCUIT. HOME RUNS SHALL HAVE NO MORE THAN THREE CIRCUITS. LINE VOLTAGE AND LOW VOLTAGE WIRING IS NOT SHOWN ON PLANS.
  "X" INDICATES TYPE:
  C - AUTOMATIC CONTROL
  GFI - GROUND FAULT INTERRUPTER
  WP - WEATHERPROOF WHILE-IN-USE COVER
  U - PROVIDE WITH (2) USB PORTS
  TR - TAMPER RESISTANT
- SIMPLEX RECEPTACLE - CEILING MOUNT, WALL MOUNT (+18", UNO)
- DUPLEX RECEPTACLE - CEILING MOUNT, WALL MOUNT (+18", UNO)
- QUADRUPLEX RECEPTACLE - CEILING MOUNT, WALL MOUNT (+18", UNO)
- ABOVE COUNTER RECEPTACLE - MOUNT AT +4" ABOVE BACKSPLASH
- $_X FLOOR BOX WITH (2) DUPLEX RECEPTACLES - FURNISH WITH (1) 3/4" MIN. CONDUIT FOR POWER FROM BOX. INCLUDE ALL HARDWARE/ACCESSORIES AS REQUIRED FOR COMPLETE INSTALLATION. PROVIDE COVER (COORDINATE WITH C.O. FOR FLOORING TYPE AND FINISH).
  "X" INDICATES TYPE:
  A - 4-GANG FLOOR BOX, CORROSION RESISTANT COATING FOR CONCRETE FLOORS (3" MIN. POUR DEPTH), (HUBBELL NO. CFB4G30CR, OAE)
  B - 4-GANG FLOOR BOX FOR RAISED ACCESS FLOORS, (HUBBELL NO. AFB4G50, OAE)
  C - FIRE RATED POKE-THROUGH FLOOR BOX FOR ELEVATED CONCRETE SLABS, 3" DIA. CORE (HUBBELL NO. PT7FSD, OAE)
  D - 8" DIA., FIRE RATED POKE-THROUGH FLOOR BOX FOR ELEVATED CONCRETE* SLABS, (HUBBELL NO. S1R8PTFIT1, OAE)
  E - FLUSH, ROUND SINGLE SERVICE FLOOR BOX FOR CONCRETE* FLOORS, UP TO 1" CONDUIT FEED (HUBBELL NO. B2506, OAE)
  F - TOMBSTONE PEDESTAL FLOOR BOX, 1" CONDUIT FEED (HUBBELL NO. 6301, OAE)
  *POKE-THROUGH FLOOR BOXES CAN ALSO BE USED FOR TILE, CARPET, OR WOOD FLOORS.
- FLOOR BOX WITH ADDITIONAL C.O. FOR DATA. FURNISH (1) 1-1/4" DEDICATED CONDUIT FROM EACH DATA COMPARTMENT, COMPLETE WITH PULL STRINGS OVER TO AND UP WALL INTO ACCESSIBLE CEILING SPACE, UNO.
- PANELBOARD OR LOAD CENTER
- SPECIAL PURPOSE RECEPTACLE (MOUNT AT +18", UNO)
  "X" INDICATES TYPE:
  A - NEMA 5-20R, #12 CU; B - NEMA 5-30R, #10 CU;
  C - NEMA 5-50R, #6 CU; D - NEMA 6-20R, #12 CU;
  E - NEMA 6-30R, #10 CU; F - NEMA 6-50R, #6 CU;
  G - NEMA 14-20R, #12 CU; H - NEMA 14-30R, #10 CU;
  I - NEMA 14-50R, #6 CU*
  * +4" AFF FOR RANGE
- PUSHBUTTON (MOUNT AT +48", UNO)
  "X" INDICATES TYPE:
  EPO - EMERGENCY POWER OFF
  ADA - HANDICAPPED ACCESSIBLE DOOR (DEVICE BY OTHERS)
  ODO - OVERHEAD DOOR OPERATOR (DEVICE BY OTHERS)
- RECESSED TV BOX, WITH BLANK COVERS FOR LOW VOLTAGE OPENINGS. MOUNT AT +72", UNO.
  X INDICATES TYPE:
  A - 2-GANG, WITH DUPLEX RECEPTACLE & SINGLE GANG DATA OPENING, HUBBELL RACO NSAV62M, WITH NSAV6C COVER
  B - 3-GANG, WITH DUPLEX RECEPTACLE, LOW VOLTAGE DIVIDER, SINGLE GANG FOR DATA (CENTER), AND REMOVABLE SINGLE GANG FOR AUDIO/VISUAL (SIDE). ARLINGTON TVBS507
  NOTE: ROUTE (1) 1" C. TO DATA OPENING AND (1) 1-1/4"C. TO AUDIO/VISUAL OPENING, FROM TOP OF GANG IN WALL INTO ACCESSIBLE CEILING SPACE. ALSO ROUTE 1-1/4" C. FROM AUDIO/VISUAL OPENING TO FLOOR BOX WHERE APPLICABLE.
- JUNCTION BOX
- DROP-DOWN RECEPTACLE
- PS-X SURFACE MOUNTED PLUGSTRIP
  "X" INDICATES TYPE:
  A - PLUGSTRIP, POWER ONLY, OUTLET EVERY 3' OC
  B - WIREMOLD SERIES 4000 POWER AND DATA
  C - WIREMOLD SERIES 5000 POWER AND DATA
- SURFACE MOUNTED RACEWAY
- RACEWAY CONCEALED IN WALL, FLOOR, OR CEILING IN FINISHED SPACES, EXPOSED IN UNFINISHED SPACES
- RACEWAY BELOW FLOOR OR BELOW GRADE
- RACEWAY STUB-OUT WITH CAPPED END
- RACEWAY STUB-OUT WITH BRUSHED END
- GROUNDING BUS

ABBREVIATIONS AND SYMBOLS GENERAL NOTES

A. THE ABBREVIATIONS ON THIS SHEET COMPRISE A STANDARD LIST; NOT ALL ABBREVIATIONS APPEAR ON THIS PROJECT.
B. THE SYMBOLS ON THIS SHEET COMPRISE A STANDARD LIST; NOT ALL SYMBOLS APPEAR ON THIS PROJECT.
C. ALL MOUNTING HEIGHTS ARE TO CENTER OF DEVICE ABOVE FINISHED FLOOR, UNLESS NOTED OTHERWISE. ELECTRICAL CONTRACTOR SHALL COORDINATE WITH OTHER CONTRACTORS, MAKING ADJUSTMENTS AS REQUIRED TO AVOID INTERFERENCE WITH EQUIPMENT SUCH AS BASEBOARD FIN-TUBE, CABINET UNIT HEATERS, ETC. C.O. SHALL BE NOTIFIED OF ALL SUCH HEIGHT ADJUSTMENTS. MOUNTING HEIGHTS INDICATED ON ARCHITECTURAL WALL ELEVATIONS OR AS NOTED SPECIFICALLY ON THE DRAWINGS OR IN THE SPECIFICATIONS SHALL TAKE PRECEDENCE OVER MOUNTING HEIGHTS LISTED.

ELECTRICAL PROJECT GENERAL NOTES

A. PRIOR TO BID CONTRACTOR SHALL VISIT THE SITE. NOT ALL WORK REQUIRED TO COMPLETE THE PROJECT IS SHOWN ON THE DRAWINGS. THE CONTRACTOR SHALL BECOME THOROUGHLY FAMILIAR WITH ALL THE WORK REQUIRED TO COMPLETE THE PROJECT IN ADDITION TO THE LOCAL CONDITIONS AND INCLUDE SAID WORK IN THE BID.
B. THE CONTRACTOR SHALL BE RESPONSIBLE FOR THE COORDINATION OF ALL ELECTRICAL SERVICE WORK WITH UTILITY. C.O. PAYS ALL FEES. CONTRACTOR DOES ALL SCHEDULING AND COORDINATION OF WORK. IT IS THE SOLE RESPONSIBILITY OF THE CONTRACTOR TO ENSURE ALL SCHEDULES ARE MET.
C. GENERAL WORK PRACTICES FOR ELECTRICAL CONSTRUCTION SHALL BE IN ACCORDANCE WITH NECA 1, "STANDARD PRACTICES FOR GOOD WORKMANSHIP IN ELECTRICAL CONTRACTING." THIS PUBLICATION IS AVAILABLE FROM NECA BY TELEPHONE AT 301-657-3110 OR ON-LINE AT WWW.NECANET.ORG.
D. IT IS THE CONTRACTORS RESPONSIBILITY TO COORDINATE WITH MECHANICAL FOR PLENUM SPACES AND PROVIDE PLENUM RATED CABLES WHERE REQUIRED FOR LIGHTING CONTROL, DATA, FIRE ALARM AND ALL OTHER L.V. SYSTEMS NOT INSTALLED IN CONDUIT. VERIFY CONDUIT REQUIREMENTS ON DRAWINGS AND SPECIFICATIONS.
E. FIRE-RESISTANCE: PROVIDE A MINIMUM HORIZONTAL DISTANCE OF 24" BETWEEN OUTLET BOXES LOCATED ON OPPOSITE SIDES OF FIRE-RESISTANCE RATED WALLS. WHERE THIS IS NOT POSSIBLE INSTALL UL LISTED PUTTY PADS ON ALL OUTLET BOXES NOT MEETING THE 24" SEPARATION. PROVIDE A UL LISTED THROUGH -PENETRATION FIRESTOP FOR PENETRATIONS OF FIRE-RESISTANCE RATED ASSEMBLIES.
F. CONDUCTORS ARE SIZED PER THE 75 DEGREE C RATING COLUMN OF NEC TABLE 310.16. IF THE TERMINAL USED FOR A TERMINATION OF A PARTICULAR CONDUCTOR IS NOT MARKED, OR THE TERMINAL IS MARKED FOR 60 DEGREE C CONDUCTORS, IT IS THE RESPONSIBILITY OF THE CONTRACTOR TO EITHER ADJUST THE AMPACITY OF THE CONDUCTOR TO MATCH THE 60 DEGREE COLUMN OF TABLE 310.16, OR REPLACE THE TERMINAL WITH ONE RATED FOR AT LEAST 75 DEGREES C.
G. BASED ON ACTUAL HOMERUN LENGTHS REQUIRED IN THE FIELD, THE CONTRACTOR SHALL CALCULATE AND INCREASE THE WIRE SIZES AS REQUIRED TO LIMIT BRANCH CIRCUIT VOLTAGE DROP TO 3%. FOR 20A BRANCH CIRCUITS THE MINIMUM CONDUCTOR SIZES SHALL BE AS FOLLOWS: #10 AWG CU FOR RUNS BETWEEN 100 AND 200 LINEAR FEET, #8 AWG CU FOR RUNS BETWEEN 200 AND 325 LINEAR FEET, AND AS CALCULATED BY THE CONTRACTOR FOR CIRCUITS EXTENDING BEYOND 325 LINEAR FEET. IN ALL CASES WHERE WIRE SIZES INCREASE, THE CONTRACTOR SHALL PROVIDE LARGER CONDUITS AS REQUIRED.
H. PROVIDE A DEDICATED NEUTRAL CONDUCTOR FOR EACH 120V BRANCH CIRCUIT.

ELECTRICAL PROJECT DEMO NOTES

A. DURING DEMOLITION, THE CONTRACTOR SHALL NOTE ALL EXISTING RACEWAY (BOTH SURFACE AND CONCEALED) TO THE EXTENT POSSIBLE. THESE RACEWAYS SHALL BE REUSED TO THE GREATEST EXTENT POSSIBLE TO INSURE A CLEAN FINISHED PRODUCT. WHERE PRACTICAL, AND ALLOWED PER CODE, FISHING THROUGH WALLS WITH MC CABLE IS PREFERRED TO SURFACE-MOUNTED CONDUIT.
B. CONTRACTOR SHALL REMOVE, TRANSPORT, AND LEGALLY DISPOSE OF LAMPS AND BALLASTS OFF-SITE. IT IS ASSUMED THAT THE BALLASTS DO NOT CONTAIN PCBs. THE CONTRACTOR SHALL NOTIFY THE C.O. IMMEDIATELY IF IT IS SUSPECTED THAT BALLASTS CONTAIN PCBs.
C. ALL POWER INTERRUPTIONS SHALL BE COORDINATED WITH C.O. ANY DISRUPTION OF WORKERS IN THE SPACE SHALL BE KEPT TO A MINIMUM AND BE COORDINATED WITH THE C.O. PRIOR TO WORK COMMENCING IN THAT SPACE.
D. CONTRACTOR SHALL EXTEND UNSWITCHED HOT LEG FROM EXISTING EMERGENCY FIXTURE LOCATION TO NEW EMERGENCY FIXTURES, AS NEEDED. SEE DEMO PLANS FOR AN APPROXIMATION OF EXISTING EMERGENCY FIXTURE LOCATIONS. FIELD VERIFY EXACT LOCATION PRIOR TO BID.
E. ELECTRICAL CONTRACTOR SHALL BE RESPONSIBLE FOR REPAIR OF ANY EXISTING CONDUIT OR FEEDER CIRCUITS THAT ARE INTENDED TO REMAIN THAT ARE SAW-CUT, OR OTHERWISE DAMAGED, AS PART OF THE DEMOLITION PROCESS. PROVISION FOR THIS WORK SHALL INCLUDE, BUT NOT BE LIMITED TO: ALL NECESSARY CONDUIT AND CONDUCTORS, MOUNTING ACCESSORIES AND LABOR, TO RESTORE THE SYSTEM TO ITS INTENDED FUNCTION.
F. ELECTRICAL DRAWINGS SHOWING EXISTING BUILDING CONDITIONS, SUCH AS DEMOLITION DRAWINGS, EXISTING PANEL SCHEDULES, ETC ARE BASED ON RECORD DRAWINGS AND SITE VISITS. IF ACTUAL EXISTING CONDITIONS DIFFER FROM THOSE SHOWN ON DRAWINGS, PLEASE NOTIFY C.O..

ELECTRICAL LIGHTING CONTROL LEGEND

STANDARD LIGHTING CONTROLS: SWITCHES AND LINE VOLTAGE DIMMERS	DIGITAL LIGHTING CONTROLS: ROOM CONTROLLERS AND LOW VOLTAGE DEVICES
$_X TOGGLE SWITCH (MOUNT AT +48", UNO) "X" INDICATES TYPE: BLANK - SINGLE POLE 3 - INDICATES THREE-WAY 4 - INDICATES FOUR-WAY D - INDICATES DIMMER SWITCH PHILIPS SUNRISE - ON/OFF K - INDICATES KEYED SWITCH T - INDICATES TIMER P - INDICATES PILOT LIGHT OS - INDICATES WALL SWITCH OCC SENSOR WATTSTOPPER DW100 (SINGLE OR DUAL DW-200 SWITCH) OSD - INDICATES WALL SWITCH OCC SENSOR WITH 0-10V DIMMING - WATTSTOPPER DW-311 a - INDICATES SINGLE POLE LIGHTING SWITCH ZONE FOR ZONE a b - INDICATES SINGLE POLE LIGHTING SWITCH ZONE FOR ZONE b ab - INDICATES LIGHTING SWITCHES WITH MULTIPLE ZONES	OCC LV LV OCCUPANCY SENSOR - DUAL TECHNOLOGY CEILING MOUNT: WATTSTOPPER LMDC-100, OR EQUAL WALL MOUNT: WATTSTOPPER LMDX-100, OR EQUAL WALL MOUNT AT +96", UNO
OCC LV LV OCCUPANCY SENSOR - DUAL TECHNOLOGY CEILING MOUNT: WATTSTOPPER DT-300, OR EQUAL WALL MOUNT: WATTSTOPPER DT-200, OR EQUAL WALL MOUNTED SHALL BE AT +96", UNO PROVIDE WITH BZ-50 POWER PACKS AS NEEDED.	P LV PHOTOCELL - CEILING MOUNT WATTSTOPPER LMLS-400, OR EQUAL
P PHOTOCELL - CEILING MOUNT, WATTSTOPPER LS-301, OR EQUAL	(1) ON/OFF ROOM CONTROLLER WITH (1) RELAY WATTSTOPPER DLM LMRC-101, OR EQUAL
	(2) ON/OFF ROOM CONTROLLER WITH (2) RELAYS WATTSTOPPER DLM LMRC-102, OR EQUAL
	(2V) ON/OFF/0-10V ROOM CONTROLLER WITH (2) RELAYS WATTSTOPPER DLM LMRC-212, OR EQUAL
	(3V) ON/OFF/0-10V ROOM CONTROLLER WITH (3) RELAYS WATTSTOPPER DLM LMRC-213, OR EQUAL
	$_{LVD} LOW VOLTAGE DIMMING SWITCH WATTSTOPPER DLM LMDM-101, OR EQUAL
	$_{LV} LOW VOLTAGE SWITCH, # INDICATES NUMBER OF BUTTONS. NO "#" IS A 2 BUTTON SWITCH. WATTSTOPPER DLM LMSW-10#, OR EQUAL

ELECTRICAL SHEET INDEX

NUMBER	SHEET NAME
E000	ELECTRICAL SYMBOLS AND ABBREVIATIONS
E001	ELECTRICAL DETAILS
E102	LEVEL 1 ELECTRICAL DEMOLITION PLAN
E106	LEVEL 1 POWER PLAN
E108	LEVEL 1 LIGHTING PLAN

mosaic
architecture-planning-design
317 Cruse Avenue Suite 201
Helena, Montana 59601
406.449.2013
www.mosaicarch.com

PROFESSIONAL ENGINEER REGISTERED STATE OF IDAHO TIMOTHY L. STEVENS

U.S. DEPARTMENT OF AGRICULTURE
FOREST SERVICE
R-1 NORTHERN REGION

Morrison Maierle
engineers · surveyors · planners · scientists
1 Engineer Place
Helena, MT 59602
406.442.3050
www.m-m.net

COPYRIGHT © MORRISON-MAIERLE, 2022

POWELL DUPLEX RENOVATION

LOCHSA-POWELL RANGER DISTRICT,
192 POWELL RD,
LOLO, ID 59847

CONSTRUCTION DOCUMENTS


MARK	DATE	REVISION

PROJECT NO. 1240LU23F0138
DATE: 7/19/2024
Drawn By: TL
Designed By: TL
Checked By: GS

ELECTRICAL SYMBOLS AND ABBREVIATIONS

SHEET: **E000**

DATE STAMP 7/17/2024 13:26:04

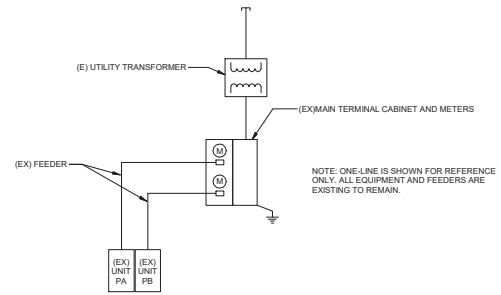

1 EXISTING ONE-LINE DIAGRAM
N.T.S.

MEP COORDINATION SCHEDULE

CONTROL TYPE:

BAS	BUILDING AUTOMATION SYSTEM
CO	CARBON MONOXIDE DETECTOR
CONT	CONTINUOUS OPERATION
EF	INTERLOCK WITH EXHAUST FAN
HCP	HOOD CONTROL PANEL
INT	INTEGRAL
L	LIGHT SWITCH
MS	MANUAL SWITCH
OS	OCCUPANCY SENSOR
PS	PRESSURE SWITCH
T	THERMOSTAT
TC	TIME CLOCK
UC	UNIT CONTROLLER
VE	VEHICLE EXHAUST DETECTION
N/A	SYSTEM...

DISCONNECT/STARTER TYPE:

CB	PANELBOARD CIRCUIT BREAKER WITHIN SIGHT OF EQUIPMENT
CSFD	COMBINATION STARTER/DISCONNECT - HOA
FD	FUSED DISCONNECT
FST	FUSTAT
FW	FACTORY-WIRED SINGLE POINT CONNECTION
MOCP	MOTOR OVER-CURRENT PROTECTION
MSS	MANUAL STARTER SWITCH WITH THERMAL OVERLOADS (1-, 2- OR 3-POLE AS REQUIRED)
NFD	NON-FUSED DISCONNECT
RCPT	20A DUPLEX RECEPTACLE (GFCI PROTECTED AS REQUIRED), CORD AND PLUG
RVSS	REDUCED VOLTAGE SOLID-STATE
VFD	VARIABLE FREQUENCY DRIVE - HOA
N/A	NOT APPLICABLE

DIVISION OF RESPONSIBILITIES:

22/22	FURNISHED AND INSTALLED BY DIV. 22, WIRED BY DIV. 22
22/26	FURNISHED AND INSTALLED BY DIV. 22, WIRED BY DIV. 26
23/23	FURNISHED AND INSTALLED BY DIV. 23, WIRED BY DIV. 23
23/26	FURNISHED AND INSTALLED BY DIV. 23, WIRED BY DIV. 26
26/26	FURNISHED AND INSTALLED BY DIV. 26, WIRED BY DIV. 26

NOTES:
1. INTEGRAL DISCONNECTS AND OVERLOADS
2. INTEGRAL OVERLOADS
3. SINGLE POINT CONNECTION
4. PROVIDE RECEPTACLE AND DATA CONNECTION FOR PANEL
5. MOUNT ON UNI-STRUT IN FRONT OF UNIT
6. SIZE FUSES IN ACCORDANCE WITH MANUFACTURER'S GUIDELINES FOR INSTALLED EQUIPMENT
7. INTEGRAL VARIABLE FREQUENCY DRIVE
8. DUCT SMOKE DETECTOR(S) REQUIRED

GENERAL NOTES:
A. CONTROL WIRING SHALL BE CONCEALED WITHIN WALL CONSTRUCTION, ABOVE CEILING, OR RUN IN CONDUIT. EXPOSED CONTROL WIRING IS UNACCEPTABLE.
B. UNLESS SPECIFICALLY NOTED, ALL FEEDERS SHALL INCLUDE A FULL SIZE NEUTRAL. IT IS THE CONTRACTOR'S RESPONSIBILITY TO VERIFY WITH THE MANUFACTURER OF THE ACTUAL EQUIPMENT BEING SUPPLIED WHETHER A NEUTRAL IS
C. REQUIRED PRIOR TO ROUGH-IN.
ALL DUCT SMOKE DETECTORS FURNISHED BY DIV. 26, INSTALLED BY DIV. 23, AND WIRED BY DIV. 26. DIV. 26 SHALL WIRE ALL FANS TO SHUT DOWN WHEN ALARM IS INITIATED BY ANY DUCT SMOKE DETECTOR.

MARK	DESCRIPTION	ELECTRICAL DATA		CONTROL		NOTES	DISCONNECT / STARTER		DISCONNECT				FEEDER	
		LOAD	VOLT-PHASE	TYPE	DIV		TYPE	DIV	SIZE (NEMA)	SWITCH (AMPS)	FUSE (AMPS)	ENCLOSURE (NEMA)	COPPER WIRE (AWG)	CONDUIT (INCHES)
BB-1	ELECTRIC BASEBOARD	2000 W	240 - 1	T	23 / 26	3	FW	23/26	--	--	--	--	12	3/4
BB-2	ELECTRIC BASEBOARD	2000 W	240 - 1	T	23 / 26	3	FW	23/26	--	--	--	--	12	3/4

LUMINAIRE SCHEDULE

TYPE	LAMPS	LOAD (W)	OUTPUT (LM, NOMINAL)	CCT (K)	DESCRIPTION	MFR	CATALOG NO. OR SERIES	MOUNTING	VOLTAGE	NOTES
CF1	LED	21 W	1,600	3000	WILDER 60" FAN WITH LED LIGHT. PROVIDE WITH ANGLE MOUNTING FOR SLOPED CEILING	HUNTER	51566 - WILDER 60" CEILING FAN	CEILING	120 V	2,6
D1	LED	15 W	1,000	3000	7" ROUND DOWNLIGHT	JUNO	JSF-7IN-10LM-SWWR-90CRI-MVOLT ZT-WH	CEILING	120 V	2
S1	LED	23 W	2,175	3000	EDGELIT 18" SURFACE MOUNT DOWNLIGHT	PROGRESS LIGHTING	P810018-030-30	CEILING	120 V	2
W1	LED	20 W	2,100	3000	OUTDOOR ARCHITECTURAL HALF ROUND WALL SCONCE.	LITHONIA	WSQ-LED-P1-30K-SR3-120-PE-DBLXD	WALL	120 V	2,6

NOTES:
1. PRIOR SUBMITTAL NOT REQUIRED. ALL ALTERNATE FIXTURE SHOP DRAWINGS WILL BE REVIEWED AFTER THE PROJECT IS AWARDED.
2. PRIOR SUBMITTAL IS REQUIRED.
3. ALTERNATE FIXTURE IS NOT ACCEPTED FOR SUBSTITUTIONS.
4. PROVIDE 0-10V DIMMING, DOWN TO 10% LUMEN OUTPUT, MINIMUM.
5. PROVIDE FUSING.
6. VERIFY FINISH WITH C.O.
7. PROVIDE WITH REMOTE 12V STEP-DOWN TRANSFORMER.
8. CIRCUIT VIA TYPE EM INVERTER.
9. LAMP DATA IS FOR 4' CROSS-SECTION OF FIXTURE.
10.MOUNT BOTTOM OF FIXTURE CENTERED AT 6" ABOVE TOP OF MIRROR. SEE ARCHITECT ELEVATIONS.

GENERAL NOTE:
THE ELECTRICAL CONTRACTOR SHALL VERIFY ALL CEILING TYPES AND PROVIDE ALL MOUNTING, FIRE-RATED, AND IC-RATED ACCESSORIES AS REQUIRED. FOR FIRE-RATED CEILING ASSEMBLIES AND FOR CEILINGS WITH INSULATION, VERIFY ALL RECESSED LUMINAIRE HOUSINGS ARE RATED APPROPRIATELY OR PROVIDE DROP-OVER ENCLOSURES OR TENTS FOR LUMINAIRES. VERIFY THAT DROP-OVER ENCLOSURES OR TENTS ALLOW FOR AIR SPACE AROUND LUMINAIRE PER MANUFACTURER'S RECOMMENDATIONS.

Branch Panel: (EX)PA

Location: KITCHEN 106 | **Volts:** 120/240 Single | **A.I.C. Rating:**
Supply From: | **Phases:** 1 | **Mains Type:** MLO
Mounting: Recessed | **Wires:** 3 | **Mains Rating:** 100 A
Enclosure:

Notes:
PANEL IS A SQUARE D QD LOAD CENTER

CKT	Circuit Description	Load Classification	Trip	Poles	A		B		Poles	Trip	Load Classification	Circuit Description	CKT
1	RCPT - LIVING ROOM	Receptacle	20 A	1	540	0			1	20 A	--	SPARE	2
3	(EX) RANGE	--	20 A	2			0	0	2	30 A	--	(EX) WATER HEATER	4
5					0	0							6
7	(EX) DRYER	--	20 A	2			0	0	2	20 A	--	(EX) LIVING ROOM HEAT	8
9					0	0							10
11	(EX) WASHER	--	20 A	1			0	0	1	20 A	--	(EX) N. BED HEAT	12
13	(EX) UP BED HEAR	--	20 A	1	0	0			1	20 A	--	(EX) N. BED HEAT	14
15	SPARE	--	20 A	1			0	0	1	20 A	--	(EX) SMOKE DETECTORS	16
17	(EX) N. BED ROOM HEAR	--	20 A	1	0	0			1	20 A	--	(EX) N. BED ROOM LIGHTS, RECEPTS, HALL	18
19	PWR - BB-1	Heating	20 A	2			1000	0	1	20 A	--	(EX) DISHWASHER	20
21					1000	0			1	20 A	--	SPARE	22
23	SPARE	--	20 A	1			0	0	1	20 A	--	SPARE	24
25	SPARE	--	20 A	1	0	0			1	20 A	--	(EX) STORAGE ROOM HEAT	26
27	(EX) KITCHEN HEAR	--	20 A	2			0	0	1	20 A	--	(EX) LIGHTS	28
29					0	0			1	20 A	--	SPARE	30
31	(EX) W. BED ROOM LIGHTS AND RECEPT.	--	20 A	1			0	0	1	20 A	--	(EX) BATHROOM LIGHTS & GARAGE RECEPT.	32
33	SPARE	--	20 A	1	0	0			1	20 A	--	(EX) KITCHEN RECEPTACLES	34
35	(EX) UP BED ROOM LIGHTS AND RECEPT.	--	20 A	1			0	0	1	20 A	--	(EX) KITCHEN RECEPTACLES	36
37	(EX) STORAGE LIGHTS AND RECEPT.	--	20 A	1	0	0			1	20 A	--	(EX) KITCHEN RECEPTACLES	38
39	(EX) LIVING ROOM RECEPT.	--	20 A	1			0	0	1	20 A	--	(EX) KITCHEN RECEPTACLES	40
41	SPARE	--	20 A	1	0	0			1	20 A	--	SPARE	42
					Total Load:	1540 VA		1000 VA					
					Total Amps:	13 A		8 A					

Legend:

Load Classification	Connected Load	Demand Factor	Estimated Demand	Panel Totals	
Heating	2000 VA	100.00%	2000 VA		
Receptacle	540 VA	100.00%	540 VA	**Total Conn. Load:**	2540 VA
				Total Est. Demand:	2540 VA
				Total Conn.:	11 A
				Total Est. Demand:	11 A

Notes:

Branch Panel: (EX)PB

Location: CORRIDOR 112 | **Volts:** 120/240 Single | **A.I.C. Rating:**
Supply From: | **Phases:** 1 | **Mains Type:** MLO
Mounting: Recessed | **Wires:** 3 | **Mains Rating:** 100 A
Enclosure:

Notes:
PANEL IS A SQUARE D QD LOAD CENTER

CKT	Circuit Description	Load Classification	Trip	Poles	A		B		Poles	Trip	Load Classification	Circuit Description	CKT
1	SPARE	--	20 A	1	0	540			1	20 A	Receptacle	REC - LIVING ROOM	2
3	(EX) RANGE	--	20 A	2			0	0	2	20 A	--	(EX) WATER HEATER	4
5					0	0							6
7	(EX) DRYER	--	20 A	2			0	0	2	20 A	--	(EX) LIVING ROOM HEAT	8
9					0	0							10
11	SPARE	--	20 A	1			0	0	2	20 A	--	(EX) LIVING ROOM HEAT	12
13	(EX) KITCHEN HEAT	--	20 A	1	0	0							14
15	(EX) KITCHEN HEAR	--	20 A	1			0	1000	2	20 A	Heating	PWR - BB-2	16
17	SPARE	--	20 A	1	0	1000							18
19	SPARE	--	20 A	1			0	0	1	20 A	--	SPARE	20
21	SPARE	--	20 A	1	0	0			1	20 A	--	SPARE	22
23	(EX) N. BED ROOM HEAR	--	20 A	1			0	0	1	20 A	--	SPARE	24
25	(EX) E. BED ROOM HEAT	--	20 A	1	0	0			1	20 A	--	SPARE	26
27	(EX) KITCHEN LIGHTS	--	20 A	1			0	0	1	20 A	--	SPARE	28
29	(EX) BATH HEAT	--	20 A	2	0	0			1	20 A	--	(EX) W. BED HEAT	30
31							0	0	1	20 A	--	(EX) BATH LIGHTS	32
33	(EX) SMOKE DETECTORS	--	20 A	1	0	0			1	20 A	--	(EX) KITCHEN PLUGS	34
35	(EX) LIVING ROOM PLUGS	--	20 A	1			0	0	1	20 A	--	(EX) KITCHEN PLUGS	36
37	(EX) UP BATH LIGHTS AND RECEPTS	--	20 A	1	0	0			1	20 A	--	(EX) DISHWASHER / DISPOSAL	38
39	(EX) W. BED ROOM LIGHTS AND RECEPTS	--	20 A	1			0	0	1	20 A	--	(EX) KITCHEN PLUGS	40
41	(EX) E. BED ROOM LIGHTS AND RECEPTS	--	20 A	1	0	0			1	20 A	--	(EX) LIVING ROOM PLUGS	42
					Total Load:	1540 VA		1000 VA					
					Total Amps:	13 A		8 A					

Legend:

Load Classification	Connected Load	Demand Factor	Estimated Demand	Panel Totals	
Heating	2000 VA	100.00%	2000 VA		
Receptacle	540 VA	100.00%	540 VA	**Total Conn. Load:**	2540 VA
				Total Est. Demand:	2540 VA
				Total Conn.:	11 A
				Total Est. Demand:	11 A

Notes:

DATE STAMP 7/17/2024 13:26:04

mosaic architecture-planning-design
317 Cruse Avenue Suite 201
Helena, Montana 59601
406.449.2013
www.mosaicarch.com

PROFESSIONAL ENGINEER REGISTERED STATE OF IDAHO GARTH L. STEVENS

U.S. DEPARTMENT OF AGRICULTURE
FOREST SERVICE
R-1 NORTHERN REGION

Morrison Maierle
engineers · surveyors · planners · scientists
1 Engineer Place
Helena, MT 59602
406.442.3050
www.m-m.net

COPYRIGHT © MORRISON-MAIERLE, 2022

POWELL DUPLEX RENOVATION

LOCHSA-POWELL RANGER DISTRICT,
192 POWELL RD,
LOLO, ID 59847


CONSTRUCTION DOCUMENTS

MARK	DATE	REVISION

PROJECT NO. 1240LU23F0138
DATE: 7/19/2024
Drawn By: TL
Designed By: TL
Checked By: GS

ELECTRICAL DETAILS

SHEET: **E001**

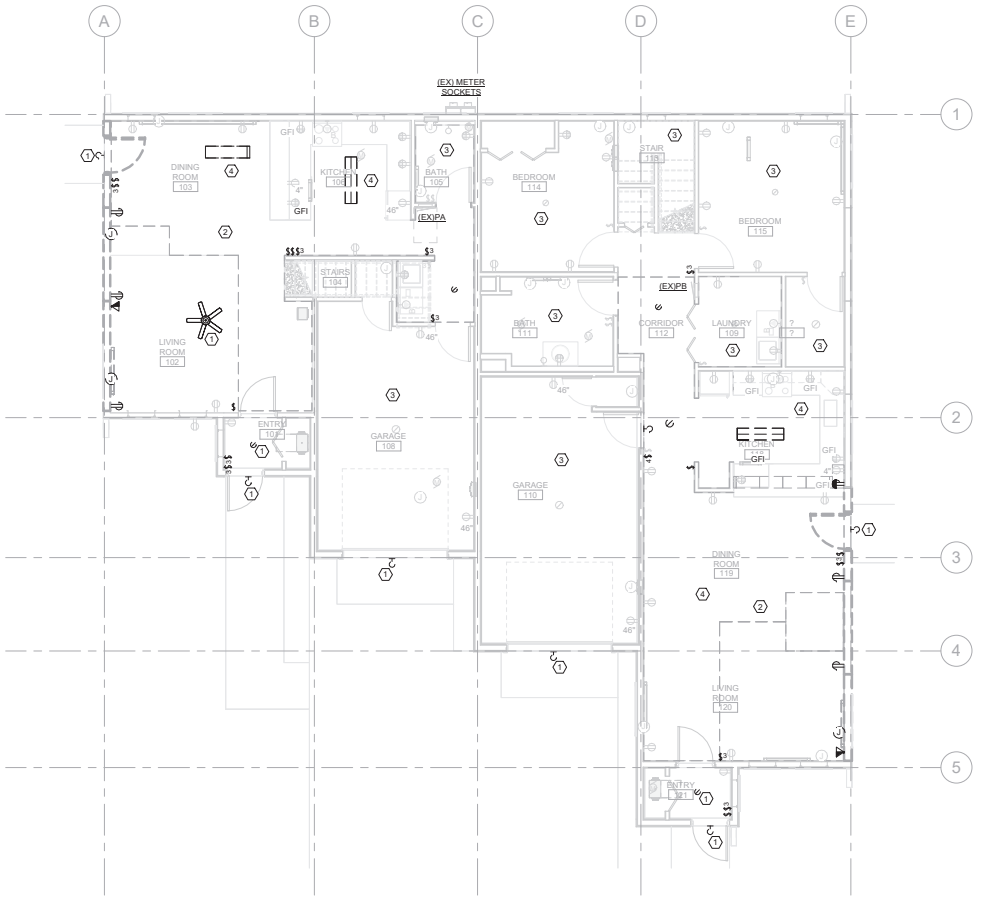

1 LEVEL 1 - ELECTRICAL DEMOLITION PLAN
3/16" = 1'-0"

ELECTRICAL DEMO NOTES

A. IT IS ABSOLUTELY NECESSARY FOR ALL TRADES INVOLVED TO COORDINATE WITH EACH OTHER AND VERIFY THAT THERE ARE NO CONFLICTS IN LOCATION OF DUCTS, CONDUITS, DIFFUSERS, BOXES, AND OTHER ITEMS THROUGHOUT THIS PROJECT BEFORE FINAL PLACEMENT OF MATERIALS.
B. ELECTRICAL CONTRACTOR IS RESPONSIBLE FOR ALL CUTTING OF FLOORS, WALLS, CEILINGS, AND ROOFS TO PERFORM THE REQUIRED WORK DEPICTED IN THESE DOCUMENTS. THE CONTRACTOR IS RESPONSIBLE FOR ALL PATCHING OF HOLES TO THE SATISFACTION OF THE ARCHITECT/ENGINEER.
C. ALL WALL REGIONS SHOWN DASHED ARE EXISTING, TO BE DEMO'D, OR IN SOME CASES ARE EXISTING DOORWAYS TO BE WALLED IN. CONTRACTOR SHALL FIELD-VERIFY AFFECTED POWER, LIGHTING AND SIGNAL, PRIOR TO BID.
D. DASHED WALLS, EQUIPMENT, FIXTURES AND DEVICES SHOWN BLACK, OR BLACK AND DASHED ARE EXISTING FOR DEMO, AND ITEMS IN GRAY AND SOLID ARE EXISTING TO REMAIN, UNLESS SPECIFICALLY NOTED OTHERWISE.
E. ALL ITEMS NOTED FOR DEMO SHALL BE COMPLETELY DEMO'D, INCLUDING DISCONNECTS, CONDUIT AND CONDUCTORS BACK TO SOURCE, UNLESS SPECIFICALLY NOTED OTHERWISE.
F. NOT ALL EXISTING DEVICE LOCATIONS HAVE BEEN VERIFIED OR SHOWN ON THESE PLANS. THE CONTRACTOR SHALL FIELD-VERIFY EXSITING CONDITIONS, PRIOR TO BID.

KEY NOTES:

1. FIXTURE TO BE REMOVED AND REPLACED. MAINTAIN WIRING FOR REUSE WHERE POSSIBLE.
2. CONTRACTOR SHALL MAKE PROVISIONS FOR CIRCUITING MODIFICATIONS AS A RESULT OF REMODEL WORK. SOME CIRCUITS MAY EXTEND BEYOND DEMOLITION SCOPE OF WORK. CONTRACTOR SHALL PRESERVE, MODIFY AND EXTEND OR REPLACE WIRING AS REQUIRED. TYPICAL.
3. EXISTING RECEPTACLES, LUMINAIRES, CONTROLS AND CIRCUITING REMAIN UNCHANGED IN THIS AREA.
4. EXCEPT WHERE SHOWN AS BEING DEMO'ED, EXISTING RECEPTACLES AND CIRCUITING REMAIN UNCHANGED IN THIS AREA. WHERE DEVICES ARE SHOWN AS BEING DEMO'ED, RETAIN THE EXISTING CIRCUITING IN THE AREA FOR REUSE.

mosaic
architecture-planning-design
317 Cruse Avenue Suite 201
Helena, Montana 59601
406.449.2013
www.mosaicarch.com

PROFESSIONAL ENGINEER REGISTERED STATE OF IDAHO TARTH L. STEVENS

U.S. DEPARTMENT OF AGRICULTURE
FOREST SERVICE
R-1 NORTHERN REGION

Morrison Maierle
engineers · surveyors · planners · scientists
1 Engineer Place
Helena, MT 59602
406.442.3050
www.m-m.net

COPYRIGHT © MORRISON-MAIERLE, 2022

POWELL DUPLEX RENOVATION

LOCHSA-POWELL RANGER DISTRICT,
192 POWELL RD,
LOLO, ID 59847

CONSTRUCTION DOCUMENTS


MARK	DATE	REVISION

PROJECT NO. 1240LU23F0138
DATE: 7/19/2024
Drawn By: TL
Designed By: TL
Checked By: GS

LEVEL 1 ELECTRICAL DEMOLITION PLAN

SHEET: **E102**

DATE STAMP 7/17/2024 13:26:05

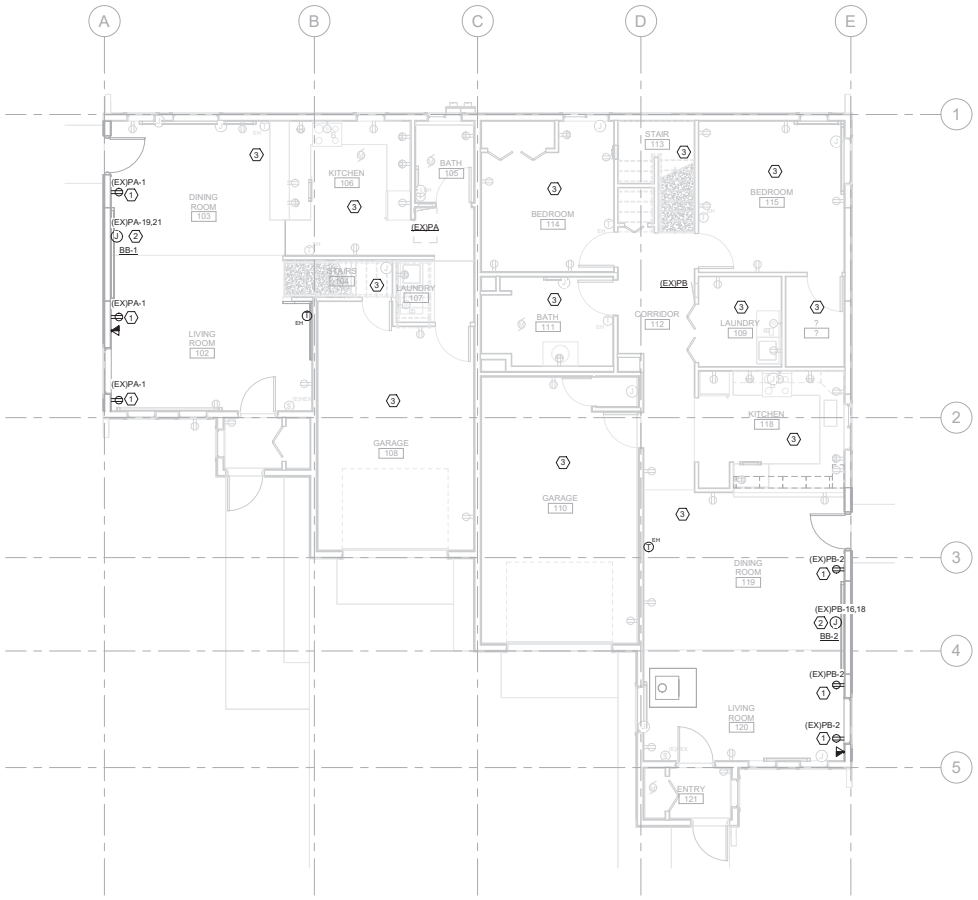

1 LEVEL 1 - POWER PLAN
3/16" = 1'-0"

POWER PLAN GENERAL NOTES

A. IT IS ABSOLUTELY NECESSARY FOR ALL TRADES INVOLVED TO COORDINATE WITH EACH OTHER AND VERIFY THAT THERE ARE NO CONFLICTS IN LOCATION OF DUCTS, CONDUITS, DIFFUSERS, BOXES, AND OTHER ITEMS THROUGHOUT THIS PROJECT BEFORE FINAL PLACEMENT OF MATERIALS.
B. ELECTRICAL CONTRACTOR IS RESPONSIBLE FOR ALL CUTTING OF FLOORS, WALLS, CEILINGS, AND ROOFS TO PERFORM THE REQUIRED WORK DEPICTED IN THESE DOCUMENTS. THE CONTRACTOR IS RESPONSIBLE FOR ALL PATCHING OF HOLES TO THE SATISFACTION OF THE ARCHITECT/ENGINEER.
C. LOW VOLTAGE CABLES (LIGHTING CONTROLS) ABOVE ACCESSIBLE CEILINGS SHALL BE SUPPORTED USING J-HOOKS AT INTERVALS NOT TO EXCEED 48" OC, UNO.

(#) KEY NOTES:

1. REUSE EXISTING CIRCUIT THAT WAS SERVING DEMO'ED DEVICES IN THIS AREA. MODIFY AND EXTEND CONDUIT AND WIRING AS REQUIRED TO ACCOMMODATE PROVIDING NEW DEVICES IN REMODEL WORK.
2. REUSE EXISTING CIRCUIT THAT WAS SERVING DEMO'ED BASEBOARD HEATER IN THIS AREA. MODIFY AND EXTEND CONDUIT AND WIRING AS REQUIRED TO ACCOMMODATE PROVIDING NEW BASEBOARD HEATER IN REMODEL WORK.
3. EXISTING RECEPTACLES AND CIRCUITING REMAIN UNCHANGED IN THIS AREA.

mosaic
architecture-planning-design
317 Cruse Avenue Suite 201
Helena, Montana 59601
406.449.2013
www.mosaicarch.com

PROFESSIONAL ENGINEER REGISTERED STATE OF IDAHO GARTH L. STEVENS

U.S. DEPARTMENT OF AGRICULTURE
FOREST SERVICE
R-1 NORTHERN REGION

Morrison Maierle
engineers · surveyors · planners · scientists
1 Engineer Place
Helena, MT 59602
406.442.3050
www.m-m.net

COPYRIGHT © MORRISON-MAIERLE, 2022

POWELL DUPLEX RENOVATION

LOCHSA-POWELL RANGER DISTRICT,
192 POWELL RD,
LOLO, ID 59847

CONSTRUCTION DOCUMENTS


MARK	DATE	REVISION

PROJECT NO. 1240LU23F0138
DATE: 7/19/2024
Drawn By: TL
Designed By: TL
Checked By: GS

LEVEL 1 POWER PLAN

SHEET: E106

DATE STAMP 7/17/2024 13:26:05

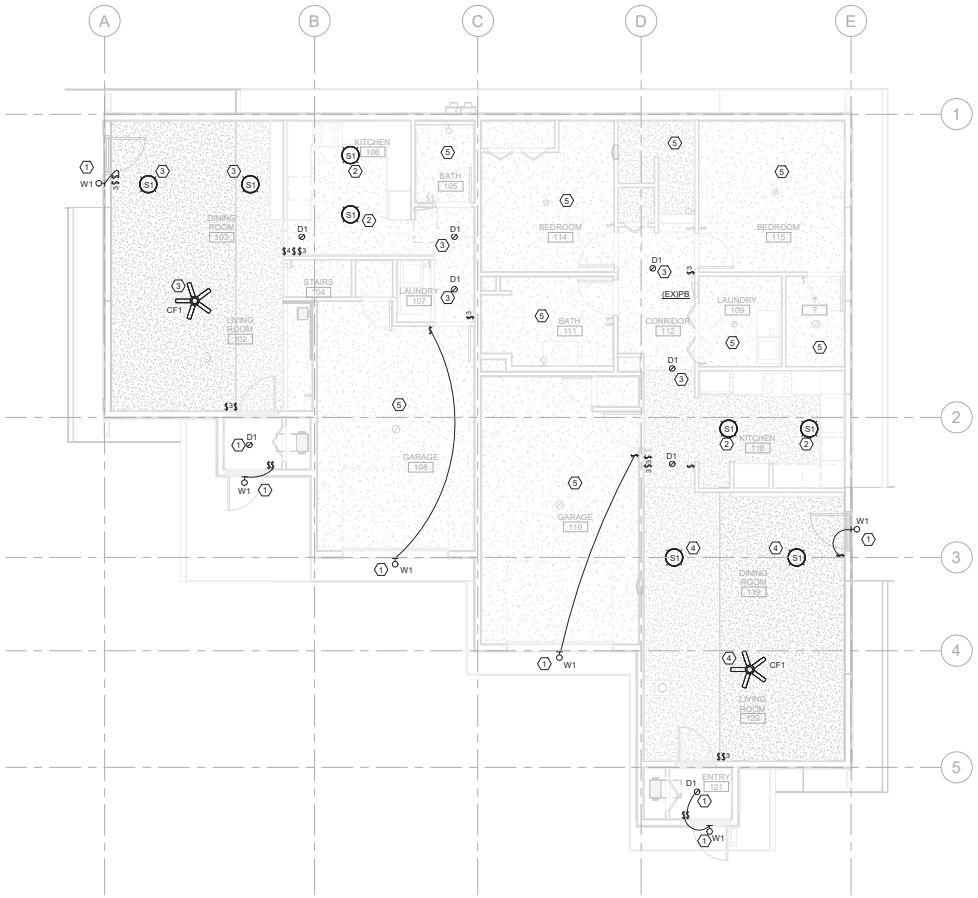

1 LEVEL 1 -LIGHTING PLAN
3/16" = 1'-0"

LIGHTING PLAN GENERAL NOTES

A. IT IS ABSOLUTELY NECESSARY FOR ALL TRADES INVOLVED TO COORDINATE WITH EACH OTHER AND VERIFY THAT THERE ARE NO CONFLICTS IN LOCATION OF DUCTS, CONDUITS, DIFFUSERS, BOXES, AND OTHER ITEMS THROUGHOUT THIS PROJECT BEFORE FINAL PLACEMENT OF MATERIALS.
B. ELECTRICAL CONTRACTOR IS RESPONSIBLE FOR ALL CUTTING OF FLOORS, WALLS, CEILINGS, AND ROOFS TO PERFORM THE REQUIRED WORK DEPICTED IN THESE DOCUMENTS. THE CONTRACTOR IS RESPONSIBLE FOR ALL PATCHING OF HOLES TO THE SATISFACTION OF THE ARCHITECT/ENGINEER.
C. LOW VOLTAGE CABLES (LIGHTING CONTROLS) ABOVE ACCESSIBLE CEILINGS SHALL BE SUPPORTED USING J-HOOKS AT INTERVALS NOT TO EXCEED 48" OC, UNO.

(#) KEY NOTES:

1. CONNECT FIXTURE TO EXISTING CIRCUIT. MODIFY AND EXTEND CONDUIT AND WIRING AS REQUIRED.
2. REUSE EXISTING LIGHTING CIRCUIT CURRENTLY SERVING THE KITCHEN. MODIFY AND EXTEND CONDUIT AND WIRING AS REQUIRED.
3. REUSE EXISTING LIGHTING CIRCUIT IN THIS AREA TO SERVE NEW FIXTURE(S), VIA NEW CONTROLS. MODIFY AND EXTEND CONDUIT AND WIRING AS REQUIRED.
4. EXTEND LIGHTING CIRCUIT FROM THE KITCHEN TO THE LIVING AREA, VIA NEW CONTROLS, TO SERVE NEW FIXTURES. MODIFY CONDUIT AND WIRING AS REQUIRED.
5. EXISTING INTERIOR LUMINAIRES, CONTROLS AND CIRCUITING REMAIN UNCHANGED IN THIS AREA.

mosaic
architecture-planning-design
317 Cruse Avenue Suite 201
Helena, Montana 59601
406.449.2013
www.mosaicarch.com

PROFESSIONAL ENGINEER REGISTERED STATE OF IDAHO GARTH L. STEVENS

FOREST SERVICE U.S. DEPARTMENT OF AGRICULTURE

U.S. DEPARTMENT OF AGRICULTURE
FOREST SERVICE
R-1 NORTHERN REGION

Morrison Maierle
engineers · surveyors · planners · scientists
1 Engineer Place
Helena, MT 59602
406.442.3050
www.m-m.net

COPYRIGHT © MORRISON-MAIERLE, 2022

POWELL DUPLEX RENOVATION

LOCHSA-POWELL RANGER DISTRICT,
192 POWELL RD,
LOLO, ID 59847

CONSTRUCTION DOCUMENTS

MARK	DATE	REVISION

PROJECT NO. 1240LU23F0138
DATE: 7/19/2024
Drawn By: TL
Designed By: TL
Checked By: GS

LEVEL 1 LIGHTING PLAN

SHEET: E108

DATE STAMP 7/17/2024 13:26:05