
United States Department of Agriculture
Forest Service

FRESNO COUNTY
R05 PACIFIC SOUTHWEST REGION
SIERRA NATIONAL FOREST
HIGH SIERRA RANGER DISTRICT


ADMINISTRATION AND RECREATION FACILTIES REHABILITATION


HIGH SIERRA NEW BARRACKS

CONTENTS		
NO	SHEET NO	SHEET TITLE
1	G1	COVERSHEET
2	G2	HIGH SIERRA VICINITY MAP
3	C1	DEMOLITION PLAN 1
4	C2	DEMOLITION PLAN 2
5	C5	HIGH SIERRA UTILITIES
6	C6	SITE PLAN 1
7	C7	SITE PLAN 2
8	G3	AUBERRY VICINITY MAP
9	C8	SITE PLAN 3
10	G4	WISHON VICINITY MAP
11	C9	SITE PLAN 4
12	Z1	POTENTIAL BARRACKS LAYOUT AND ELEVATION
13	Z2	PROPOSED TOILET
14	Z3	PROPOSED POLE BARN

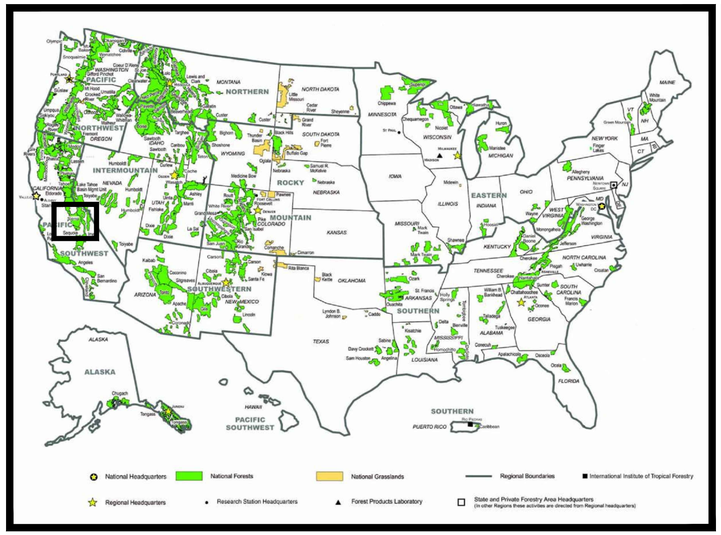


FOREST LOCATION MAP

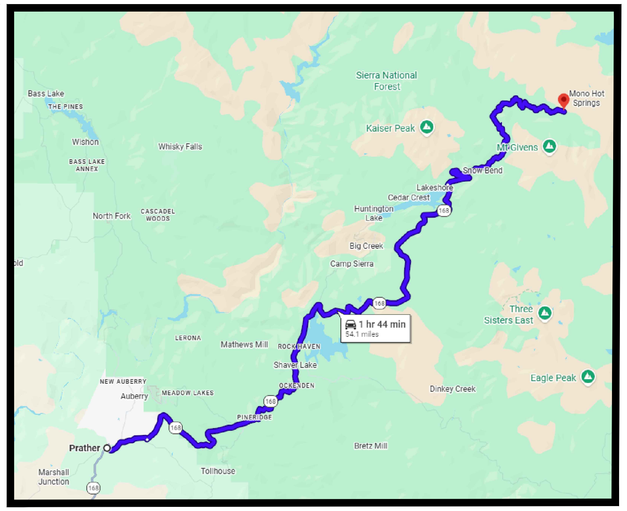

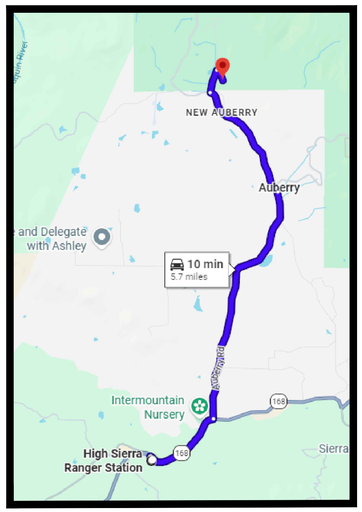

PROJECT LOCATION MAPS

Map data ©2026 Google

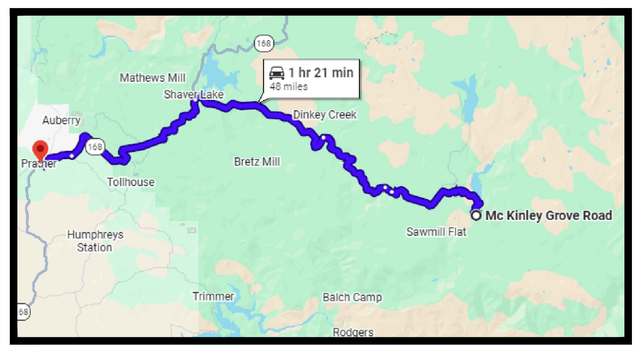

TRAVEL DIRECTIONS:

HIGH SIERRA STATION (LEFT):
FROM THE HIGH SIERRA RANGER DISTRICT OFFICE, 29688 Auberry Rd, Prather, CA 93651, PROCEED EAST ON HIGHWAY 168 FOR 33 MILES TURN RIGHT ONTO KAISER PASS RD. CONTINUE FOR 21 MILES. DESTINATION IS ON THE LEFT

AUBERRY STATION (MIDDLE):
FROM THE HIGH SIERRA RANGER DISTRICT OFFICE, 29688 Auberry Rd, Prather, CA 93651, PROCEED EAST ON HIGHWAY 168 FOR 3 MILES. TURN LEFT ONTO AUBERRY RD. TAKE A SLIGHT LEFT ONTO POWERHOOUSE RD. TURN RIGHT ONTO WISH I AH RD. CONTINUE FOR 0.3 MILES. DESTINATION IS ON THE RIGHT.

WISHON STATION (RIGHT):
FROM THE HIGH SIERRA RANGER DISTRICT OFFICE, 29688 Auberry Rd, Prather, CA 93651, PROCEED EAST ON HIGHWAY 168 for 17 MILES. TURN RIGHT ON DINKEY CREEK RD, CONTINUE FOR 20 MILES. TURN RIGHT ONTO MCKINLY GROVE RD. CONTINUE FOR ANOTHER 20 MILES. DESTINATION IS ON YOUR RIGHT.

RECOMMENDED BY:

FOREST ENGINEER _____ DATE _____

DISTRICT RANGER _____ DATE _____


FOREST SUPERVISOR _____ DATE _____

RO FACILITIES PROGRAM MANAGER _____ DATE _____

APPROVED:

DIRECTOR OF ENGINEERING _____ DATE _____

2/2/26 15:23 ANTHONY PETROSSO D:\REHAB NEW TINY HOMES\REHAB PLACEMENT.DWG;

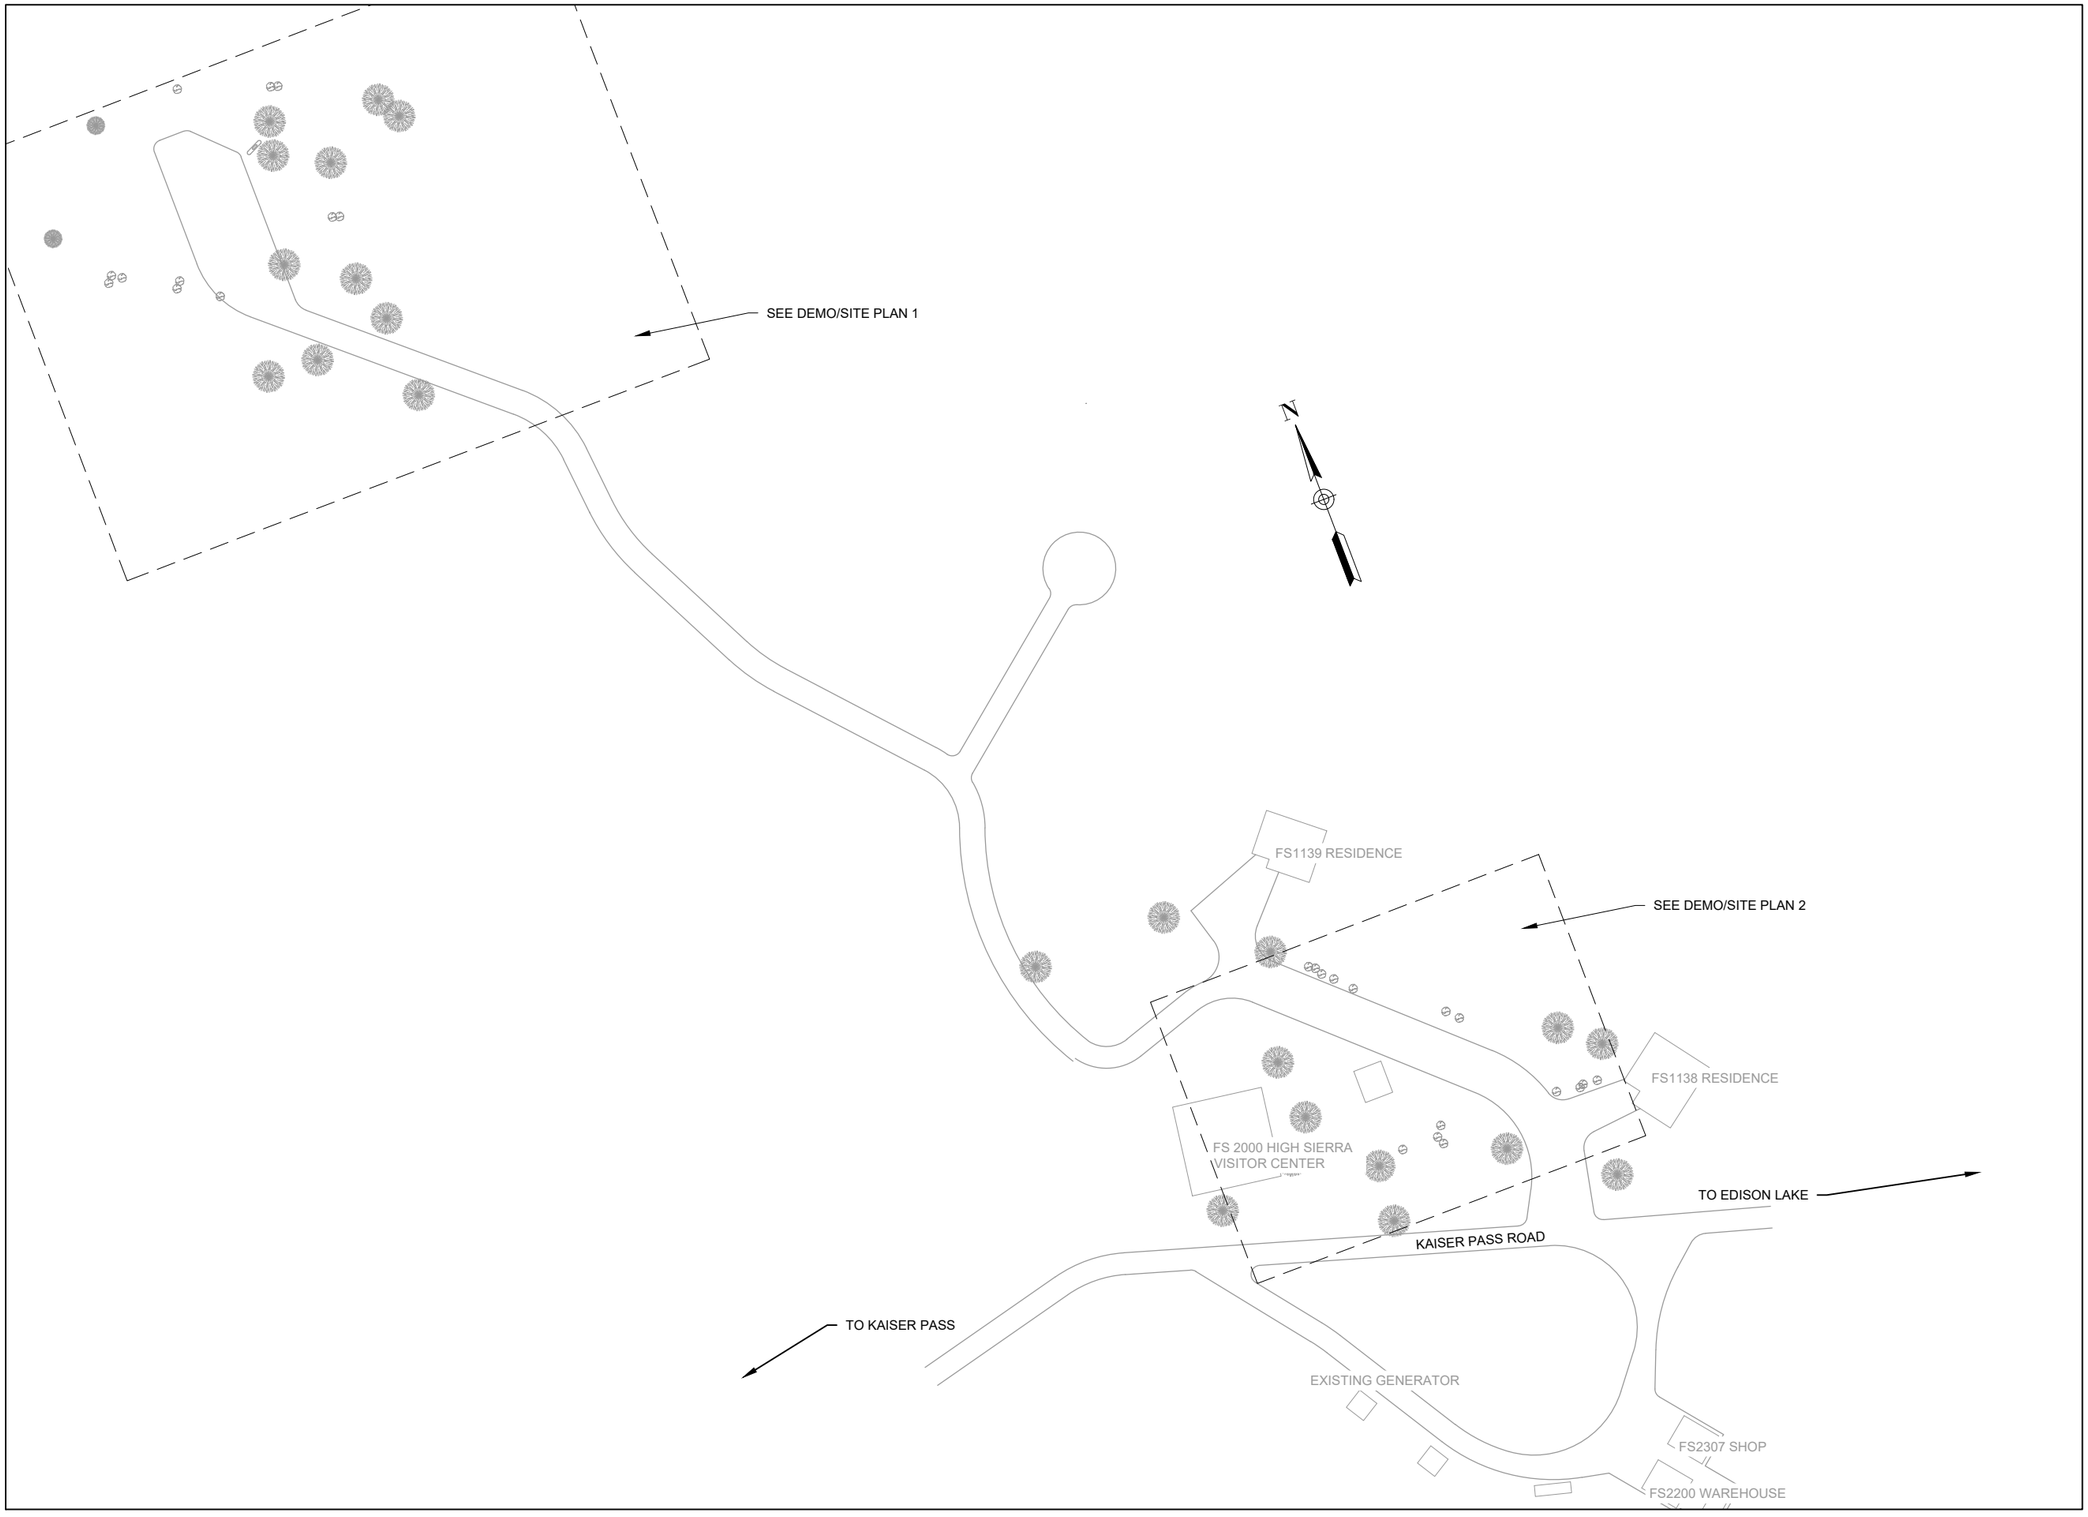

2/23/26 15:23 ANTHONY.PETROSSO D:\REHAB NEW TINY HOMES\REHAB PLACEMENT.DWG

United States Department of Agriculture
Forest Service

(R05)
Pacific Southwest Region

STAMPS, LOGOS, AND SEALS

NO.	REVISION / ISSUE	DATE
4		
3		
2		
1		

PROJECT NAME

HS NEW BARRACKS ADMIN AND REC REHAB


Sierra National Forest

High Sierra Ranger District

DRAWING TITLE

HIGH SIERRA VICINITY MAP

DATE 2/23/2026	ARCHIVE NO.
DESIGNER A.PETROSSO	DRAWING SHEET NO. G2
DRAWN A.PETROSSO	
CHECKED A.CABRERA	
PROJECT NO. 12345678	SHEET 2 OF 14

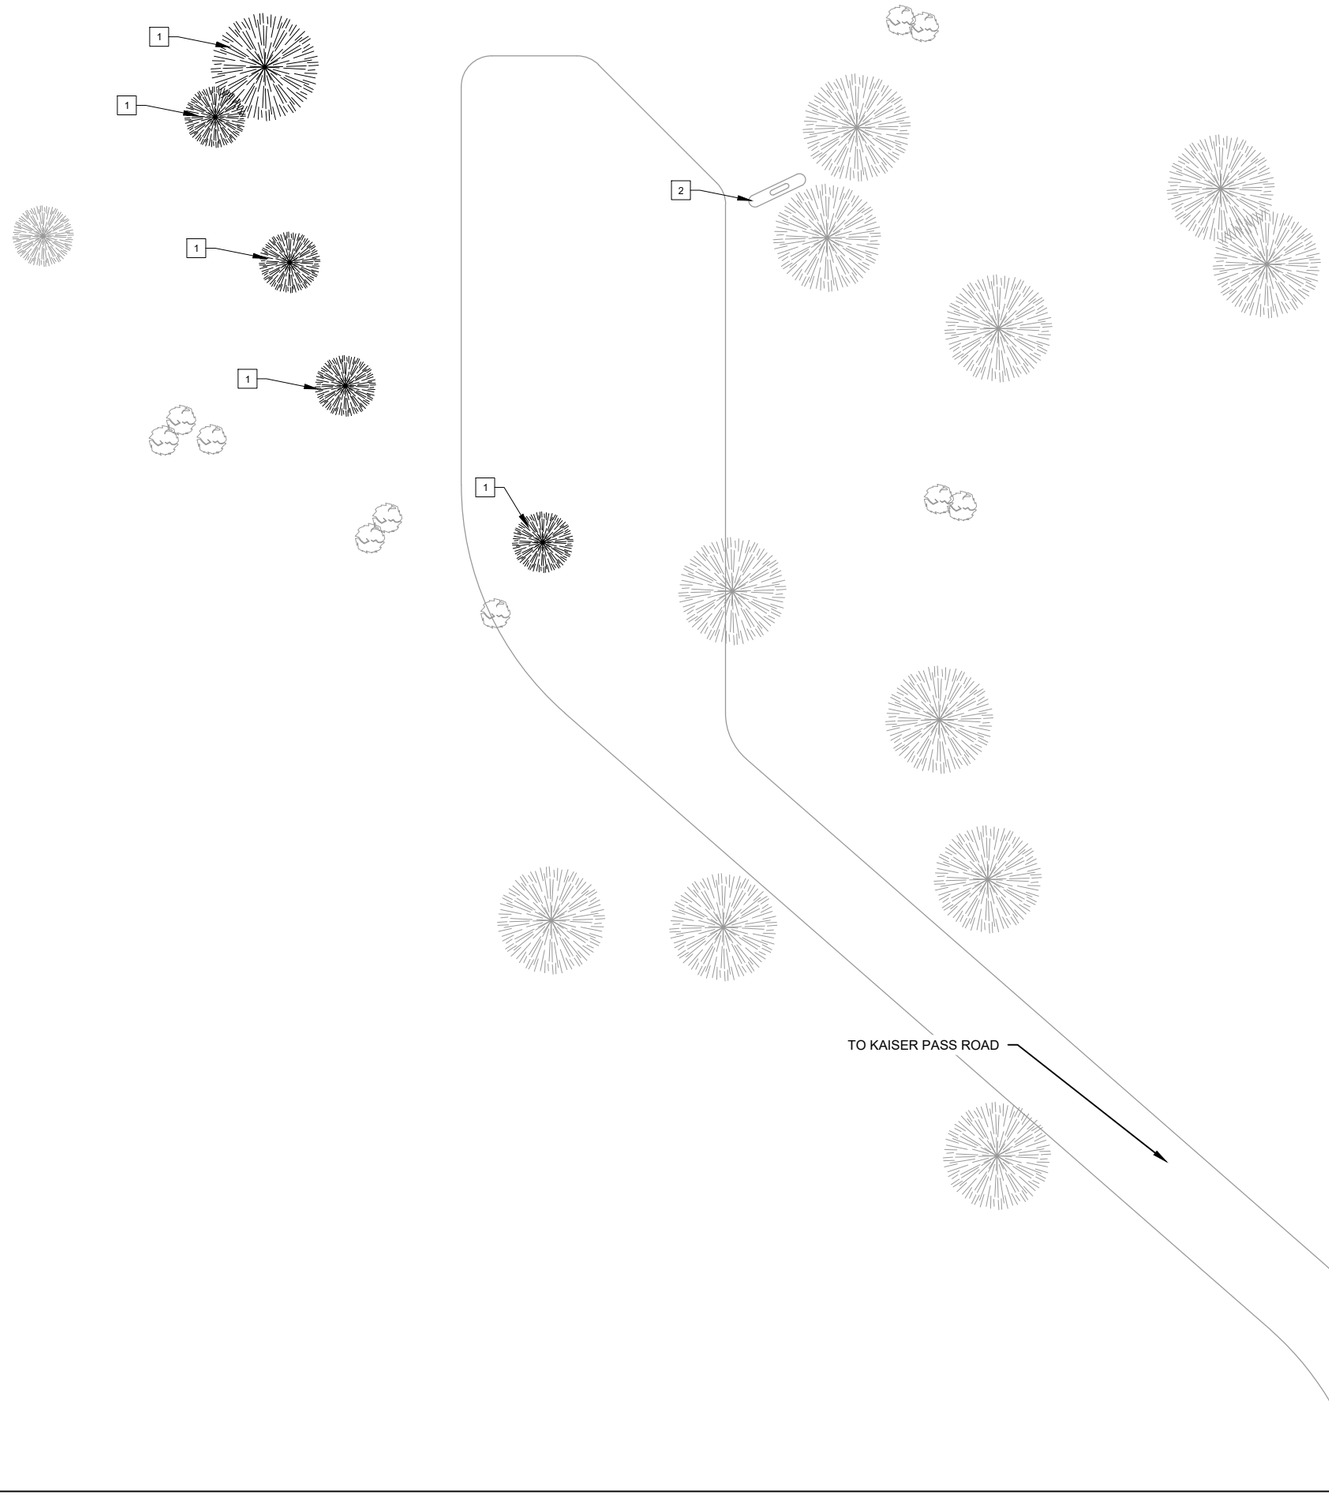

KEYNOTES	
MARK	DESCRIPTION
1	REMOVE EXISTING TREES AND VEGETATION
2	PROTECT EXISTING LPG TANK

* PLAN DOES NOT SHOW ALL EXISTING VEGETATION. REMOVE ANY ADDITIONAL VEGETATION AS NECESSARY

United States Department of Agriculture
Forest Service

(R05)
Pacific Southwest Region

STAMPS, LOGOS, AND SEALS

NO.	REVISION / ISSUE	DATE
4		
3		
2		
1		

PROJECT NAME

HS NEW BARRACKS ADMIN AND REC REHAB

Sierra National Forest


High Sierra Ranger District

DRAWING TITLE

DEMOLITION PLAN 1

DATE 2/23/2026	ARCHIVE NO.
DESIGNER A.PETROSSO	DRAWING SHEET NO. C1
DRAWN A.PETROSSO	
CHECKED A.CABRERA	
PROJECT NO. 12345678	SHEET 3 OF 14

2/23/26 15:23 ANTHONY.PETROSSO D:\REHAB NEW TINY HOMES\REHAB PLACEMENT.DWG;

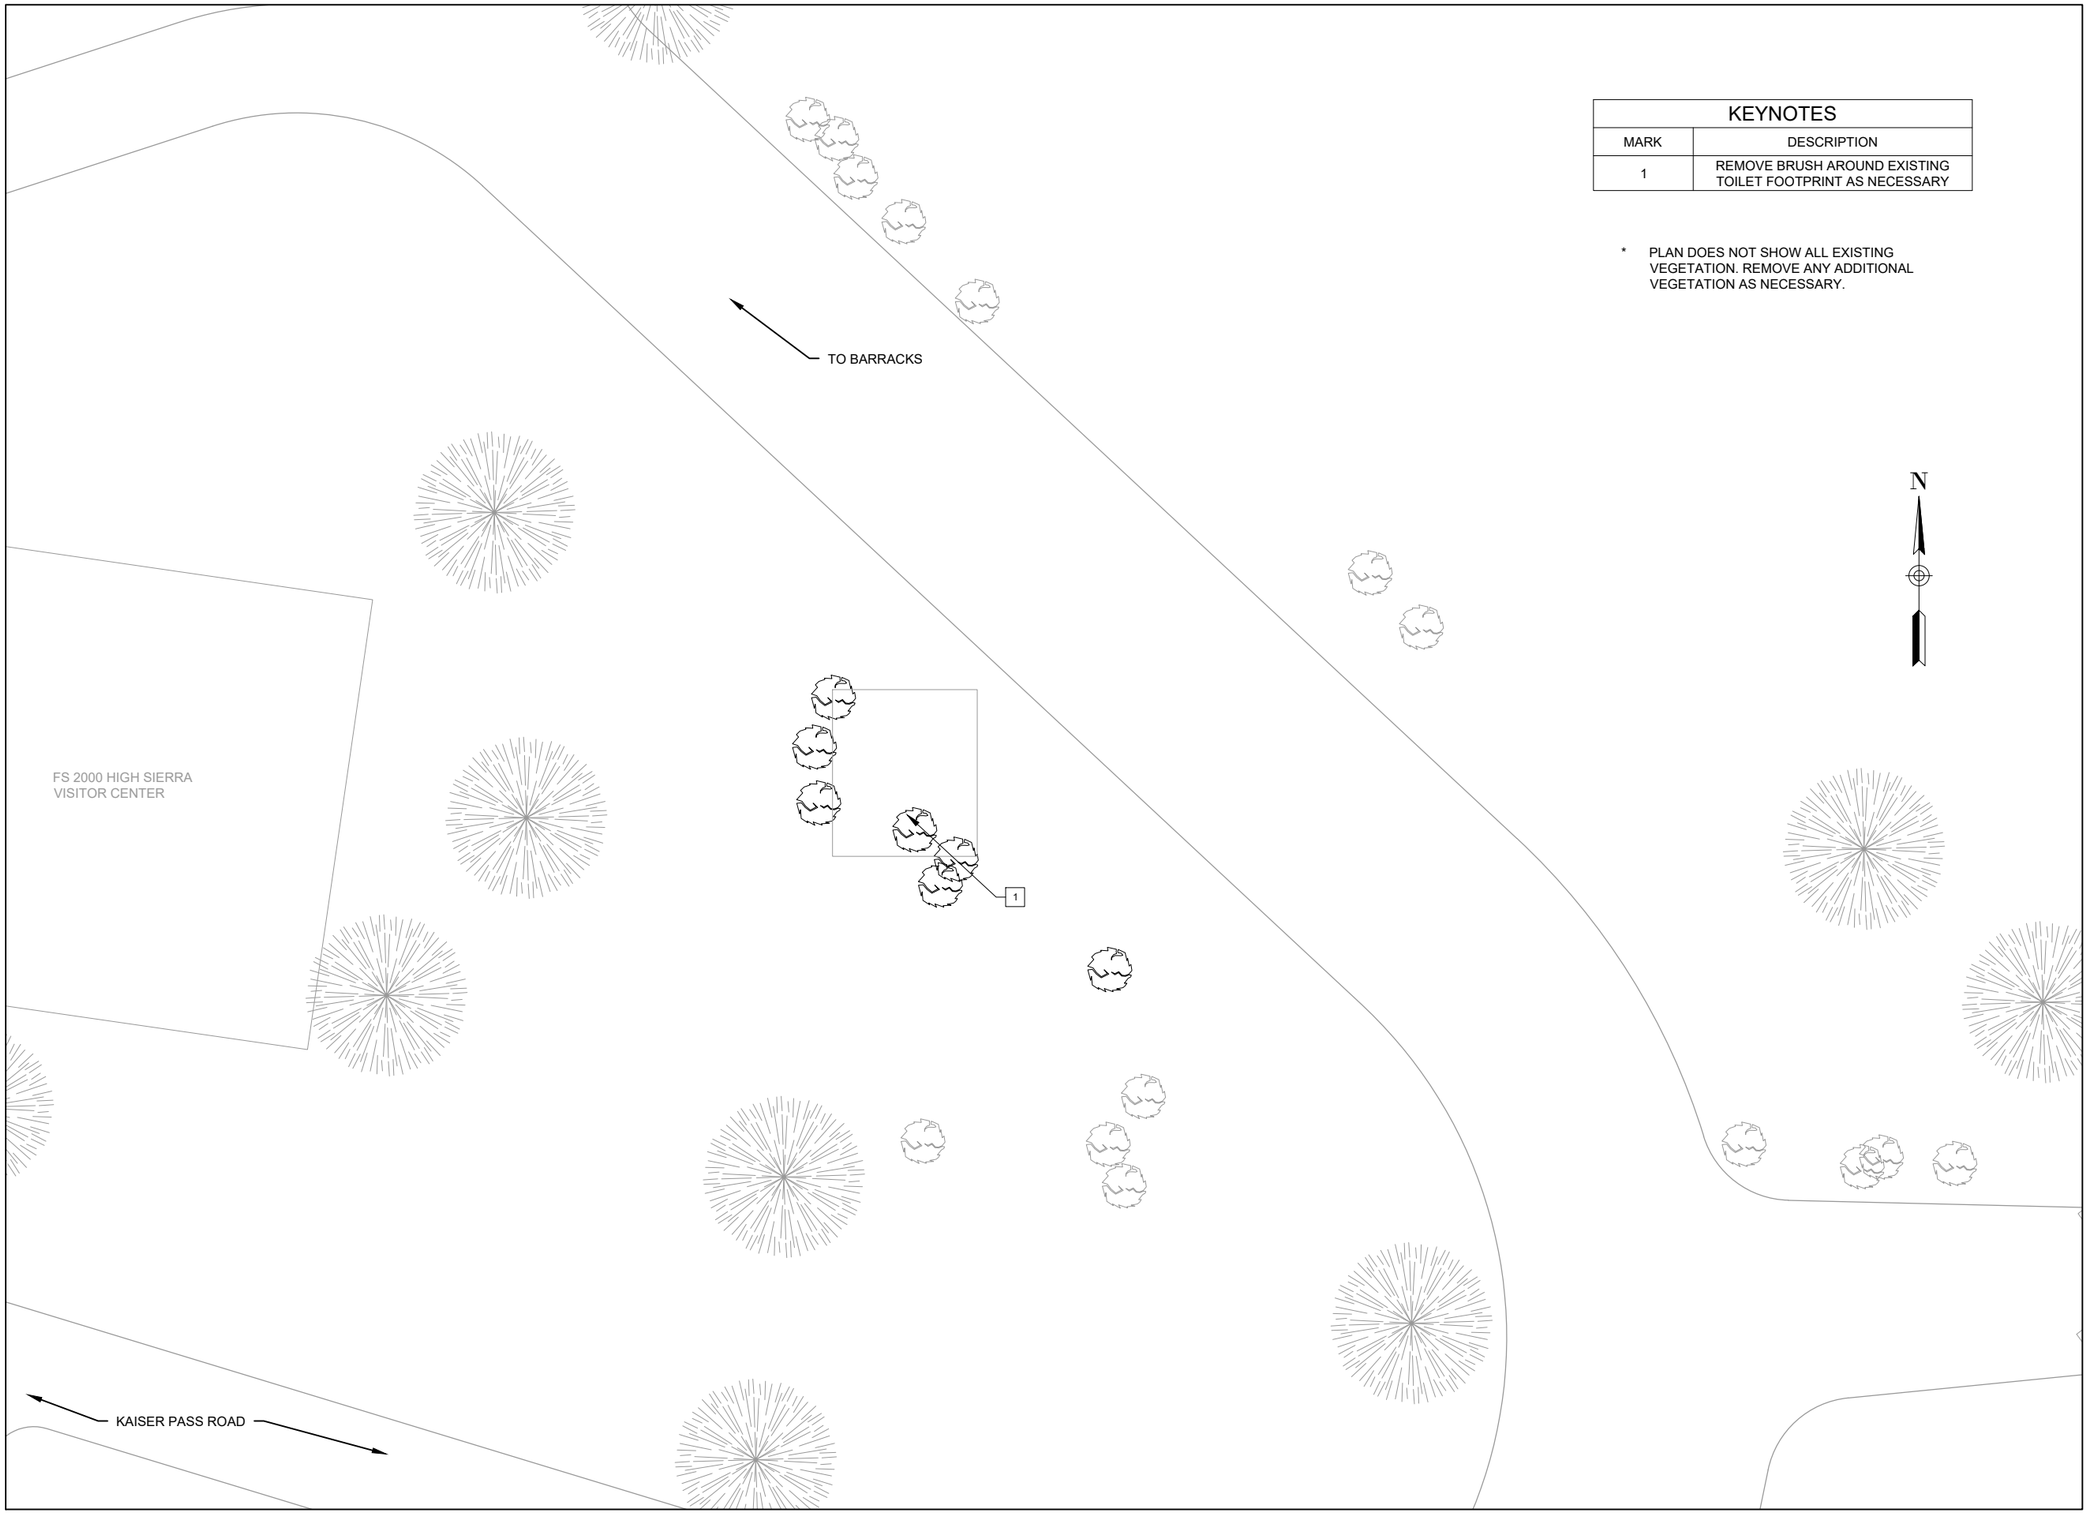

KEYNOTES	
MARK	DESCRIPTION
1	REMOVE BRUSH AROUND EXISTING TOILET FOOTPRINT AS NECESSARY

* PLAN DOES NOT SHOW ALL EXISTING VEGETATION. REMOVE ANY ADDITIONAL VEGETATION AS NECESSARY.

N

United States Department of Agriculture
Forest Service

(R05)
Pacific Southwest Region

STAMPS, LOGOS, AND SEALS

NO.	REVISION / ISSUE	DATE
4		
3		
2		
1		

PROJECT NAME

HS NEW BARRACKS ADMIN AND REC REHAB

Sierra National Forest


High Sierra Ranger District

DRAWING TITLE

DEMOLITION PLAN 2

DATE 2/23/2026	ARCHIVE NO.
DESIGNER A.PETROSSO	DRAWING SHEET NO. C2
DRAWN A.PETROSSO	
CHECKED A.CABRERA	
PROJECT NO. 12345678	SHEET 4 OF 14

2/23/26 15:23 ANTHONY PETROSSO D:\REHAB NEW TINY HOMES\REHAB PLACEMENT.DWG;

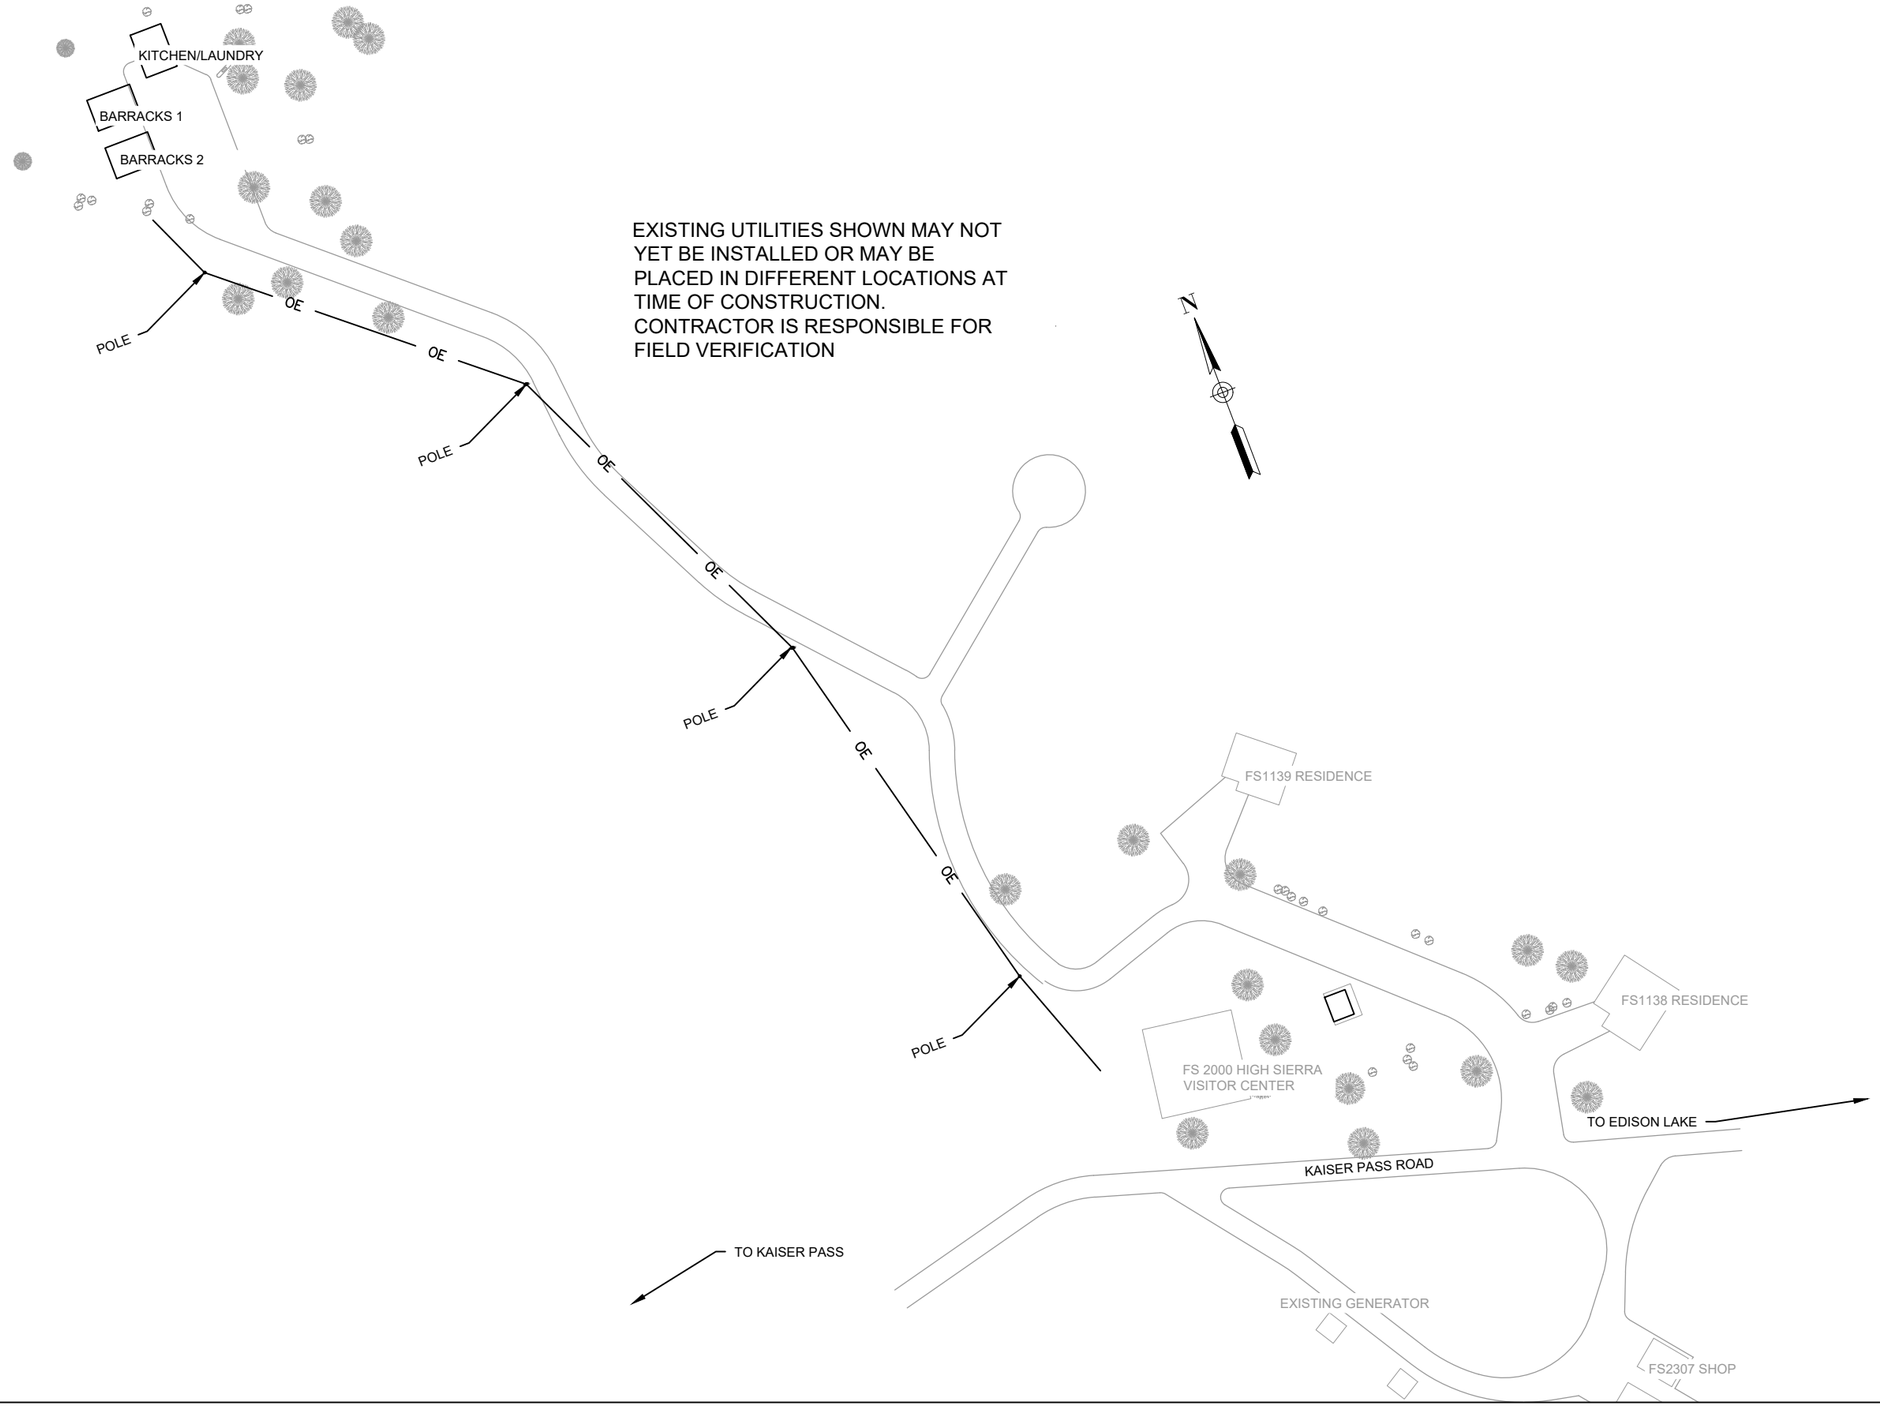

2/22/26 15:23 ANTHONY PETROSSO D:\REHAB NEW TINY HOMES\REHAB PLACEMENT.DWG;

United States Department of Agriculture
Forest Service

(R05)
Pacific Southwest Region

STAMPS, LOGOS, AND SEALS

NO.	REVISION / ISSUE	DATE
4		
3		
2		
1		

PROJECT NAME

HS NEW BARRACKS ADMIN AND REC REHAB


Sierra National Forest

High Sierra Ranger District

DRAWING TITLE

HIGH SIERRA UTILITIES

DATE 2/23/2026	ARCHIVE NO.
DESIGNER A.PETROSSO	DRAWING SHEET NO. C5
DRAWN A.PETROSSO	
CHECKED A.CABRERA	
PROJECT NO. 12345678	SHEET 5 OF 14

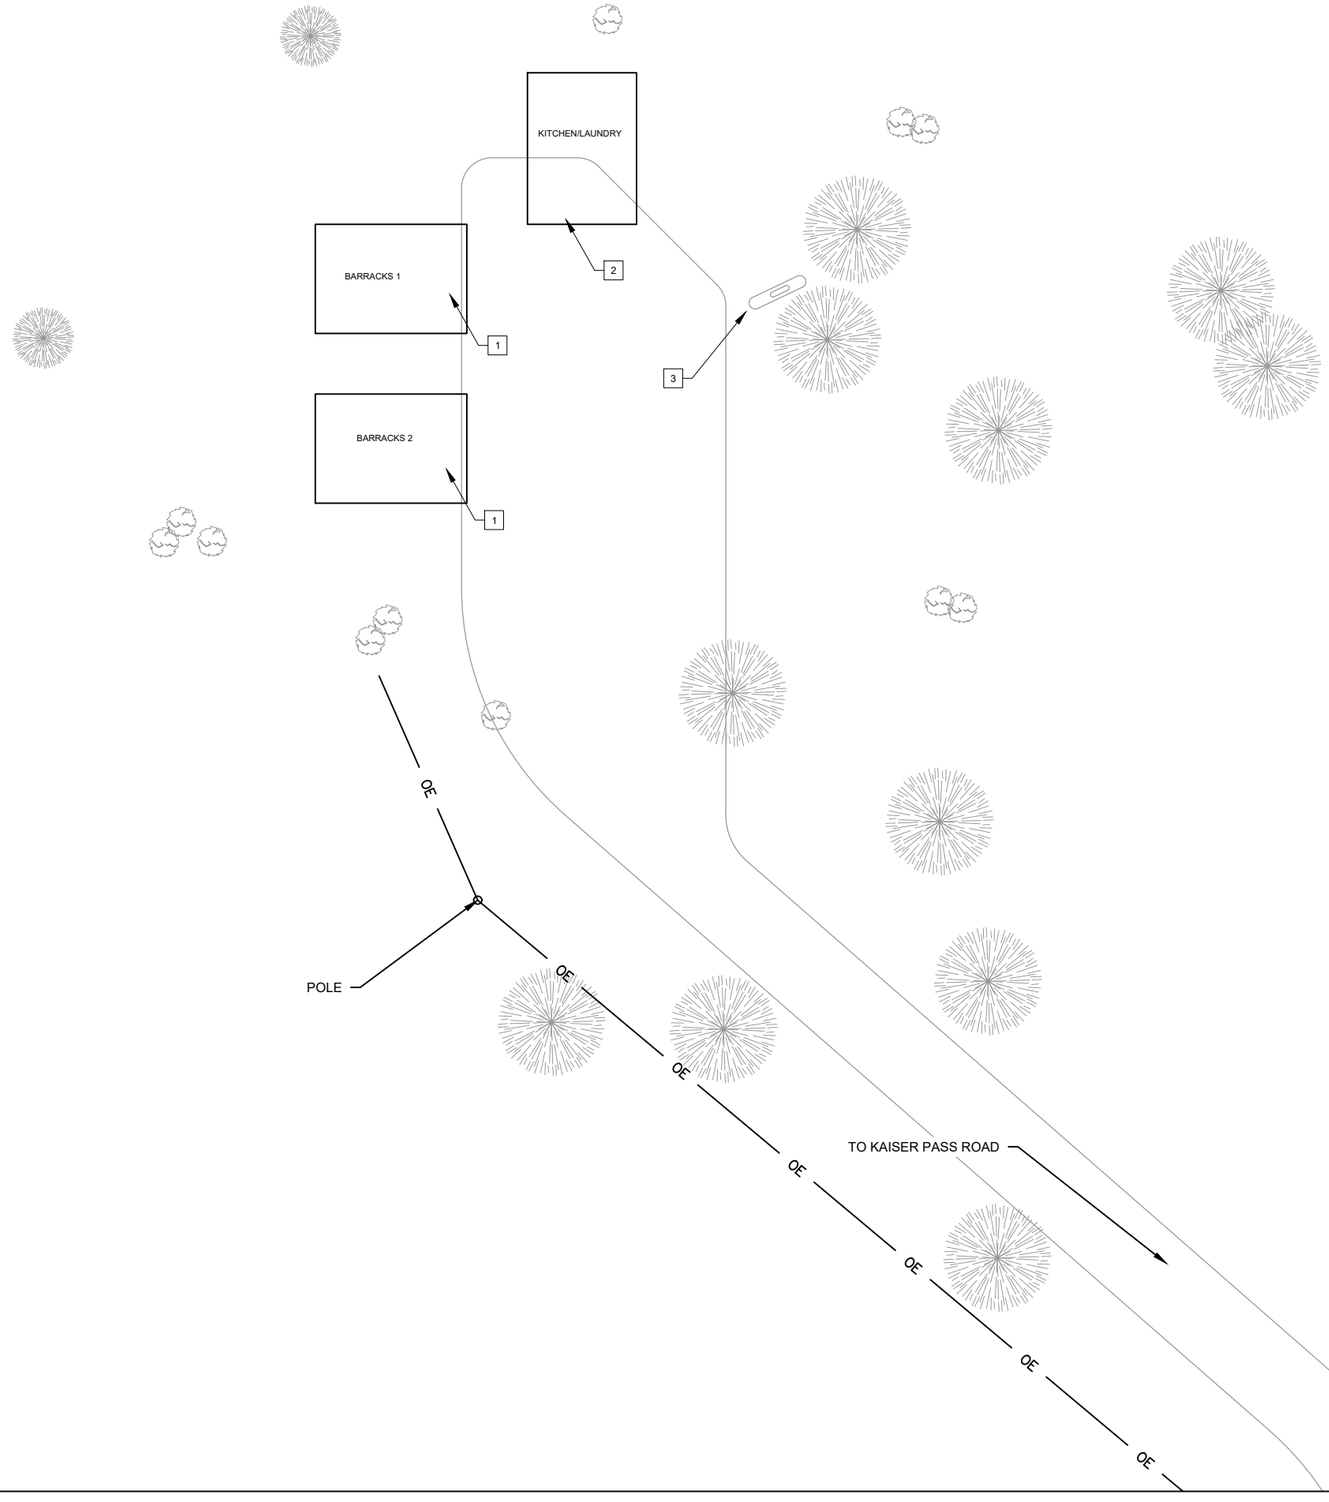

KEYNOTES	
MARK	DESCRIPTION
1	CONSTRUCT NEW ~600 SF BARRACKS BUILDING
2	CONSTRUCT NEW ~600 SF KITCHEN / LAUNDRY BUILDING
3	PROTECT EXISTING LPG TANK

United States Department of Agriculture
Forest Service

(R05)
Pacific Southwest Region

STAMPS, LOGOS, AND SEALS

NO.	REVISION / ISSUE	DATE
4		
3		
2		
1		

PROJECT NAME

HS NEW BARRACKS ADMIN AND REC REHAB

Sierra National Forest

High Sierra Ranger District


DRAWING TITLE

SITE PLAN 1

DATE 2/23/2026	ARCHIVE NO.
DESIGNER A.PETROSSO	DRAWING SHEET NO. C6
DRAWN A.PETROSSO	
CHECKED A.CABRERA	
PROJECT NO. 12345678	SHEET 6 OF 14

2/23/26 15:23 ANTHONY.PETROSSO D:\REHAB NEW TINY HOMES\REHAB PLACEMENT.DWG;

KEYNOTES	
MARK	DESCRIPTION
1	INSTALL NEW DOUBLE VAULT TOILET WITHIN EXISTING FOOTPRINT

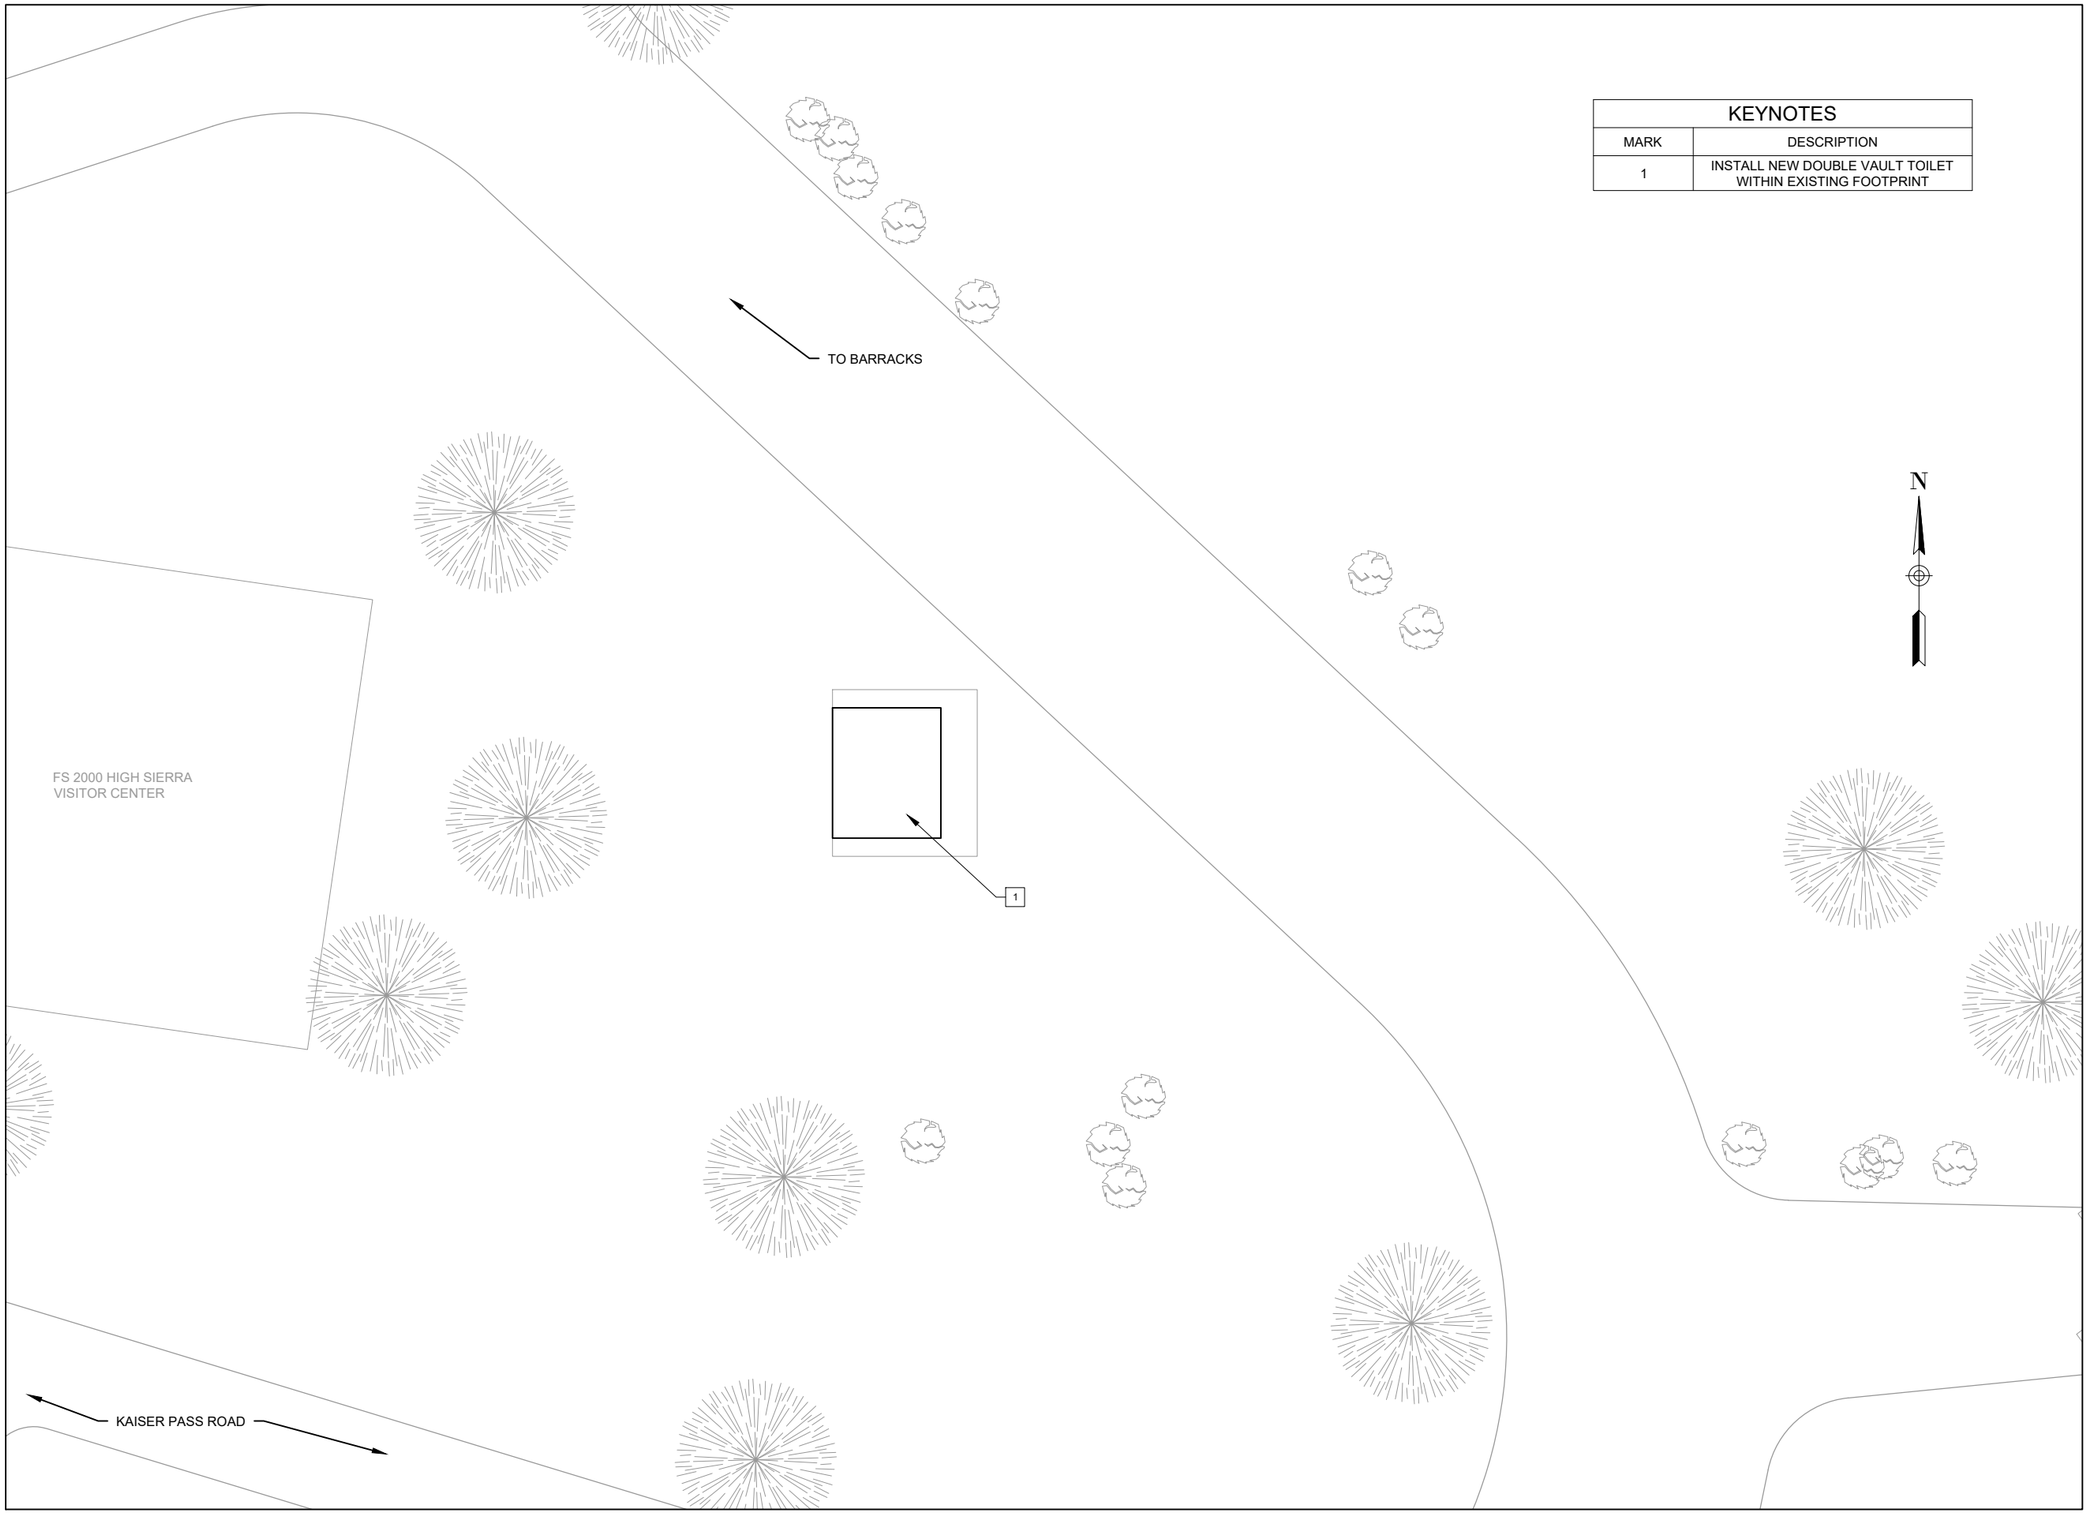

N

United States Department of Agriculture
Forest Service

(R05)
Pacific Southwest Region

STAMPS, LOGOS, AND SEALS

NO.	REVISION / ISSUE	DATE
4		
3		
2		
1		

PROJECT NAME

HS NEW BARRACKS ADMIN AND REC REHAB

Sierra National Forest


High Sierra Ranger District

DRAWING TITLE

SITE PLAN 2

DATE 2/23/2026	ARCHIVE NO.
DESIGNER A.PETROSSO	DRAWING SHEET NO. C7
DRAWN A.PETROSSO	
CHECKED A.CABRERA	
PROJECT NO. 12345678	SHEET 7 OF 14

2/23/26 15:23 ANTHONY.PETROSSO D:\REHAB NEW TINY HOMES\REHAB PLACEMENT.DWG;

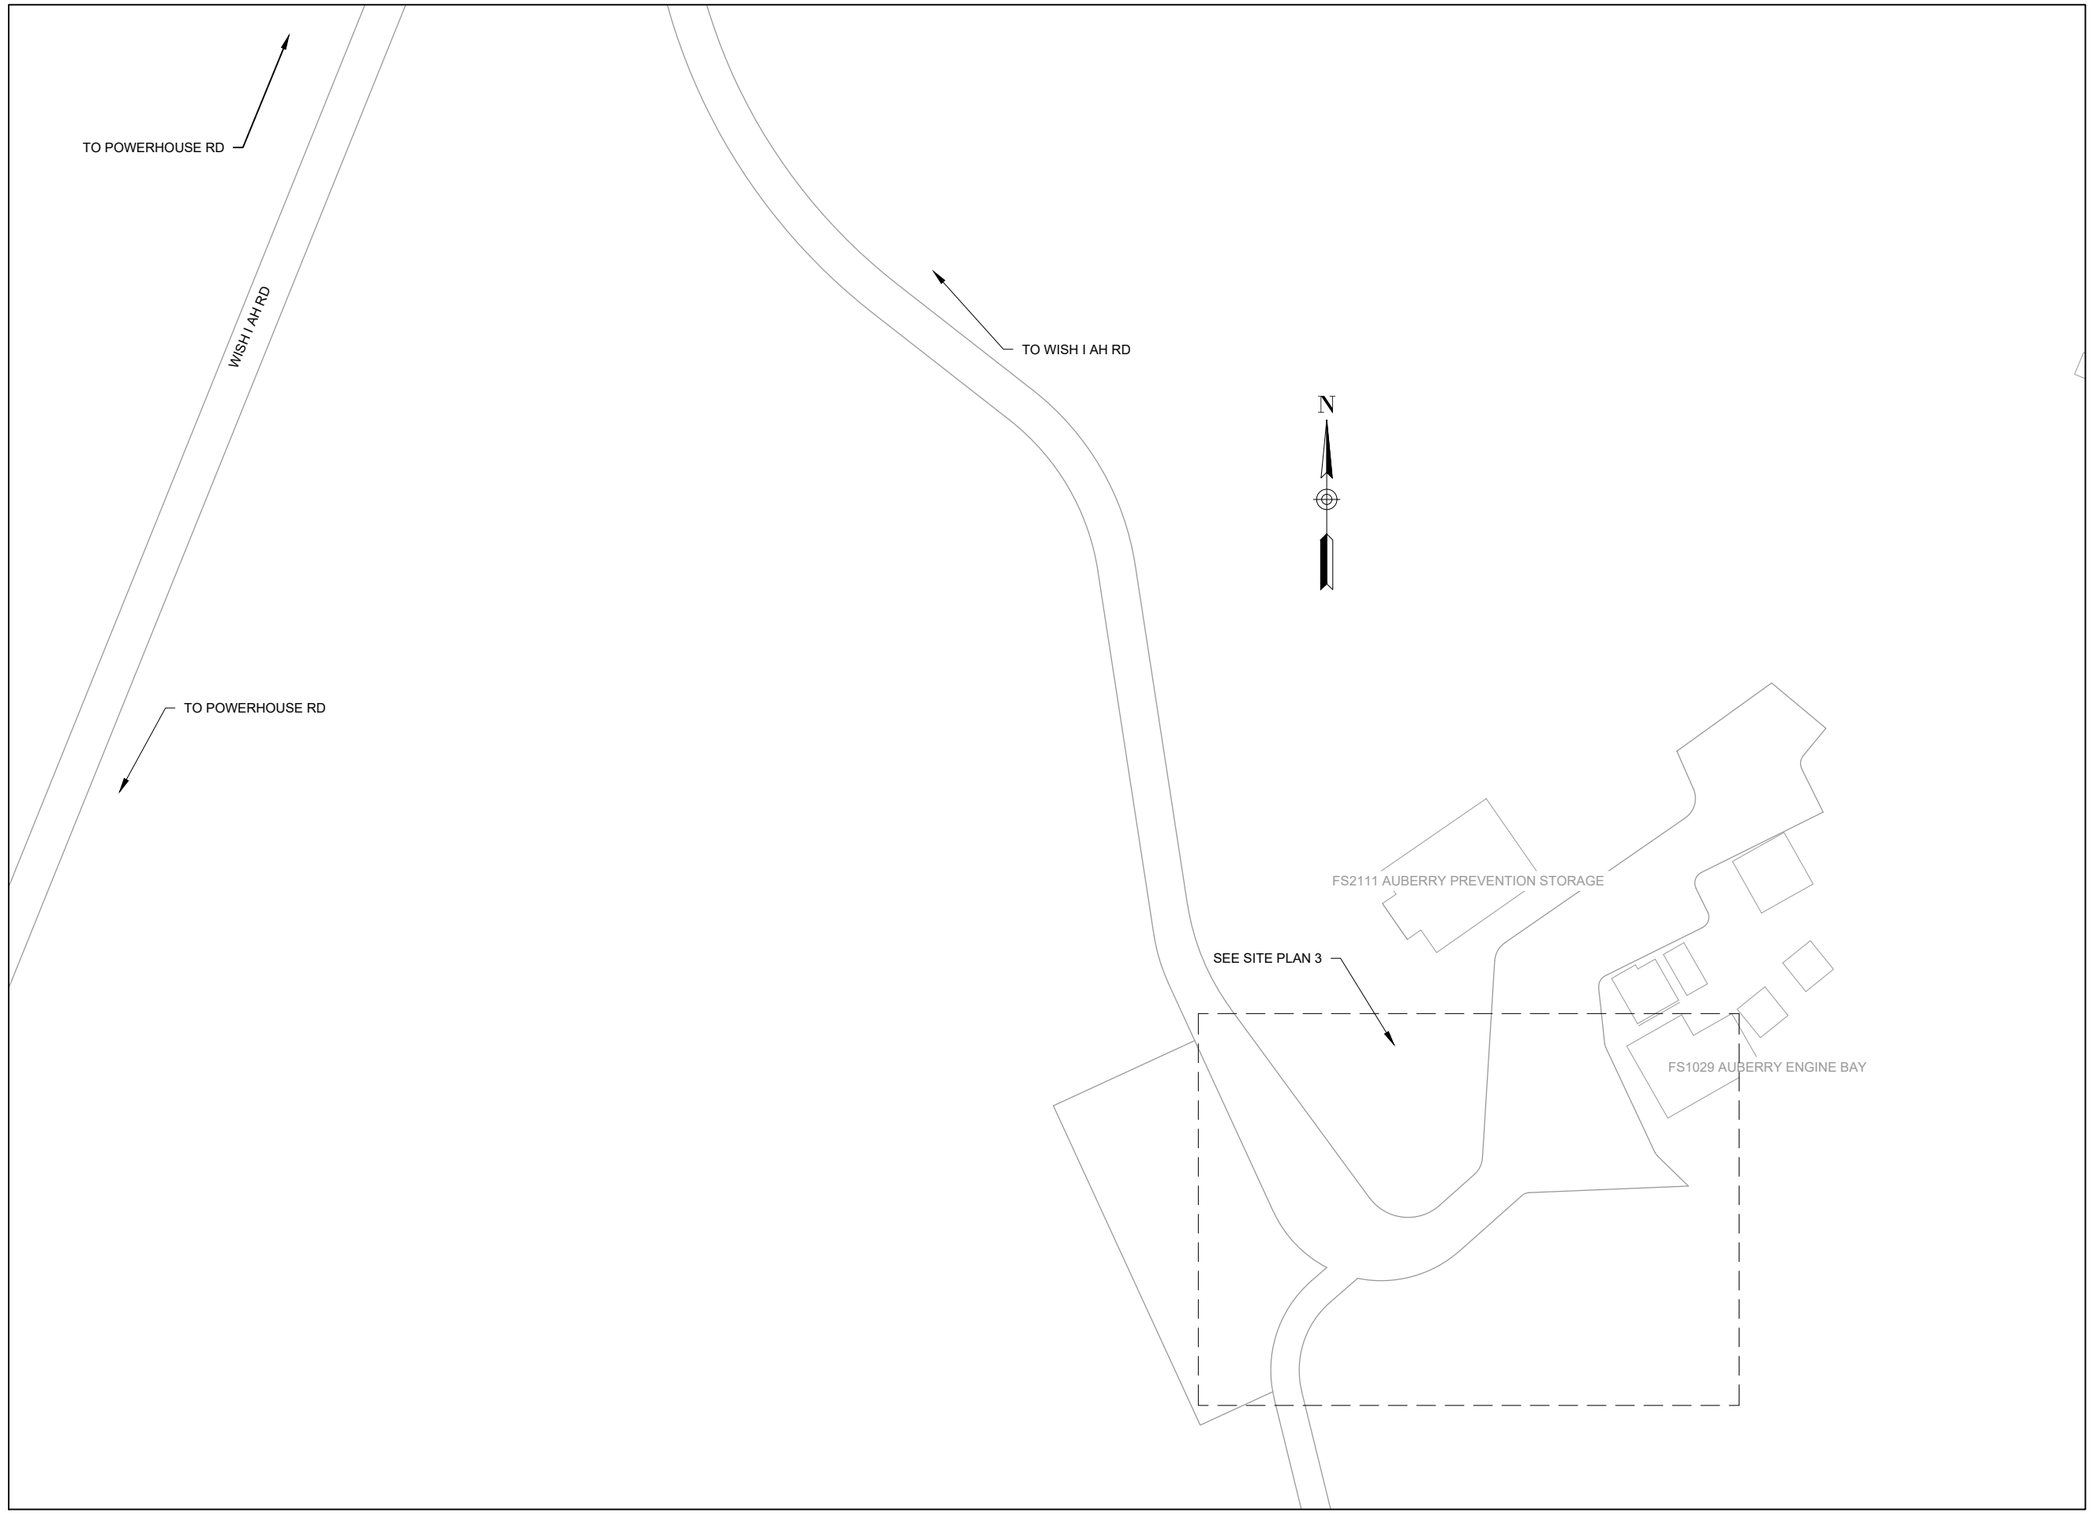

United States Department of Agriculture
Forest Service

(R05)
Pacific Southwest Region

STAMPS, LOGOS, AND SEALS

NO.	REVISION / ISSUE	DATE
4		
3		
2		
1		

PROJECT NAME

HS NEW BARRACKS ADMIN AND REC REHAB

Sierra National Forest


High Sierra Ranger District

DRAWING TITLE

AUBERRY VICINITY MAP

DATE 2/23/2026	ARCHIVE NO.
DESIGNER A.PETROSSO	DRAWING SHEET NO. G3
DRAWN A.PETROSSO	
CHECKED A.CABRERA	
PROJECT NO. 12345678	SHEET 8 OF 14

2/23/26 15:23 ANTHONY.PETROSSO D:\REHAB NEW TINY HOMES\REHAB PLACEMENT.DWG;

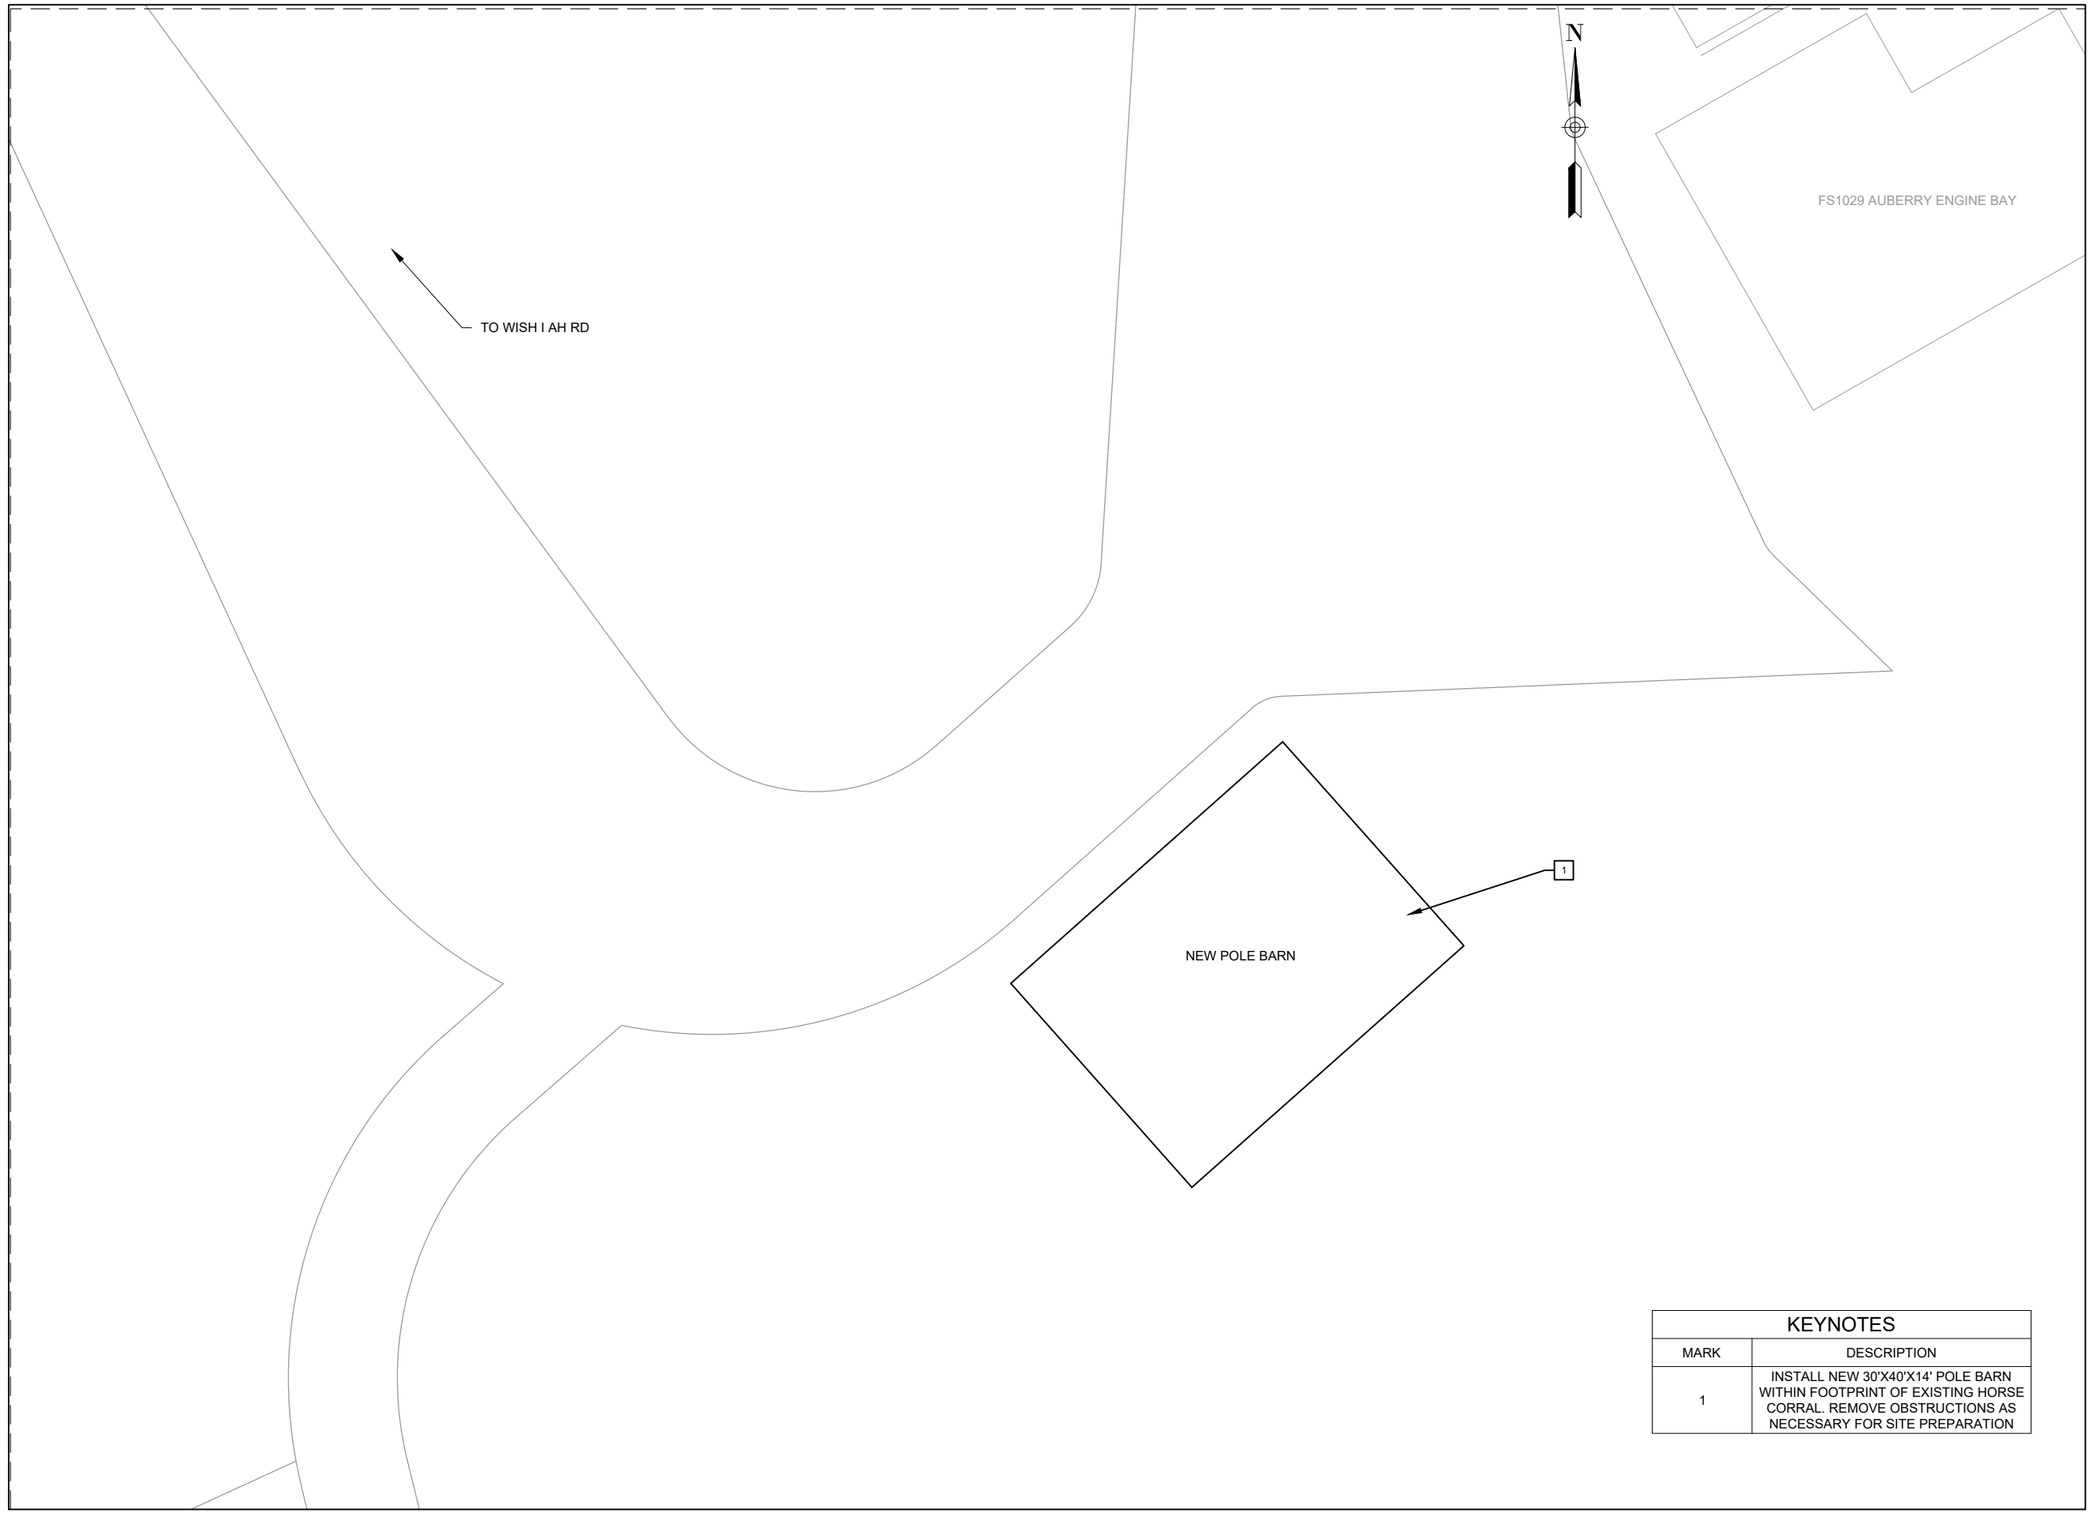

KEYNOTES	
MARK	DESCRIPTION
1	INSTALL NEW 30'X40'X14' POLE BARN WITHIN FOOTPRINT OF EXISTING HORSE CORRAL. REMOVE OBSTRUCTIONS AS NECESSARY FOR SITE PREPARATION

United States Department of Agriculture
Forest Service

(R05)
Pacific Southwest Region

STAMPS, LOGOS, AND SEALS

NO.	REVISION / ISSUE	DATE
4		
3		
2		
1		

PROJECT NAME

HS NEW BARRACKS ADMIN AND REC REHAB

Sierra National Forest


High Sierra Ranger District

DRAWING TITLE

SITE PLAN 3

DATE 2/23/2026	ARCHIVE NO.
DESIGNER A.PETROSSO	DRAWING SHEET NO. C8
DRAWN A.PETROSSO	
CHECKED A.CABRERA	
PROJECT NO. 12345678	SHEET 9 OF 14

2/23/26 15:23 ANTHONY.PETROSSO D:\REHAB NEW TINY HOMES\REHAB PLACEMENT.DWG;

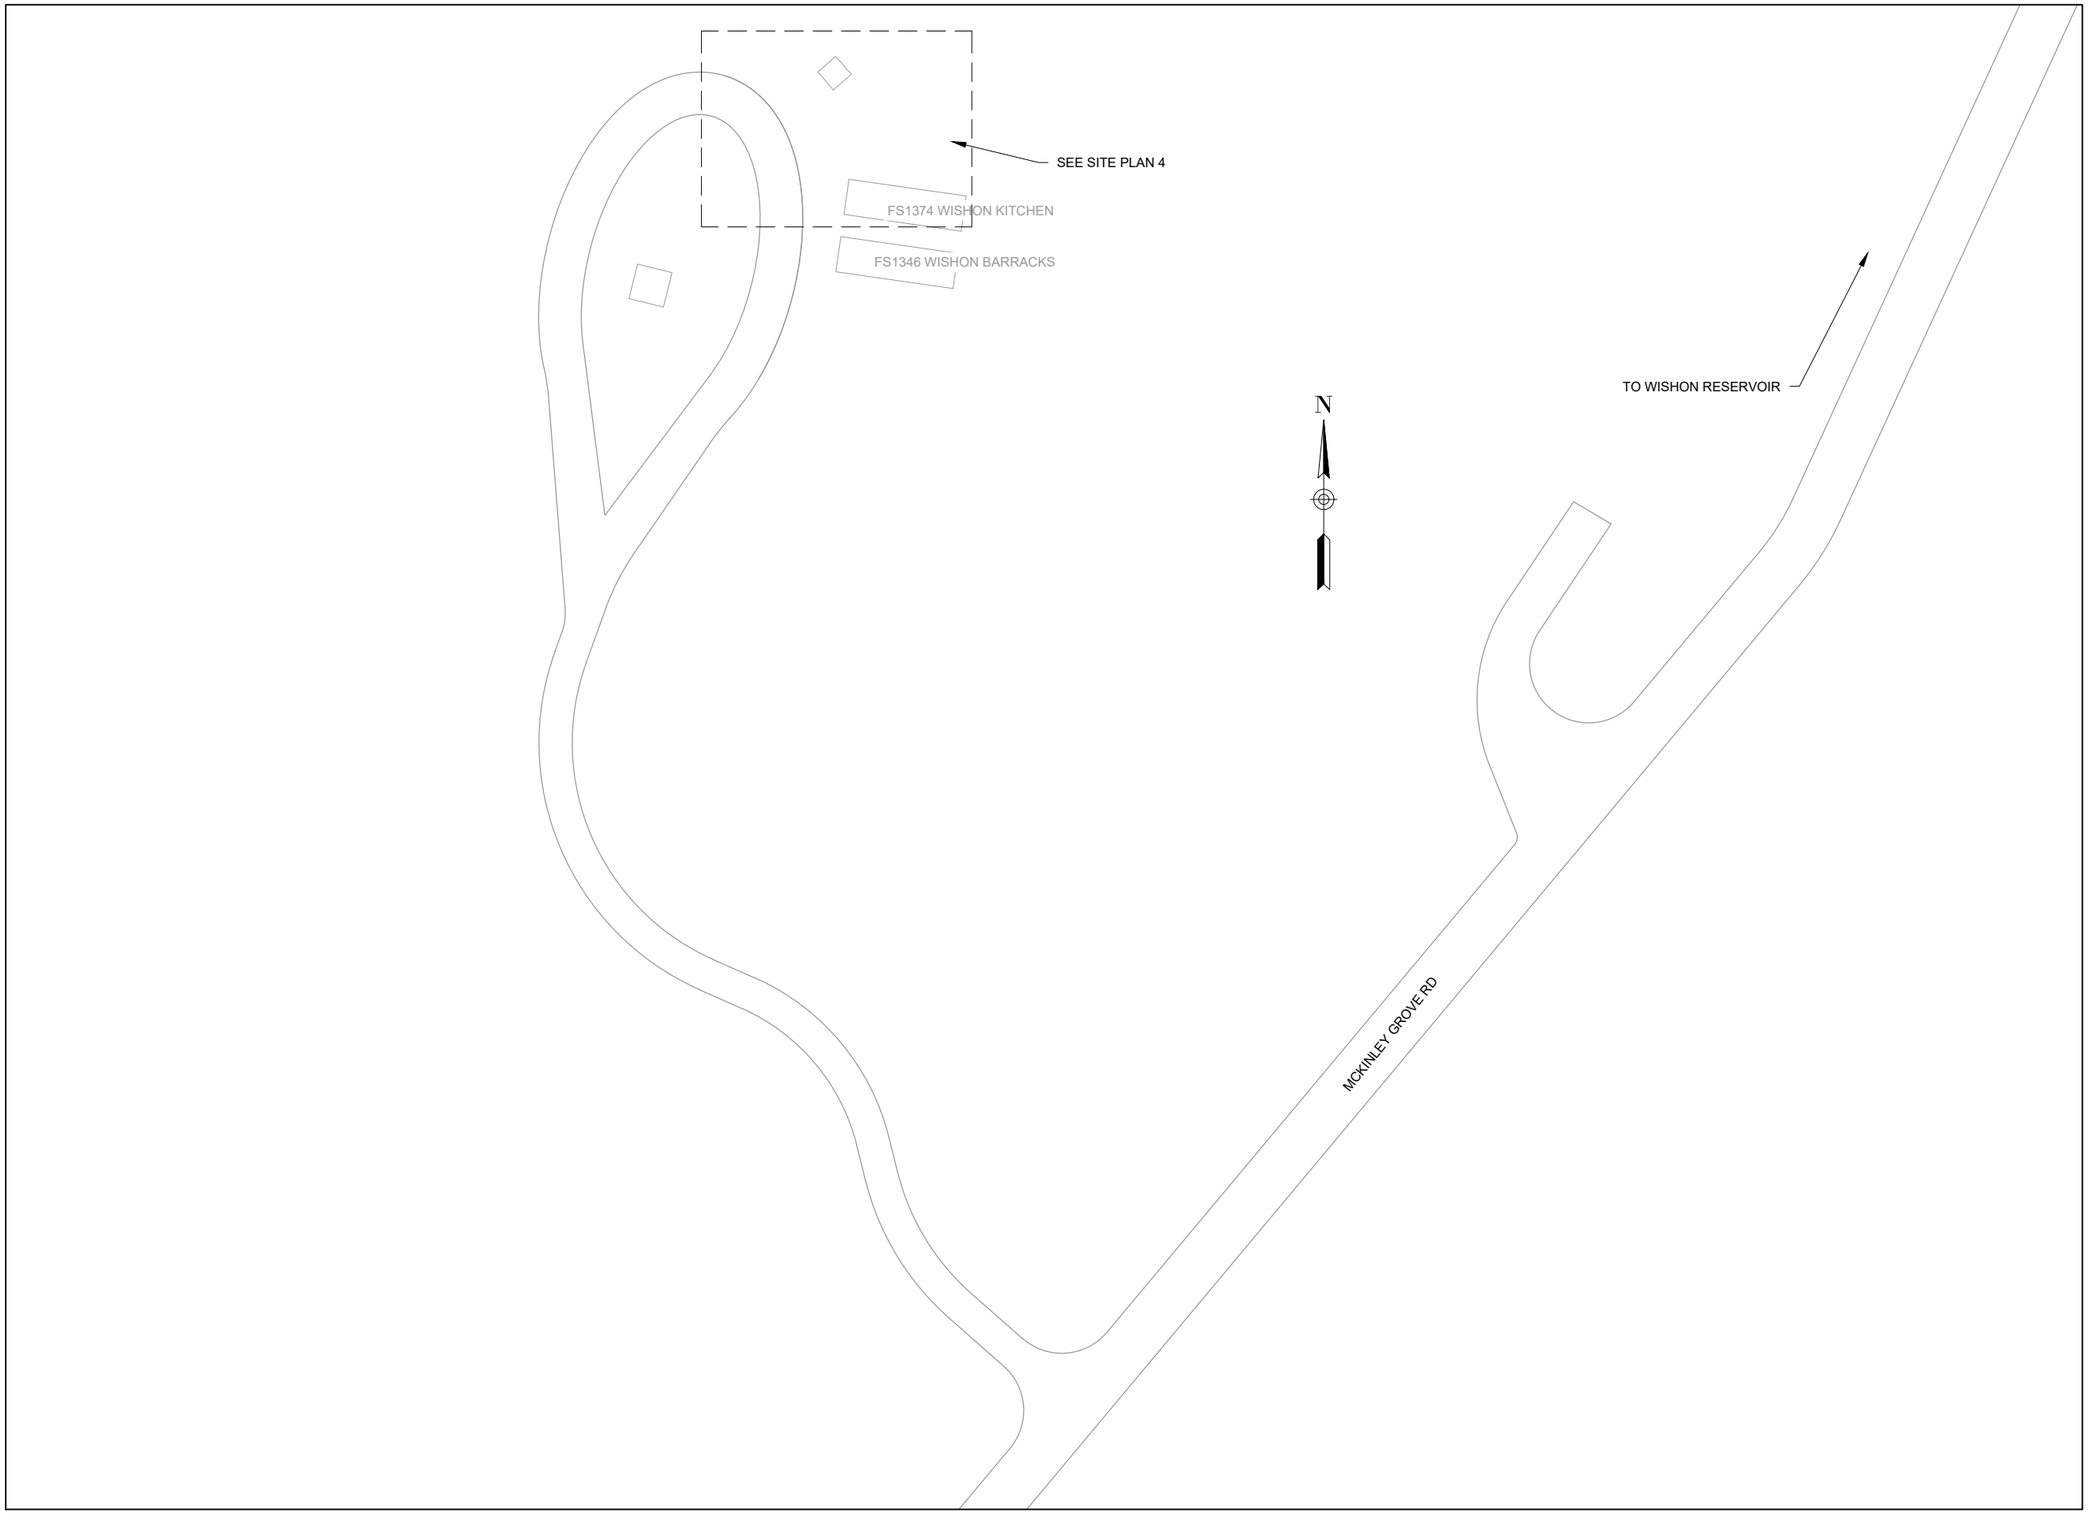

2/22/26 15:23 ANTHONY PETROSSO D:\REHAB NEW TINY HOMES\REHAB PLACEMENT.DWG;

United States Department of Agriculture
Forest Service

(R05)
Pacific Southwest Region

STAMPS, LOGOS, AND SEALS

NO.	REVISION / ISSUE	DATE
4		
3		
2		
1		

PROJECT NAME

HS NEW BARRACKS ADMIN AND REC REHAB

Sierra National Forest

High Sierra Ranger District


DRAWING TITLE


WISHON VICINITY MAP

DATE 2/23/2026	ARCHIVE NO.
DESIGNER A.PETROSSO	DRAWING SHEET NO. G4
DRAWN A.PETROSSO	
CHECKED A.CABRERA	
PROJECT NO. 12345678	SHEET 10 OF 14

N

KEYNOTES	
MARK	DESCRIPTION
1	INSTALL 6'X8' GENERATOR SHED ON EXISTING CONCRETE PAD.

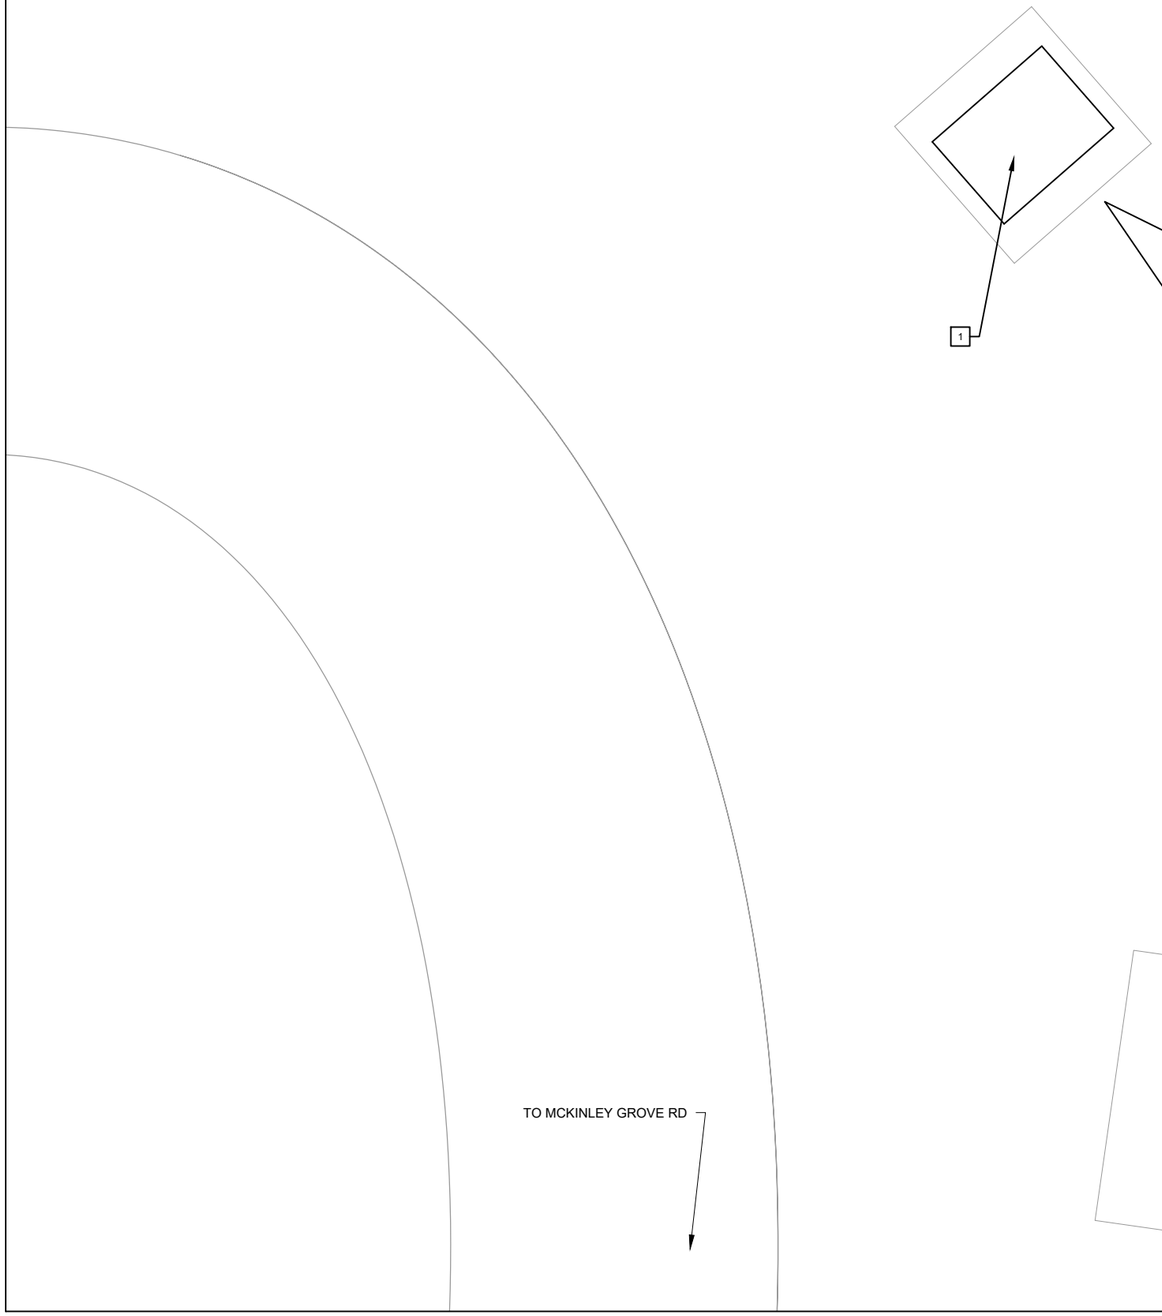

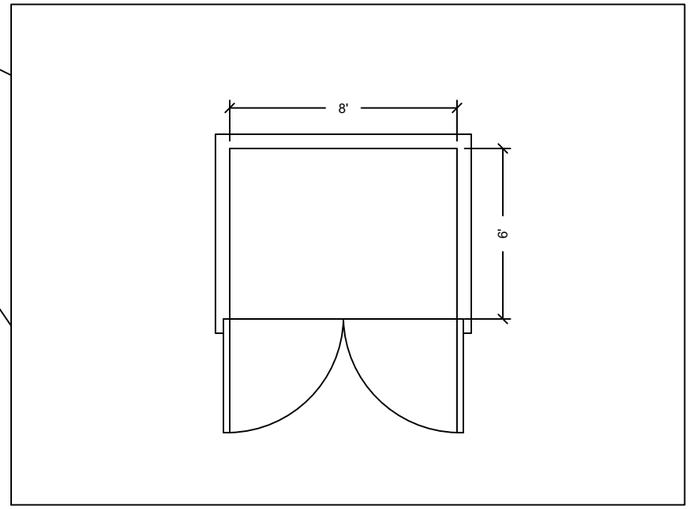

PROPOSED GENERATOR SHED FLOOR PLAN (NTS)

United States Department of Agriculture
Forest Service

(R05)
Pacific Southwest Region

STAMPS, LOGOS, AND SEALS

NO.	REVISION / ISSUE	DATE
4		
3		
2		
1		

PROJECT NAME

HS NEW BARRACKS ADMIN AND REC REHAB

Sierra National Forest

High Sierra Ranger District

DRAWING TITLE

SITE PLAN 4


DATE 2/23/2026	ARCHIVE NO.
DESIGNER A.PETROSSO	DRAWING SHEET NO. C9
DRAWN A.PETROSSO	
CHECKED A.CABRERA	
PROJECT NO. 12345678	SHEET 11 OF 14

2/23/26 15:23 ANTHONY PETROSSO D:\REHAB NEW TINY HOMES\REHAB PLACEMENT.DWG;


PLAN 2508R

www.dreamhomeplans.com

DREAM HOME PLANS

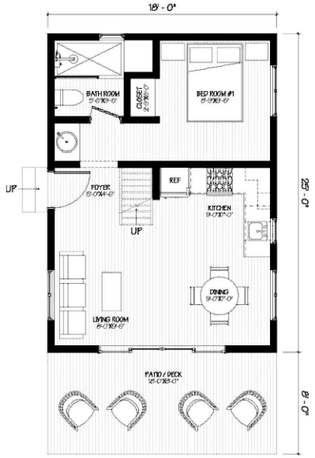


1 Ground Floor Plan
1/2" = 1'-0" 450 SQFT

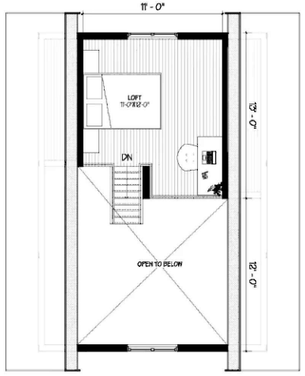


2 Loft Floor Plan
1/2" = 1'-0" 140 SQFT

CAD PLANS



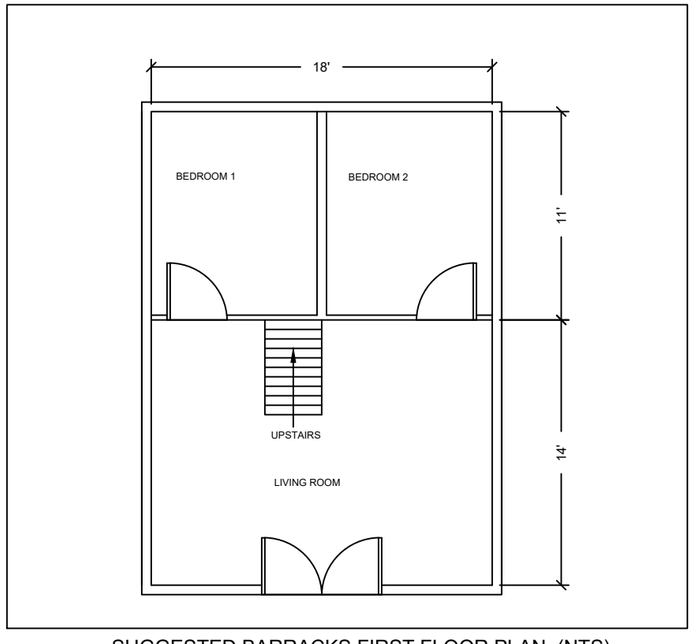

SUGGESTED BARRACKS FIRST FLOOR PLAN (NTS)

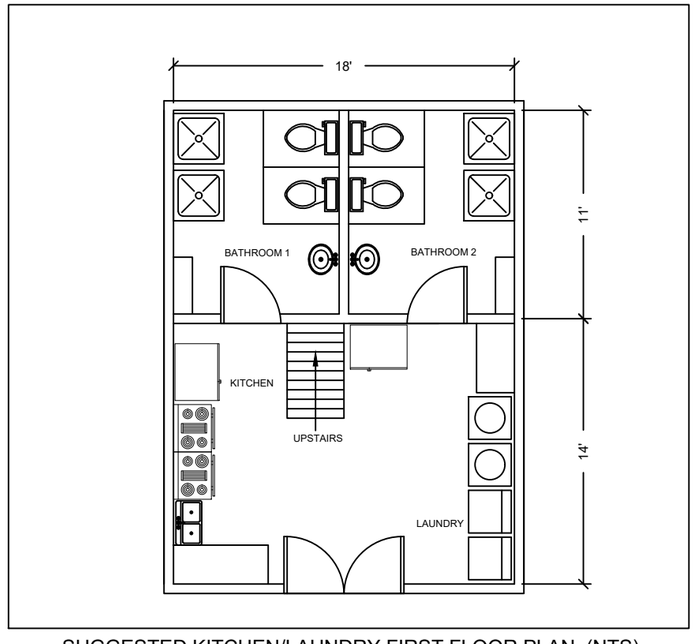

SUGGESTED KITCHEN/LAUNDRY FIRST FLOOR PLAN (NTS)

United States Department of Agriculture
Forest Service

(R05)
Pacific Southwest Region

STAMPS, LOGOS, AND SEALS

NO.	REVISION / ISSUE	DATE
4		
3		
2		
1		

PROJECT NAME

HS NEW BARRACKS ADMIN AND REC REHAB

Sierra National Forest

High Sierra Ranger District

DRAWING TITLE

POTENTIAL BARRACKS LAYOUT AND ELEVATION

DATE 2/23/2026	ARCHIVE NO.
DESIGNER	DRAWING SHEET NO. Z1
DRAWN	
CHECKED	
PROJECT NO. 12345678	SHEET 12 OF 14

2/22/26 15:23 ANTHONY PETROSSO D:\REHAB NEW TINY HOMES\REHAB PLACEMENT.DWG;





United States Department of Agriculture
Forest Service

(R05)
Pacific Southwest Region

STAMPS, LOGOS, AND SEALS

NO.	REVISION / ISSUE	DATE
4		
3		
2		
1		

PROJECT NAME

HS NEW BARRACKS ADMIN AND REC REHAB

Sierra National Forest


High Sierra Ranger District


DRAWING TITLE

PROPOSED TOILET

DATE 2/23/2026	ARCHIVE NO.
DESIGNER	DRAWING SHEET NO. Z2
DRAWN	
CHECKED	
PROJECT NO. 12345678	SHEET 13 OF 14

2/23/26 15:23 ANTHONY.PETROSSO D:\REHAB NEW TINY HOMES\REHAB PLACEMENT.DWG;

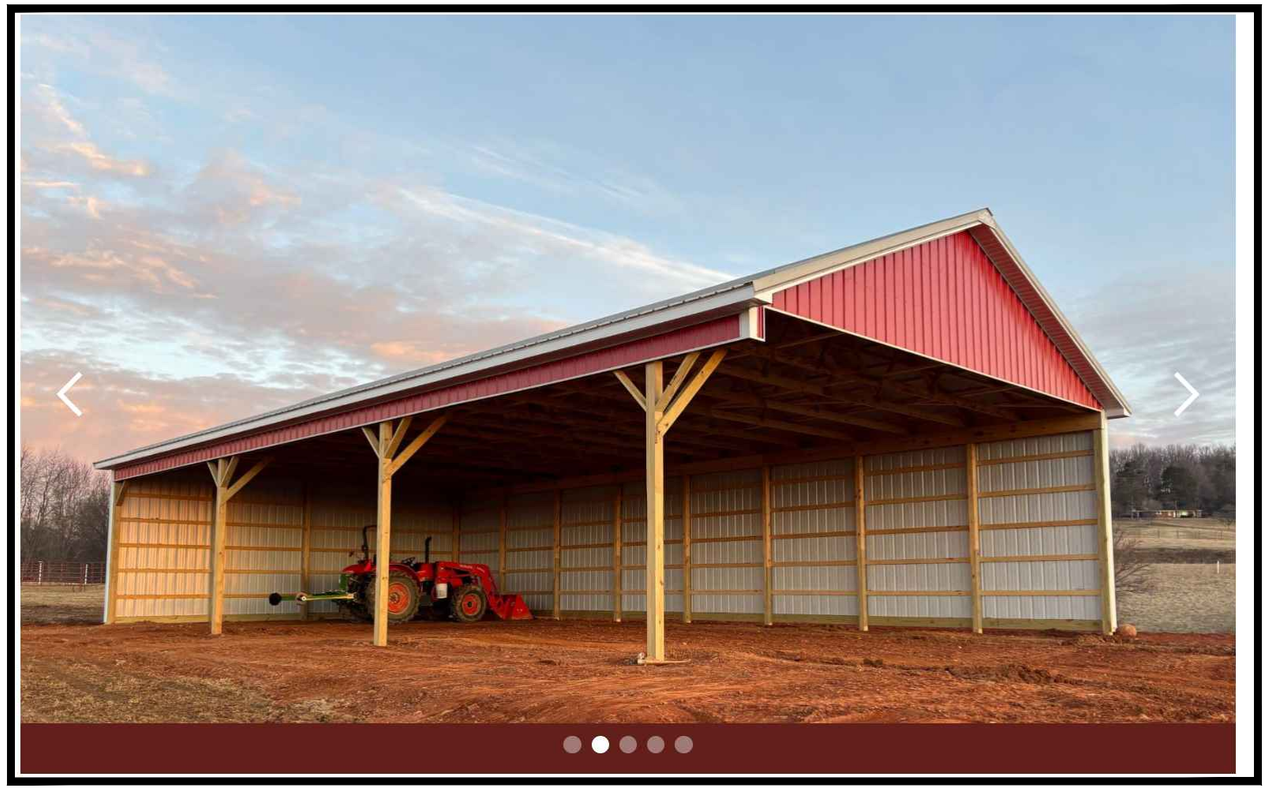

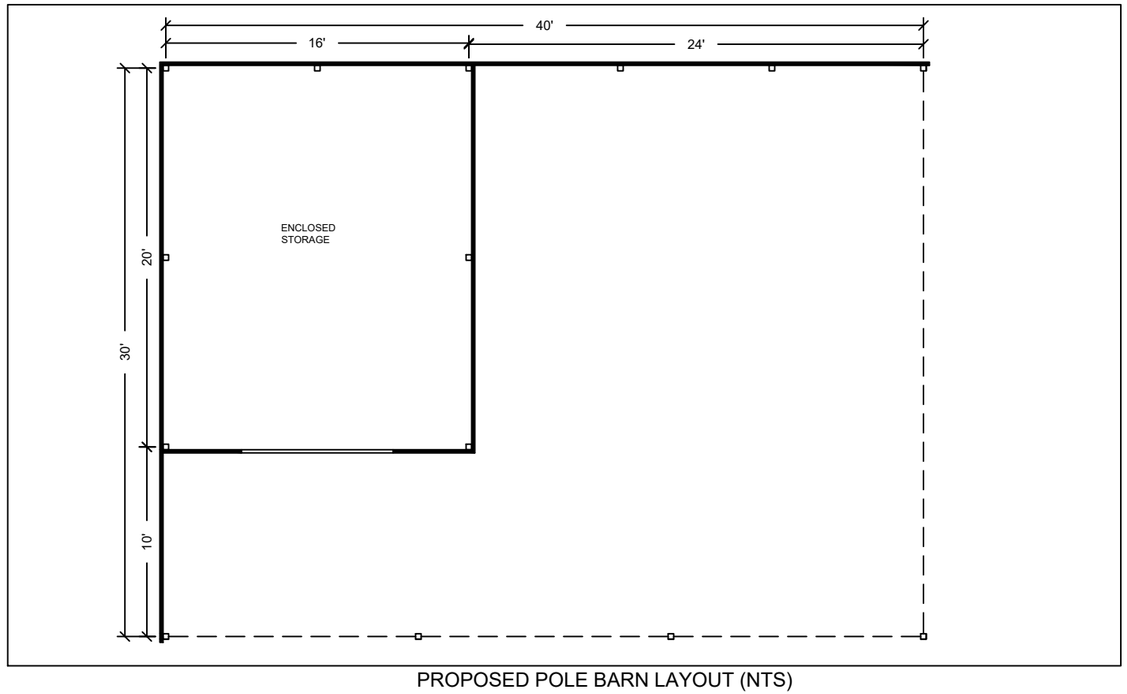

PROPOSED POLE BARN LAYOUT (NTS)

United States Department of Agriculture
Forest Service

(R05)
Pacific Southwest Region

STAMPS, LOGOS, AND SEALS

NO.	REVISION / ISSUE	DATE
4		
3		
2		
1		

PROJECT NAME

HS NEW BARRACKS ADMIN AND REC REHAB

Sierra National Forest

High Sierra Ranger District

DRAWING TITLE

PROPOSED POLE BARN

DATE 2/23/2026	ARCHIVE NO.
DESIGNER	DRAWING SHEET NO. **Z3**
DRAWN	
CHECKED	
PROJECT NO. 12345678	SHEET 14 OF 14

2/22/26 15:23 ANTHONY PETROSSO D:\REHAB NEW TINY HOMES\REHAB PLACEMENT.DWG;